SeaView Garden Villas

Type 1 (216.9 m²)

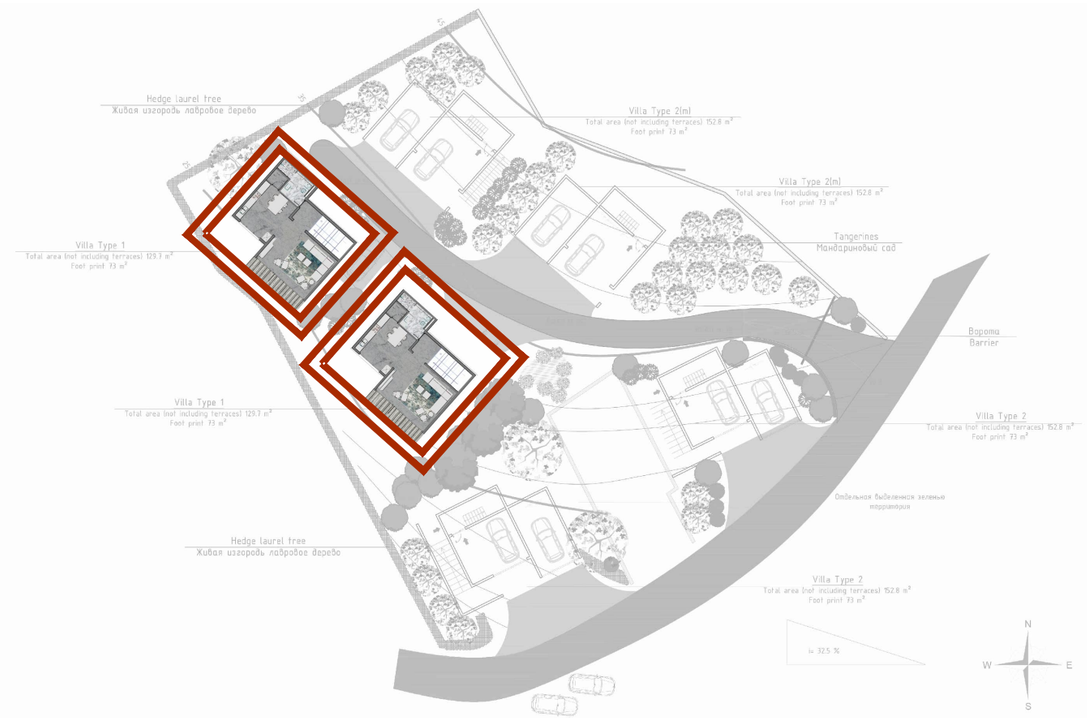

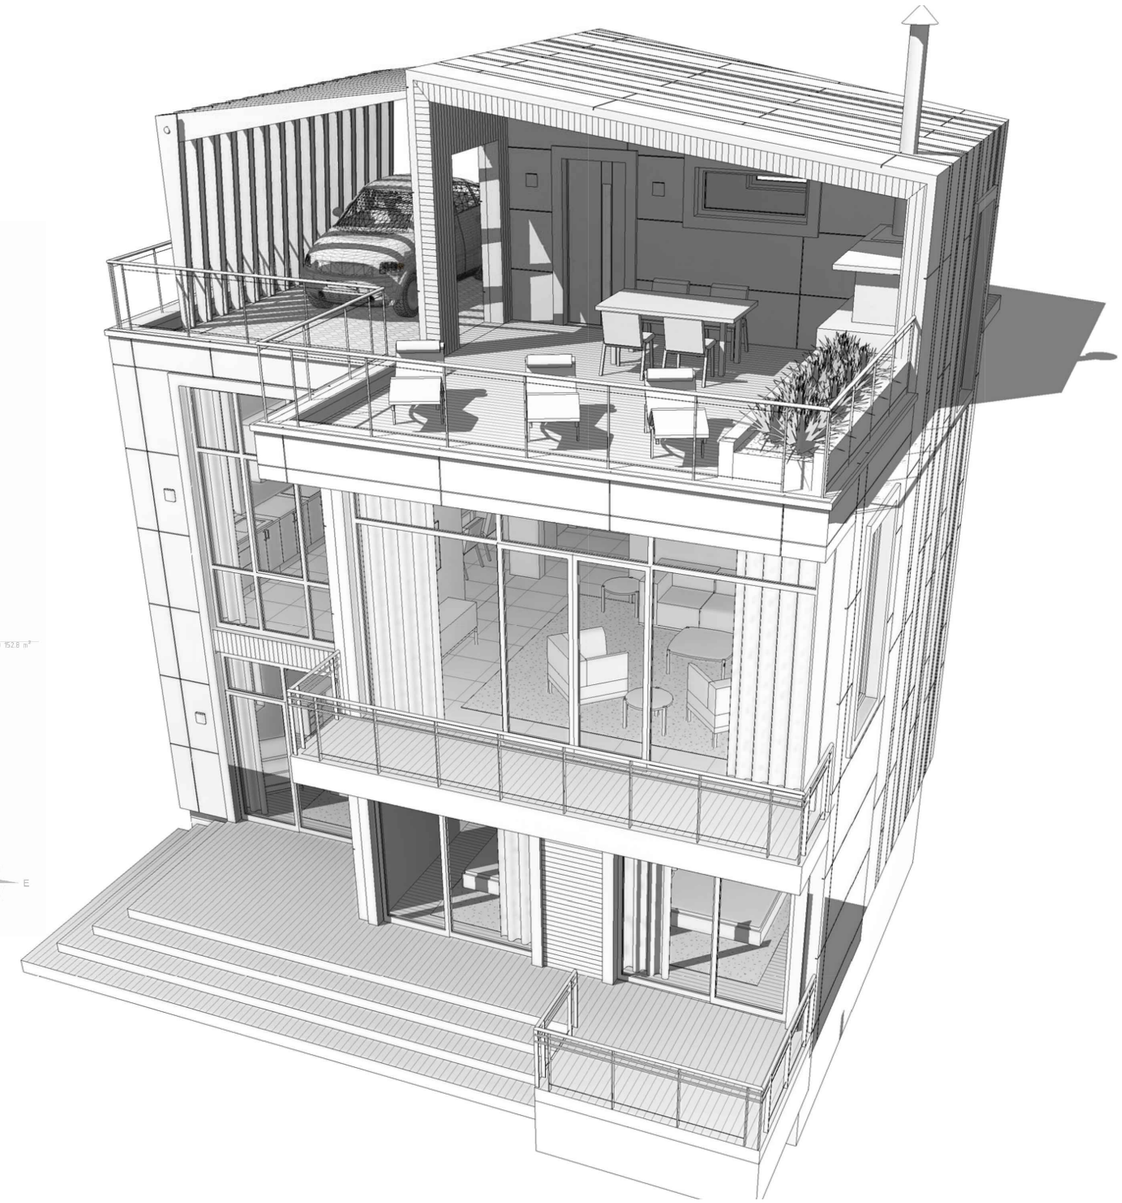

L.B.O.S.
DESIGN

L.B.O.S.
DESIGN

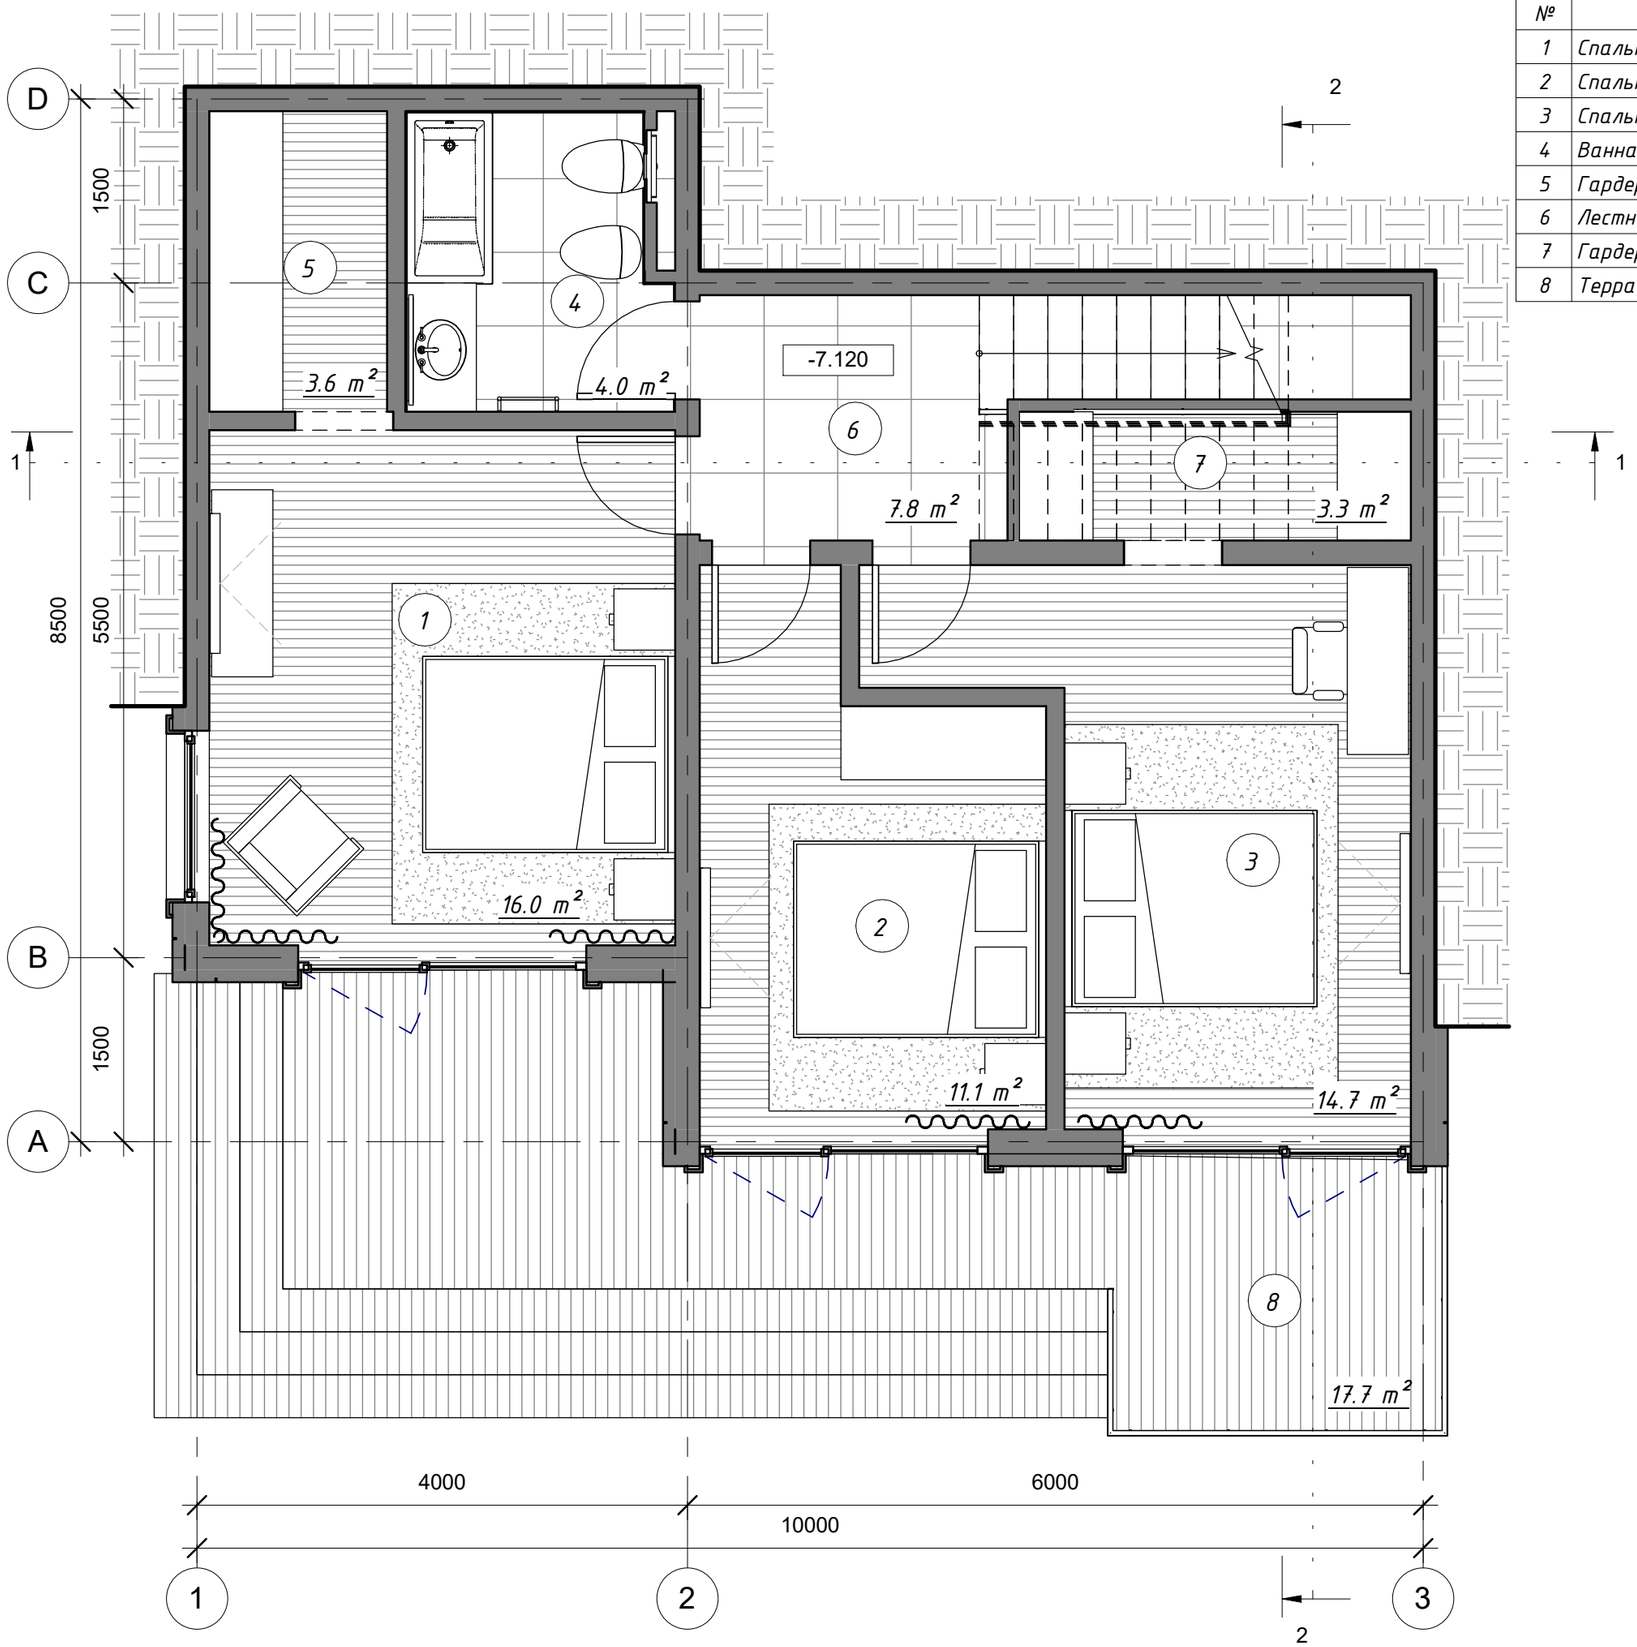

Экспликация помещений. Цокольный этаж 2

№	Наименование	Площадь
1	Спальня	16.0 m²
2	Спальня	11.1 m²
3	Спальня	14.7 m²
4	Ванная комната	4.0 m²
5	Гардероб	3.6 m²
6	Лестница	7.8 m²
7	Гардероб	3.3 m²
8	Терраса	17.7 m²
		78.1 m²

L.B.O.S.
DESIGN

№	Описание	Дата

Batumi Investment
SeaView Garden Villa. №1

Стадия (Stage): Эскиз (Concept)

Цокольный этаж 2. План

Номер проекта	0001
Дата	01.04.2021
Чертил	Сидорук О.
Проверил	

A101

Масштаб	1 : 50

5/10/2021 9:45:41 AM

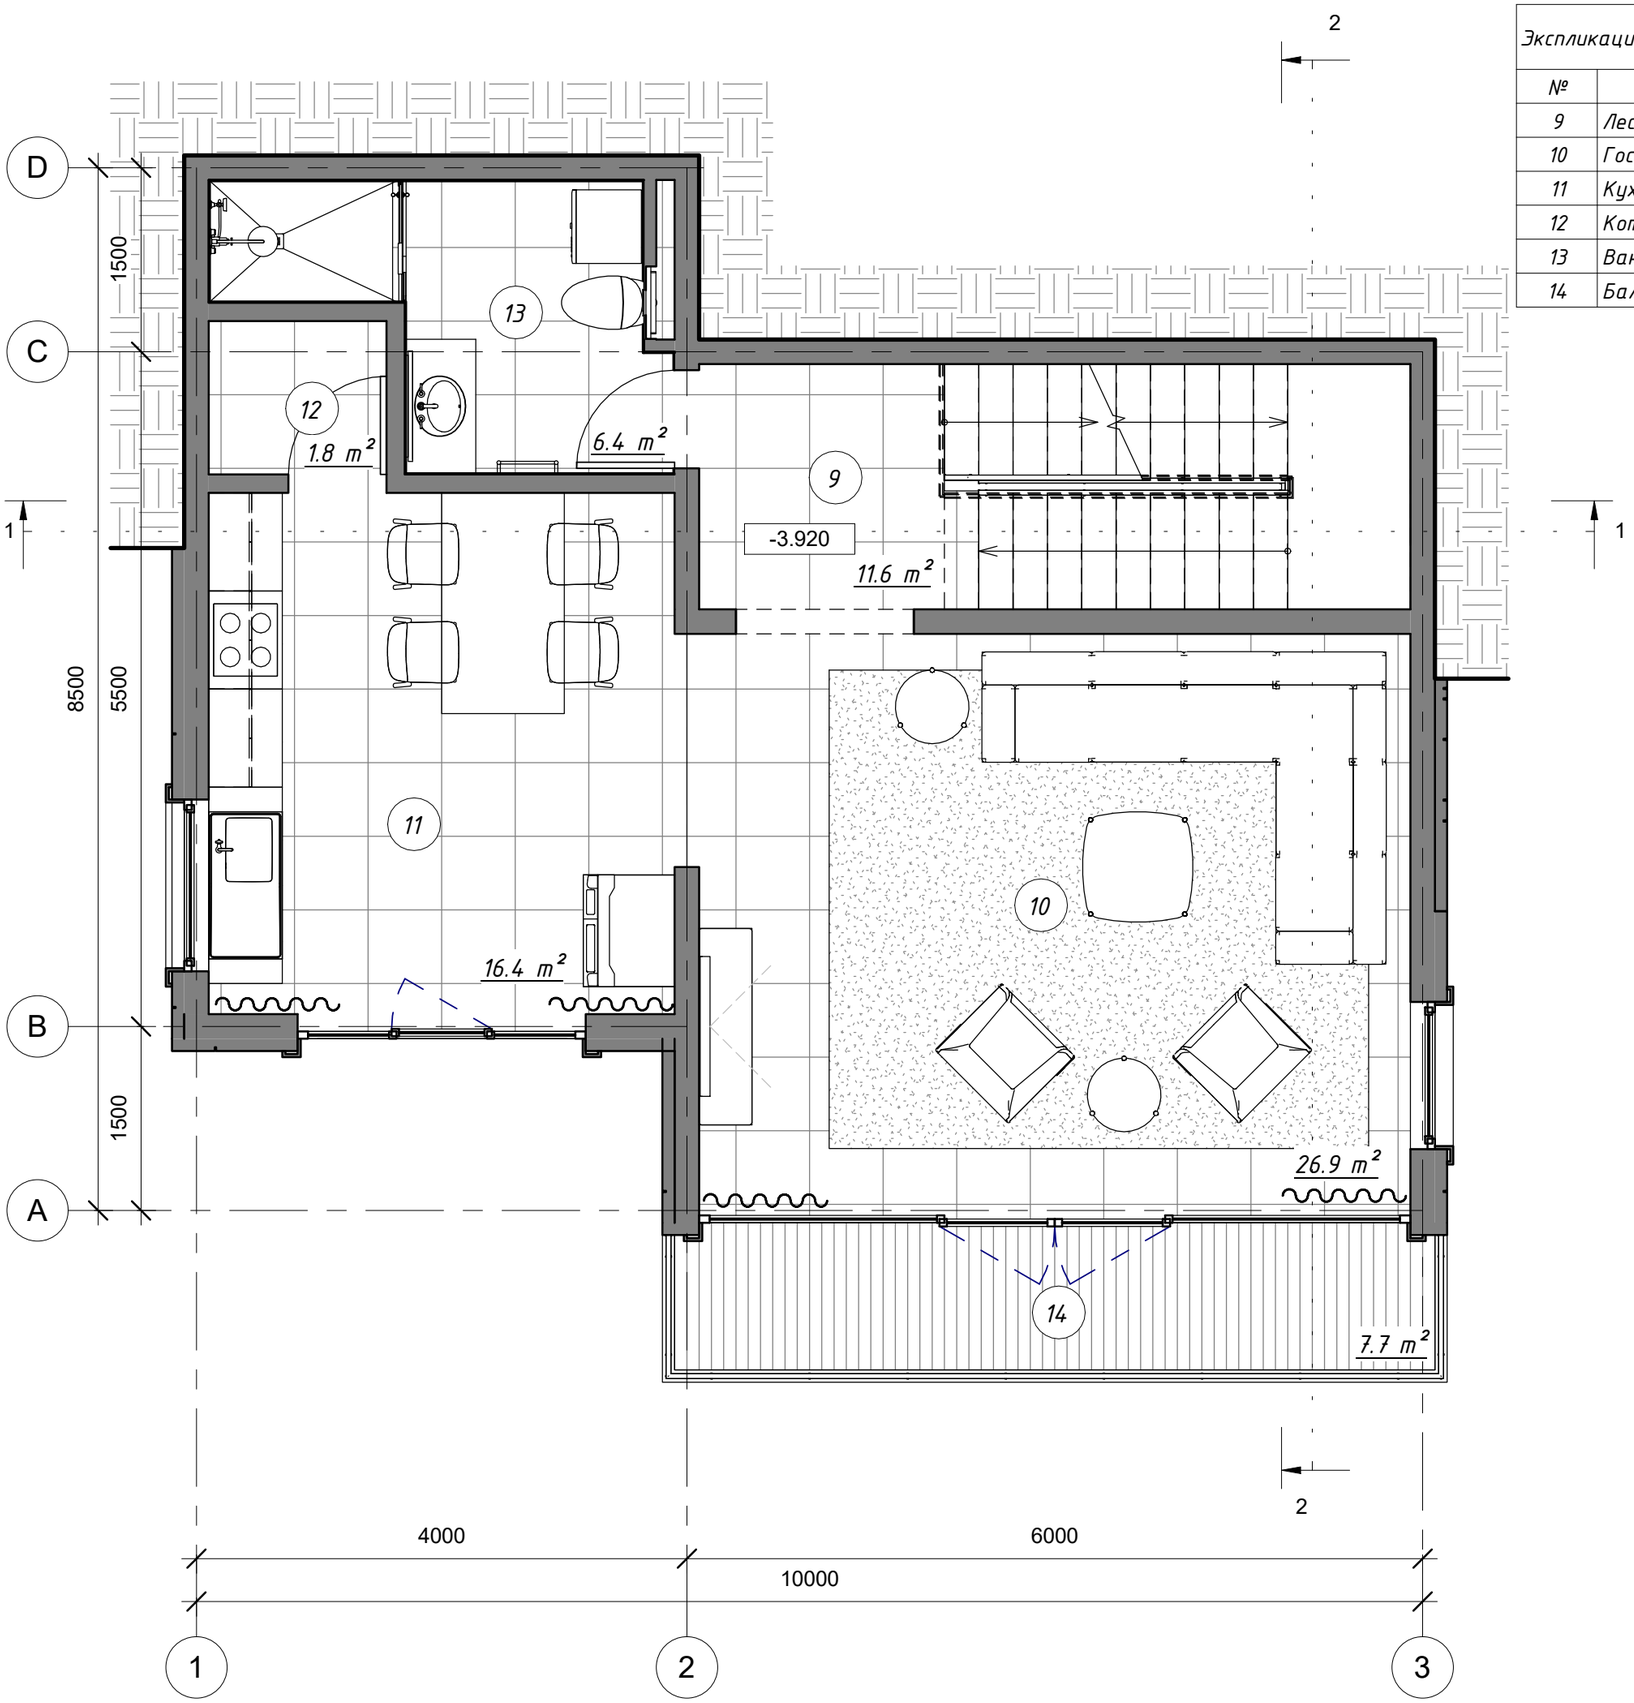

Экспликация помещений. Цокольный этаж 1

№	Наименование	Площадь
9	Лестница	11.6 m²
10	Гостиная	26.9 m²
11	Кухня-столовая	16.4 m²
12	Котельня	1.8 m²
13	Ванная комната	6.4 m²
14	Балкон	7.7 m²
		70.7 m²

L.B.O.S.
DESIGN

№	Описание	Дата

Batumi Investment
SeaView Garden Villa. №1

Стадия (Stage): Эскиз (Concept)

Цокольный этаж 1. План

Номер проекта	0001
Дата	01.04.2021
Чертил	Сидорук О.
Проверил	

A102

Масштаб 1 : 50

5/10/2021 9:45:45 AM

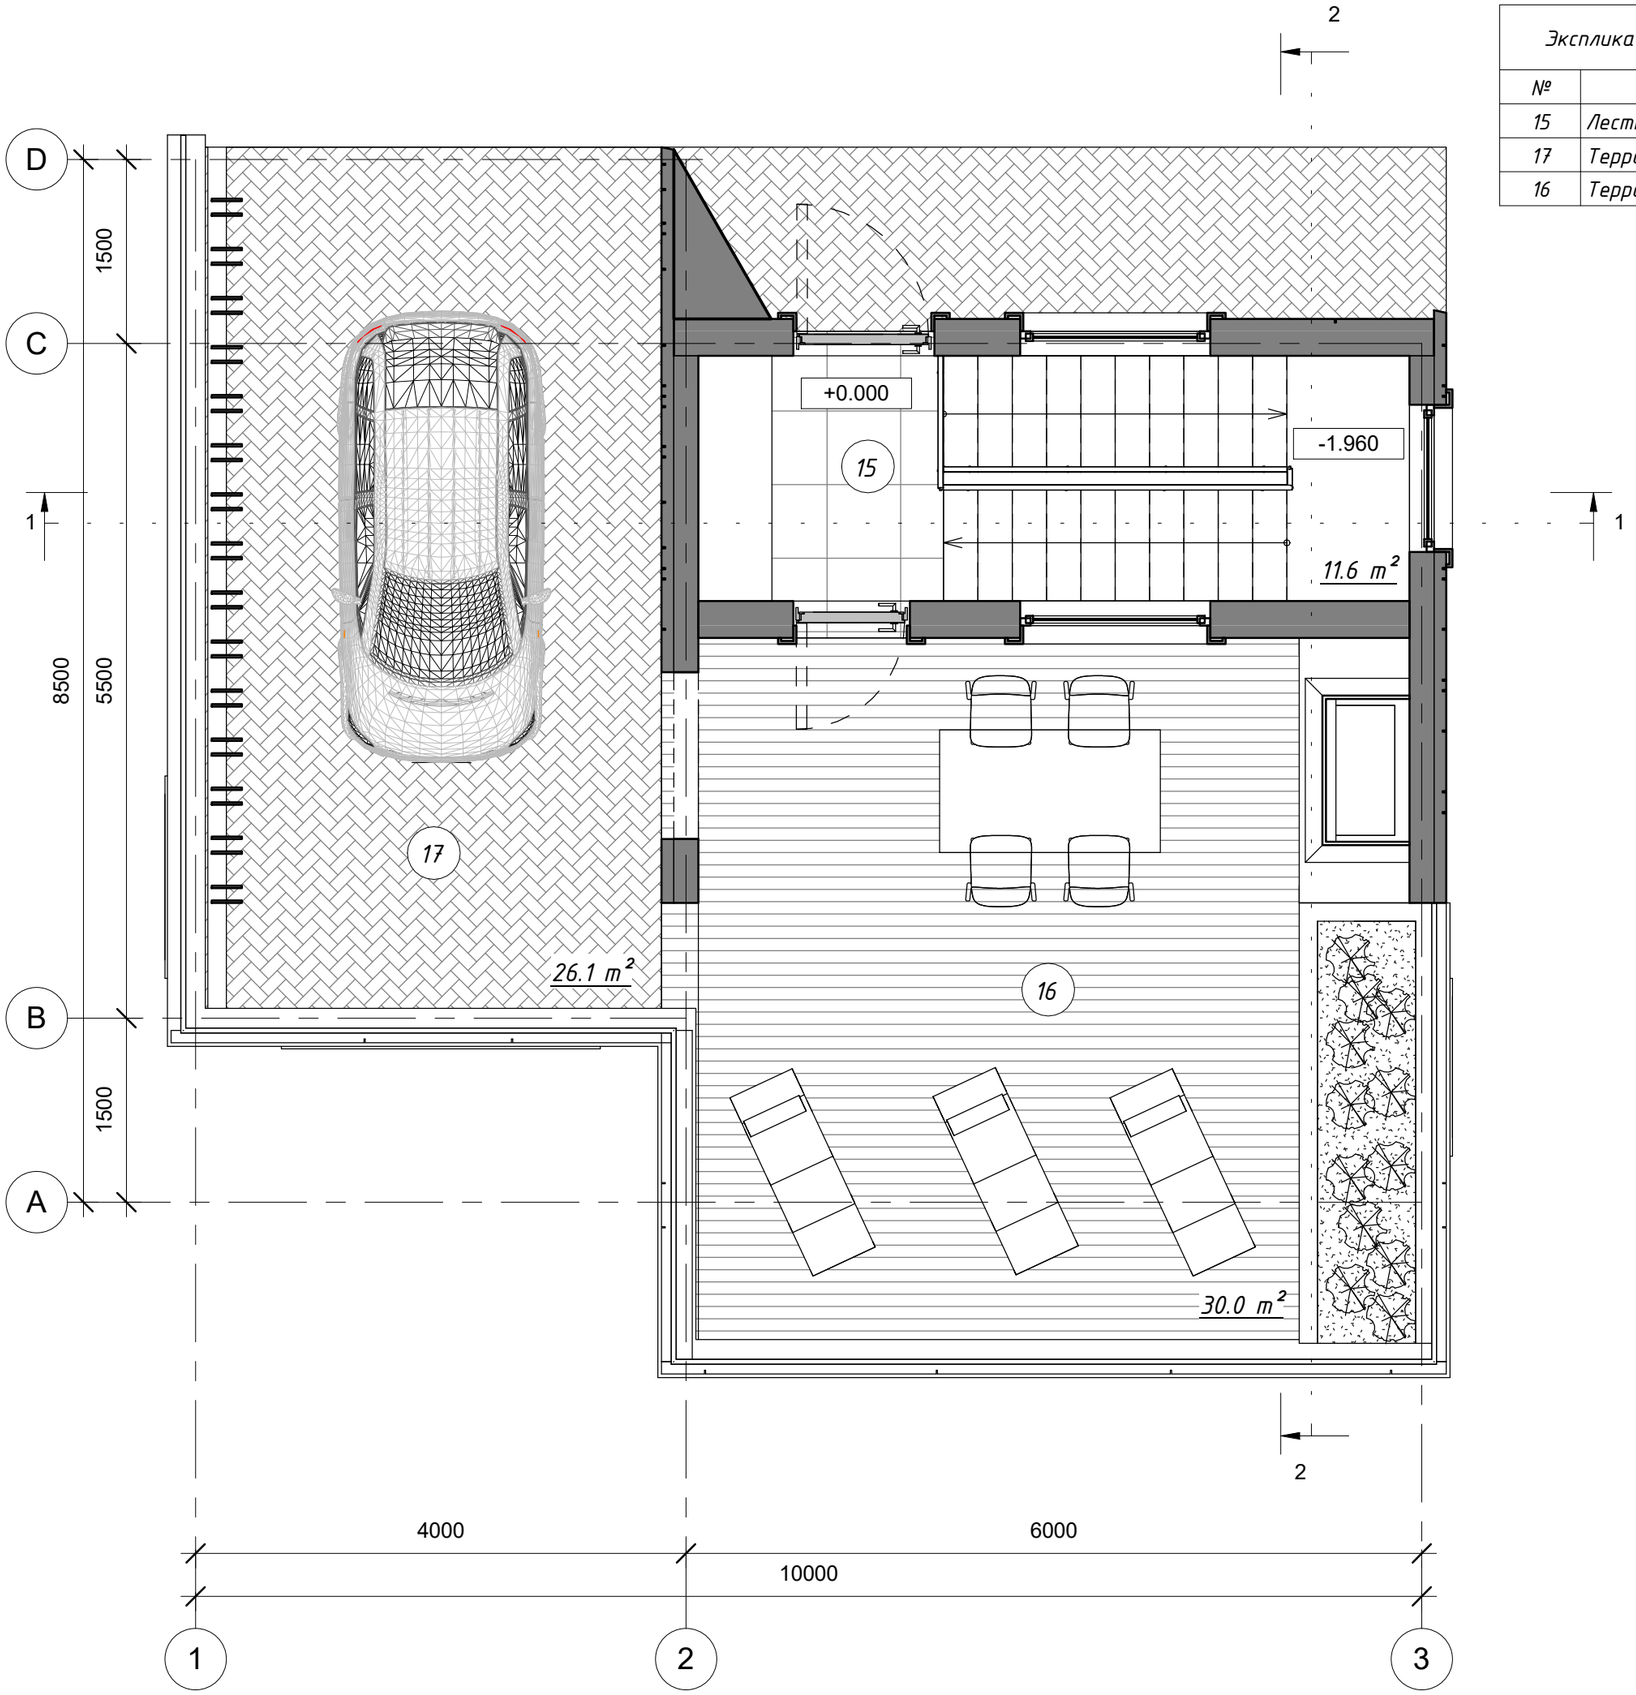

Экспликация помещений. 1-го этажа		
№	Наименование	Площадь
15	Лестница	11.6 m²
17	Терраса	26.1 m²
16	Терраса	30.0 m²
		67.7 m²

L.B.O.S.
DESIGN

№	Описание	Дата

Batumi Investment
SeaView Garden Villa. №1

Стадия (Stage): Эскиз (Concept)

1-го этажа. План

Номер проекта	0001
Дата	01.04.2021
Чертил	Сидорук О.
Проверил	

A103

Масштаб 1 : 50

5/10/2021 9:45:47 AM

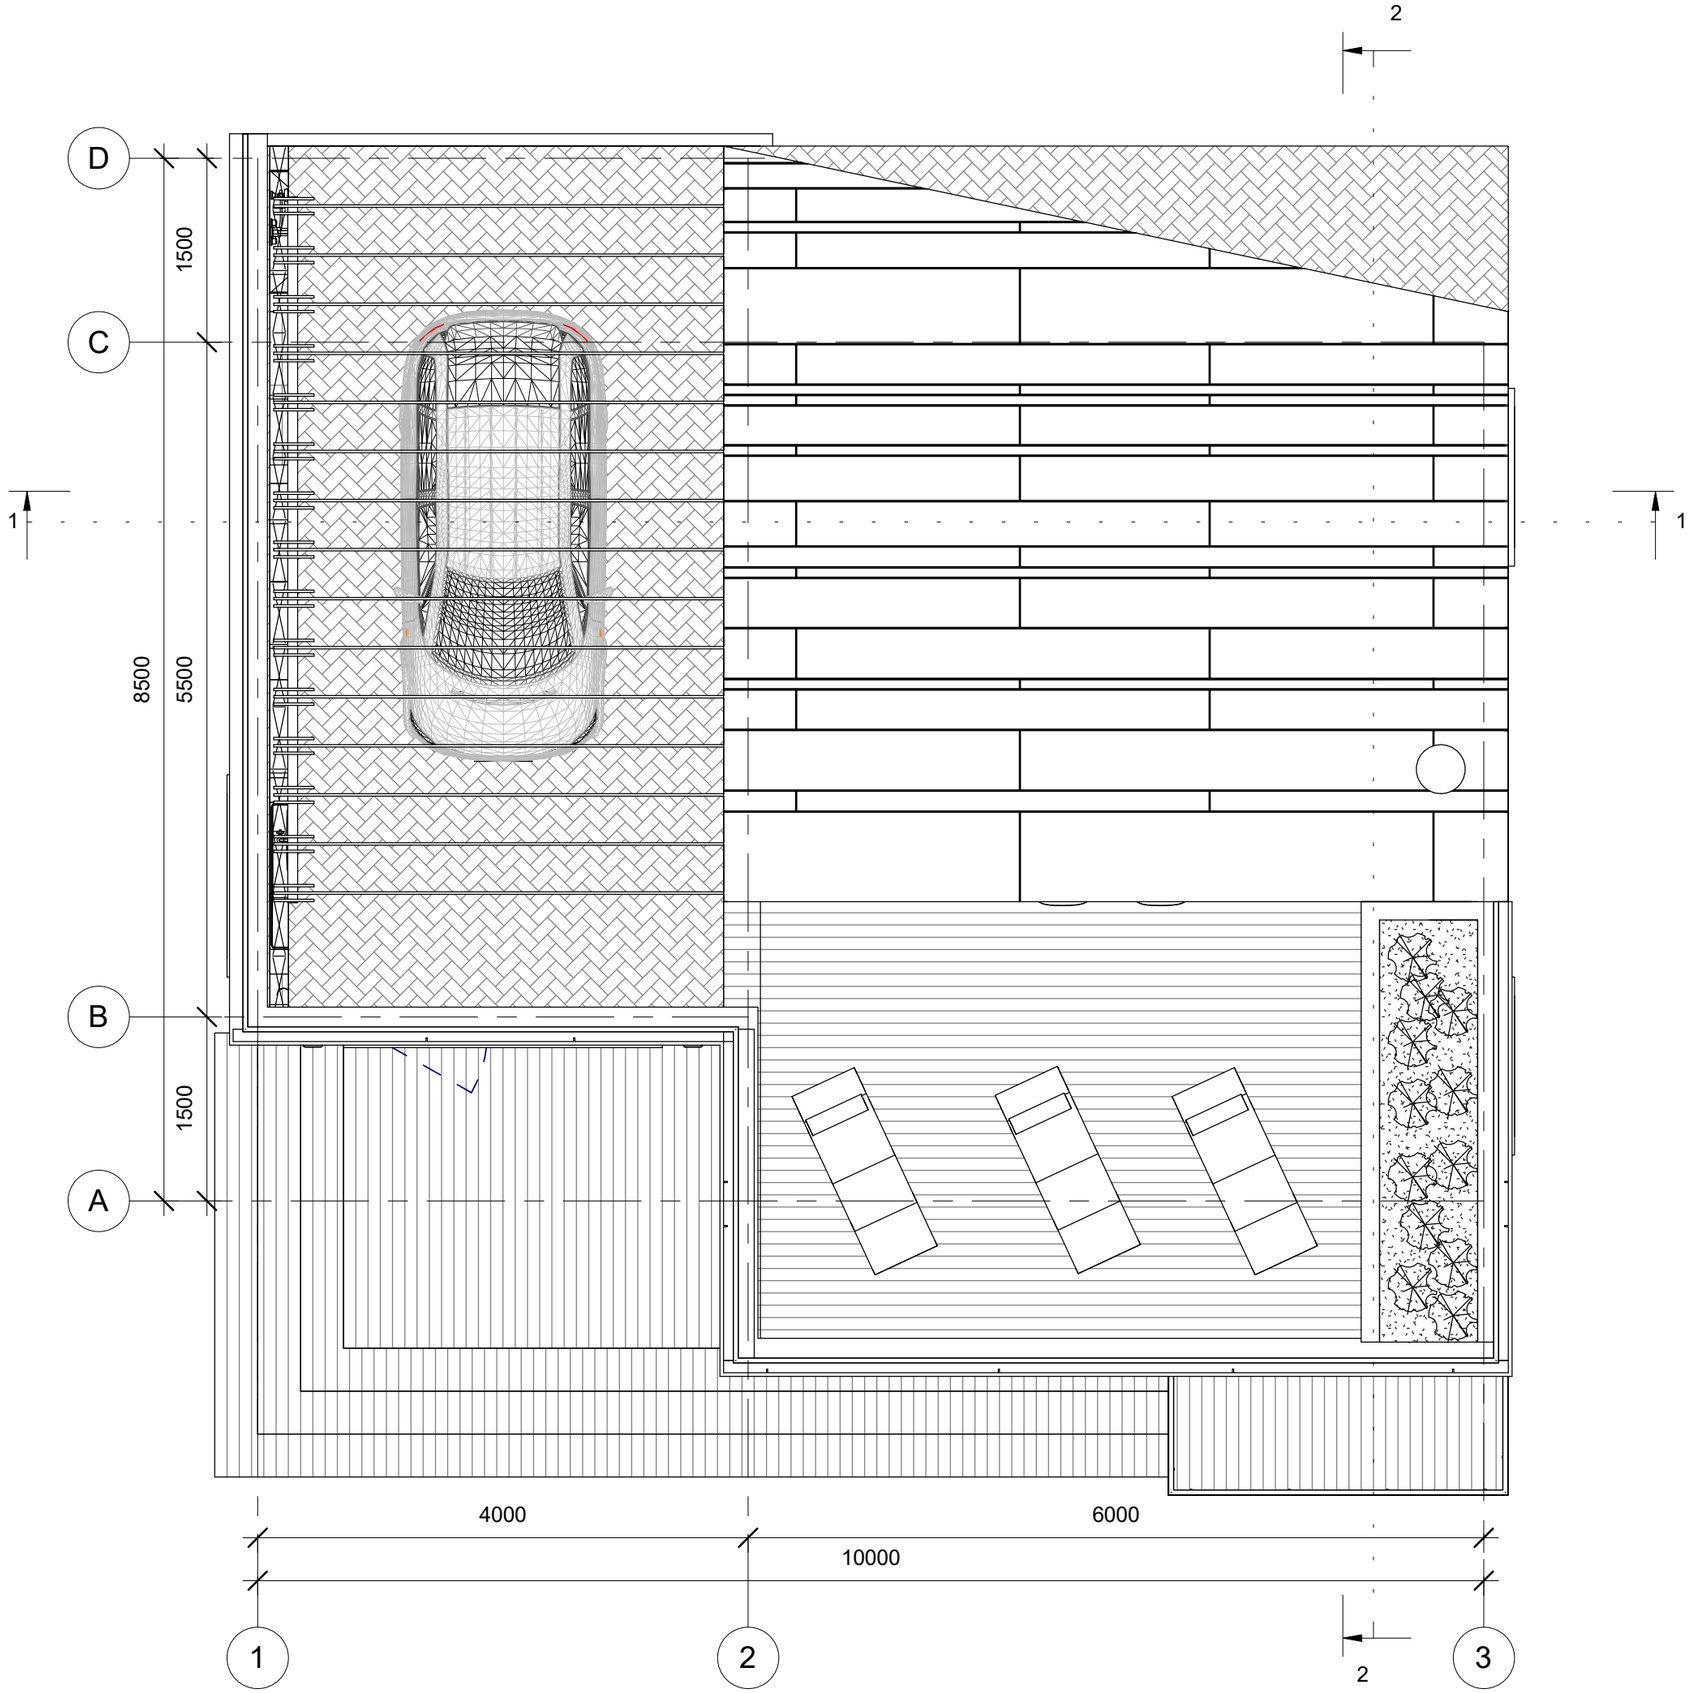

L.B.O.S.
DESIGN

№	Описание	Дата

Batumi Investment
SeaView Garden Villa. №1

Стадия (Stage): Эскиз (Concept)

План кровли

Номер проекта	0001
Дата	01.04.2021
Чертил	Сидорук О.
Проверил	

A104

Масштаб	1 : 50

5/10/2021 9:45:48 AM

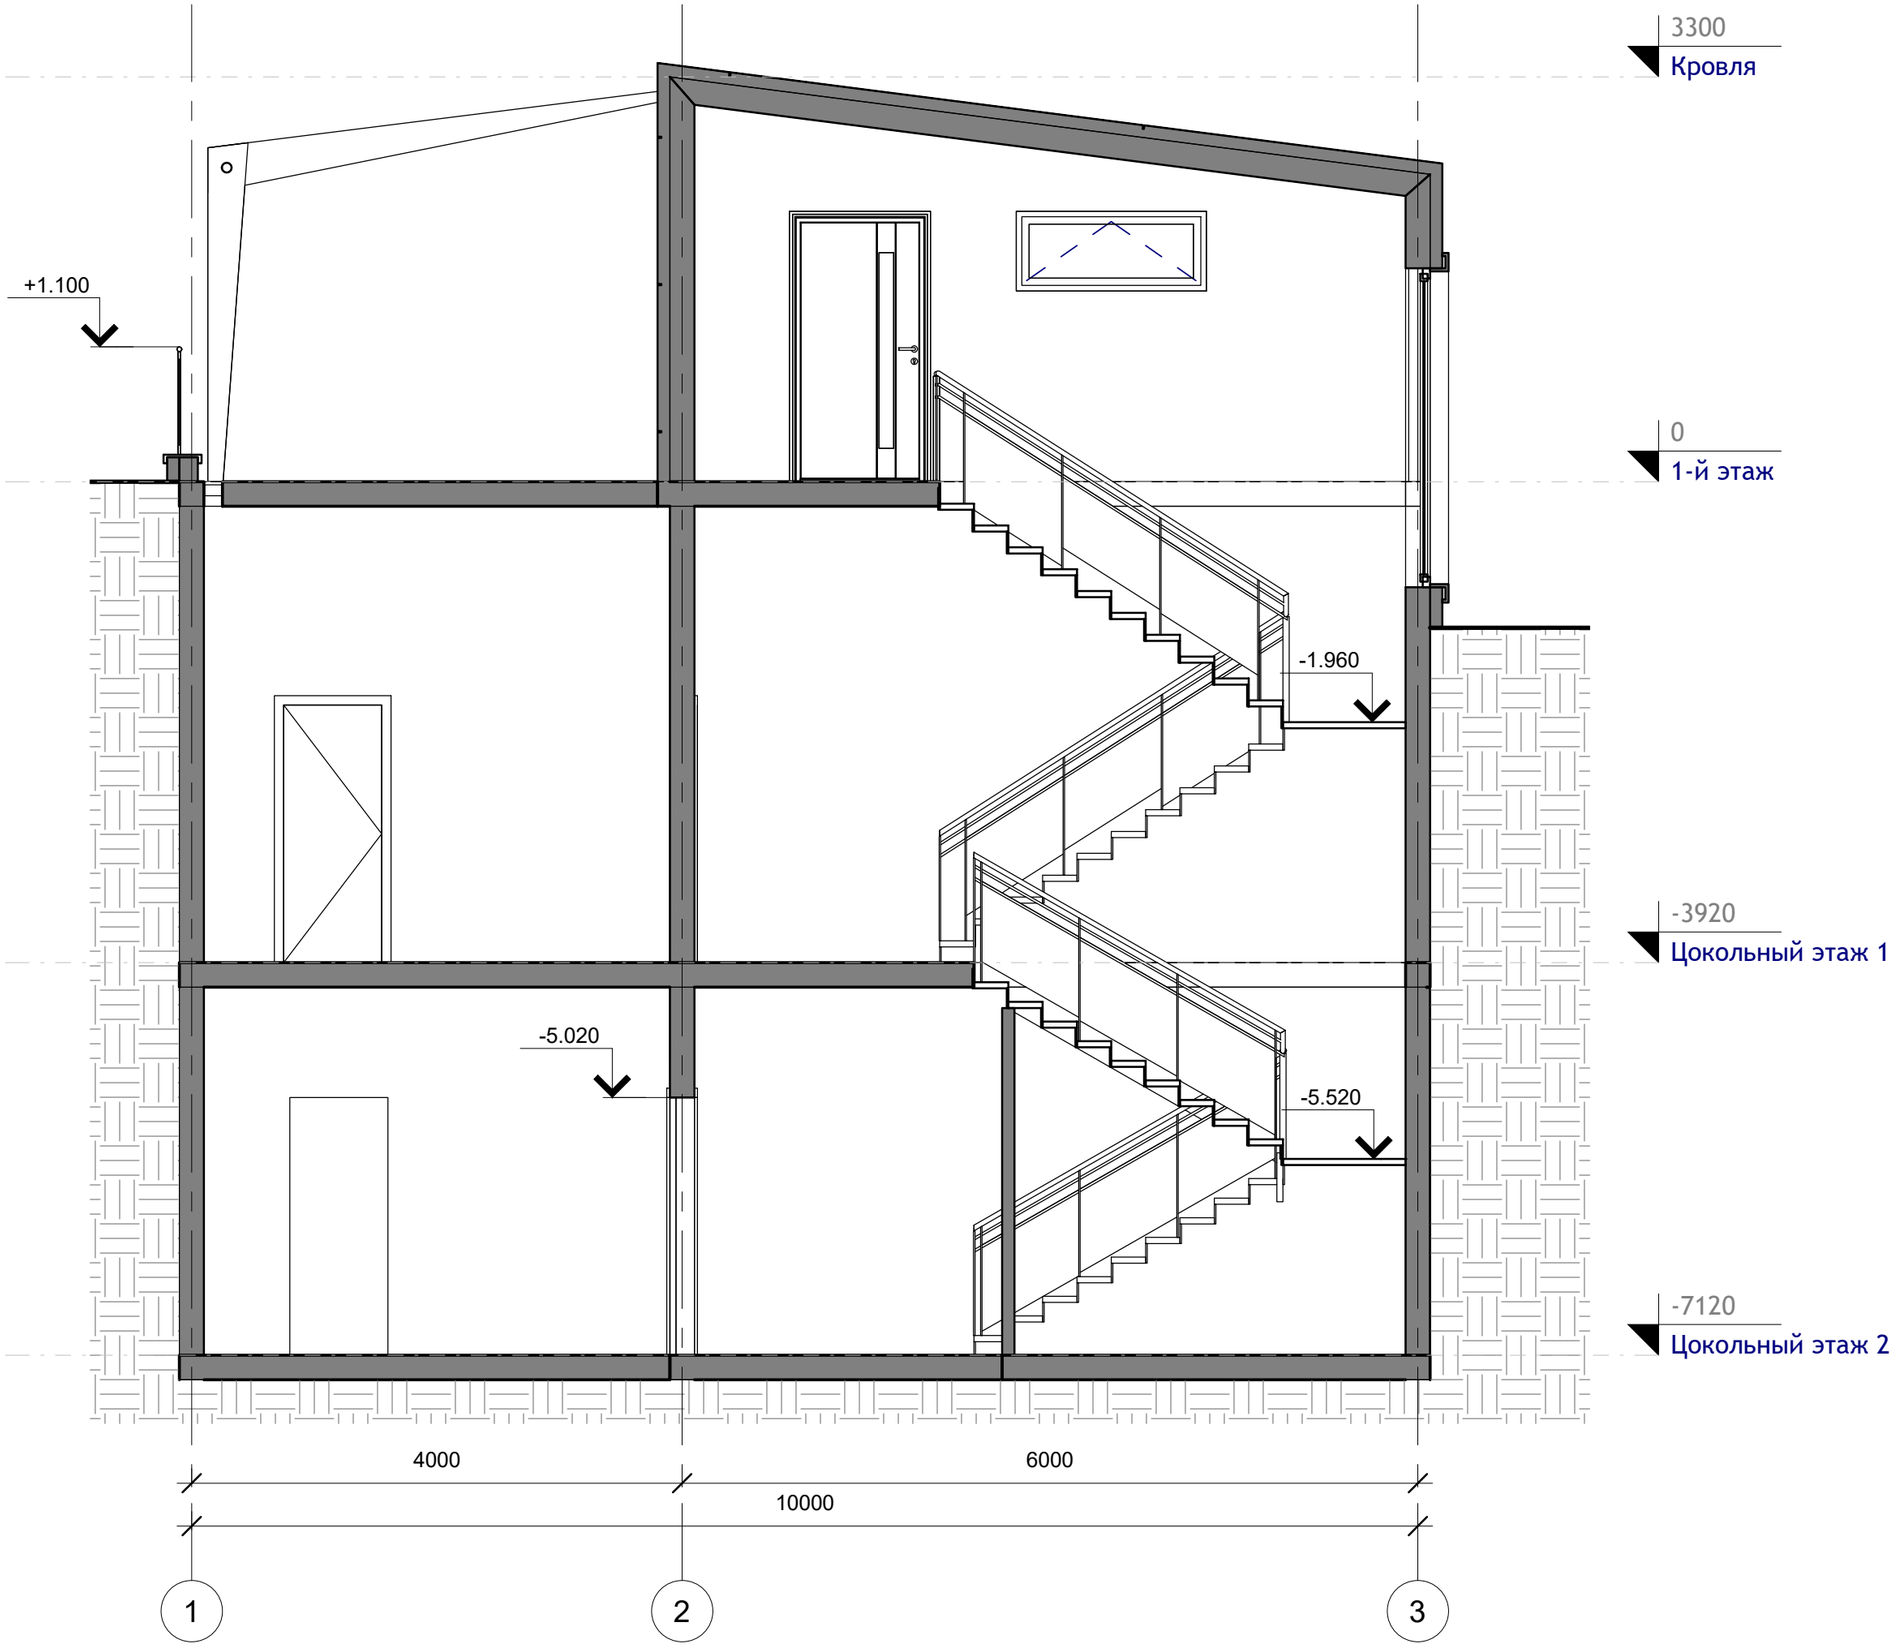

L.B.O.S.
DESIGN

№	Описание	Дата

Batumi Investment
SeaView Garden Villa. №1

Стадия (Stage): Эскиз (Concept)

Разрез 1-1

Номер проекта	0001
Дата	01.04.2021
Чертил	Сидорук О.
Проверил	

A105

Масштаб	1 : 50

5/10/2021 9:45:49 AM

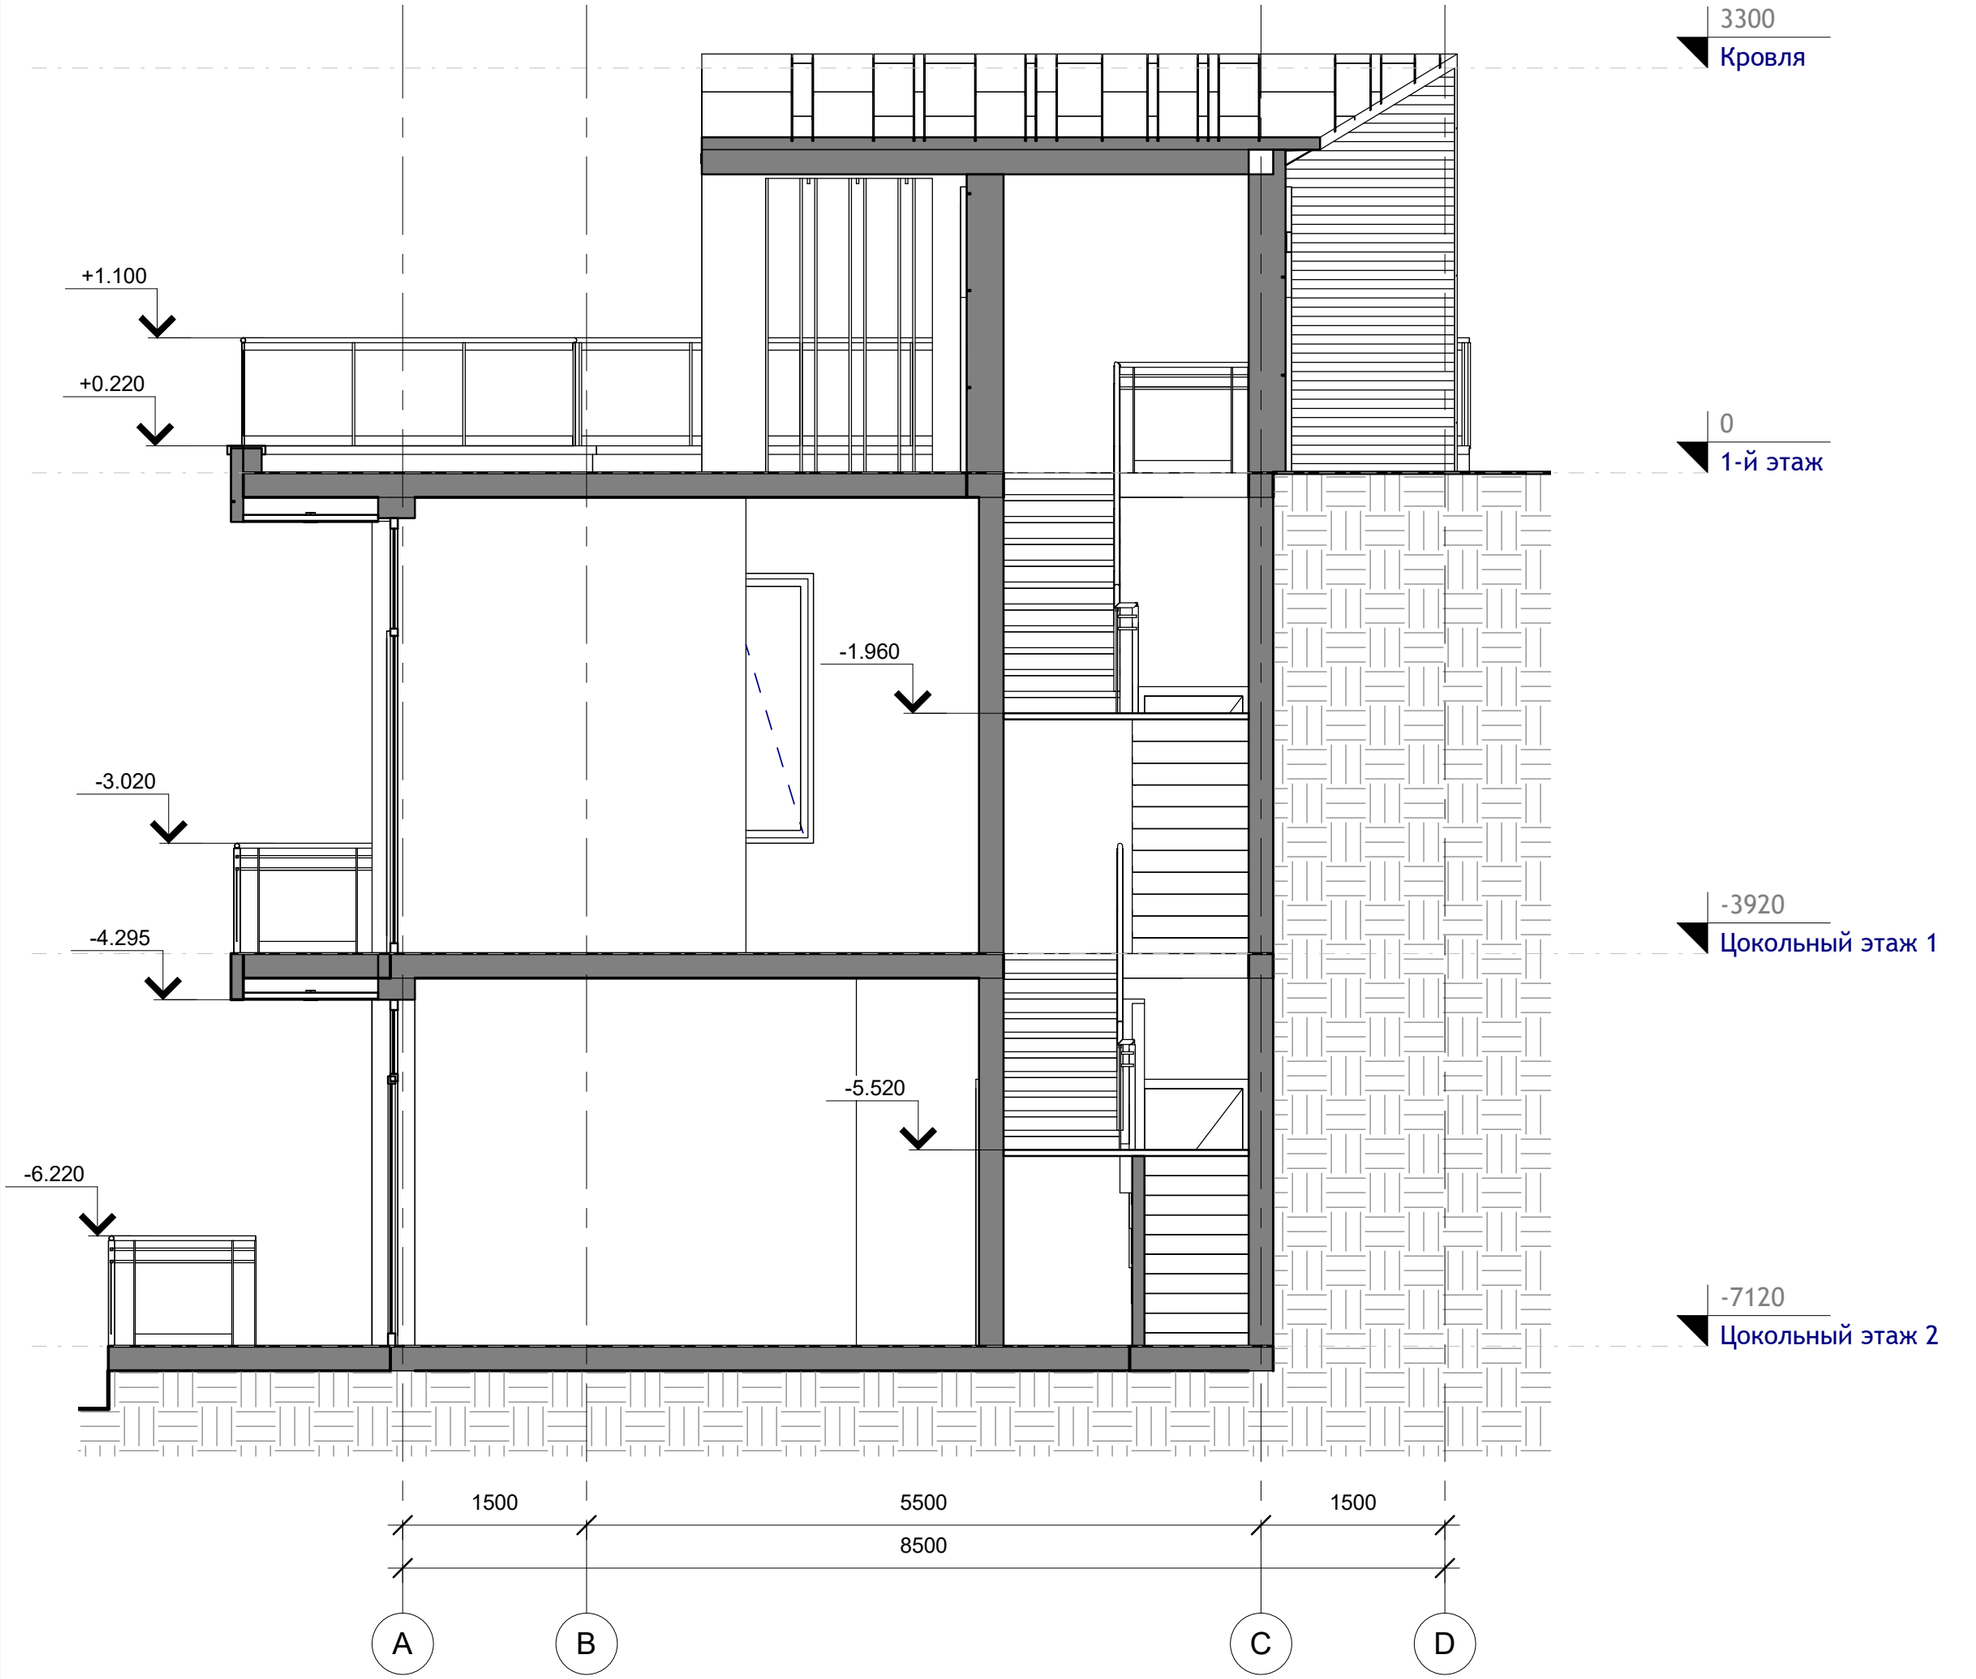

L.B.O.S.
DESIGN

№	Описание	Дата

Batumi Investment
SeaView Garden Villa. №1

Стадия (Stage): Эскиз (Concept)

Разрез 2-2

Номер проекта	0001
Дата	01.04.2021
Чертил	Сидорук О.
Проверил	

A106

Масштаб	1 : 50

5/10/2021 9:45:50 AM

L.B.O.S.
DESIGN

№	Описание	Дата

Batumi Investment
SeaView Garden Villa. №1

Стадия (Stage): Эскиз (Concept)

Фасад в осях 1-3

Номер проекта	0001
Дата	01.04.2021
Чертил	Сидорук О.
Проверил	

A107

Масштаб	1 : 50

5/10/2021 9:45:51 AM

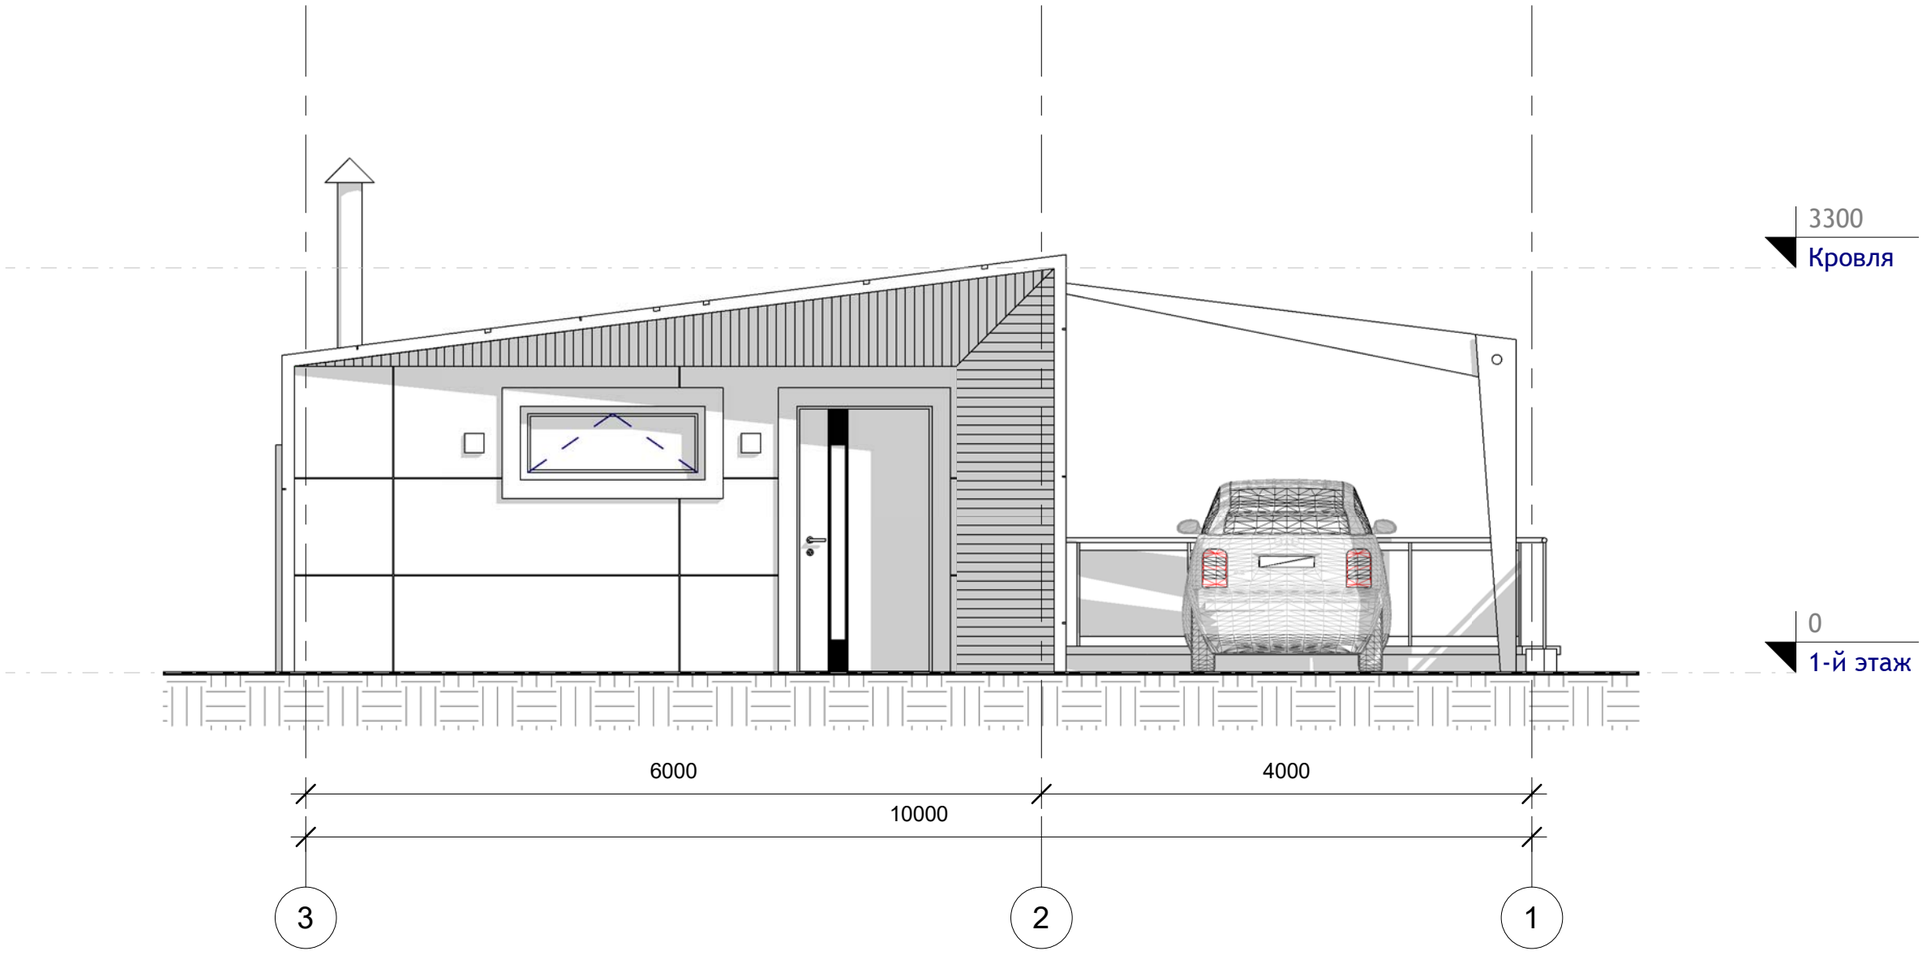

L.B.O.S.
DESIGN

№	Описание	Дата

Batumi Investment
SeaView Garden Villa. №1

Стадия (Stage): Эскиз (Concept)

Фасад в осях 3-1

Номер проекта	0001
Дата	01.04.2021
Чертил	Сидорук О.
Проверил	

A108

Масштаб	1 : 50

5/10/2021 9:45:52 AM

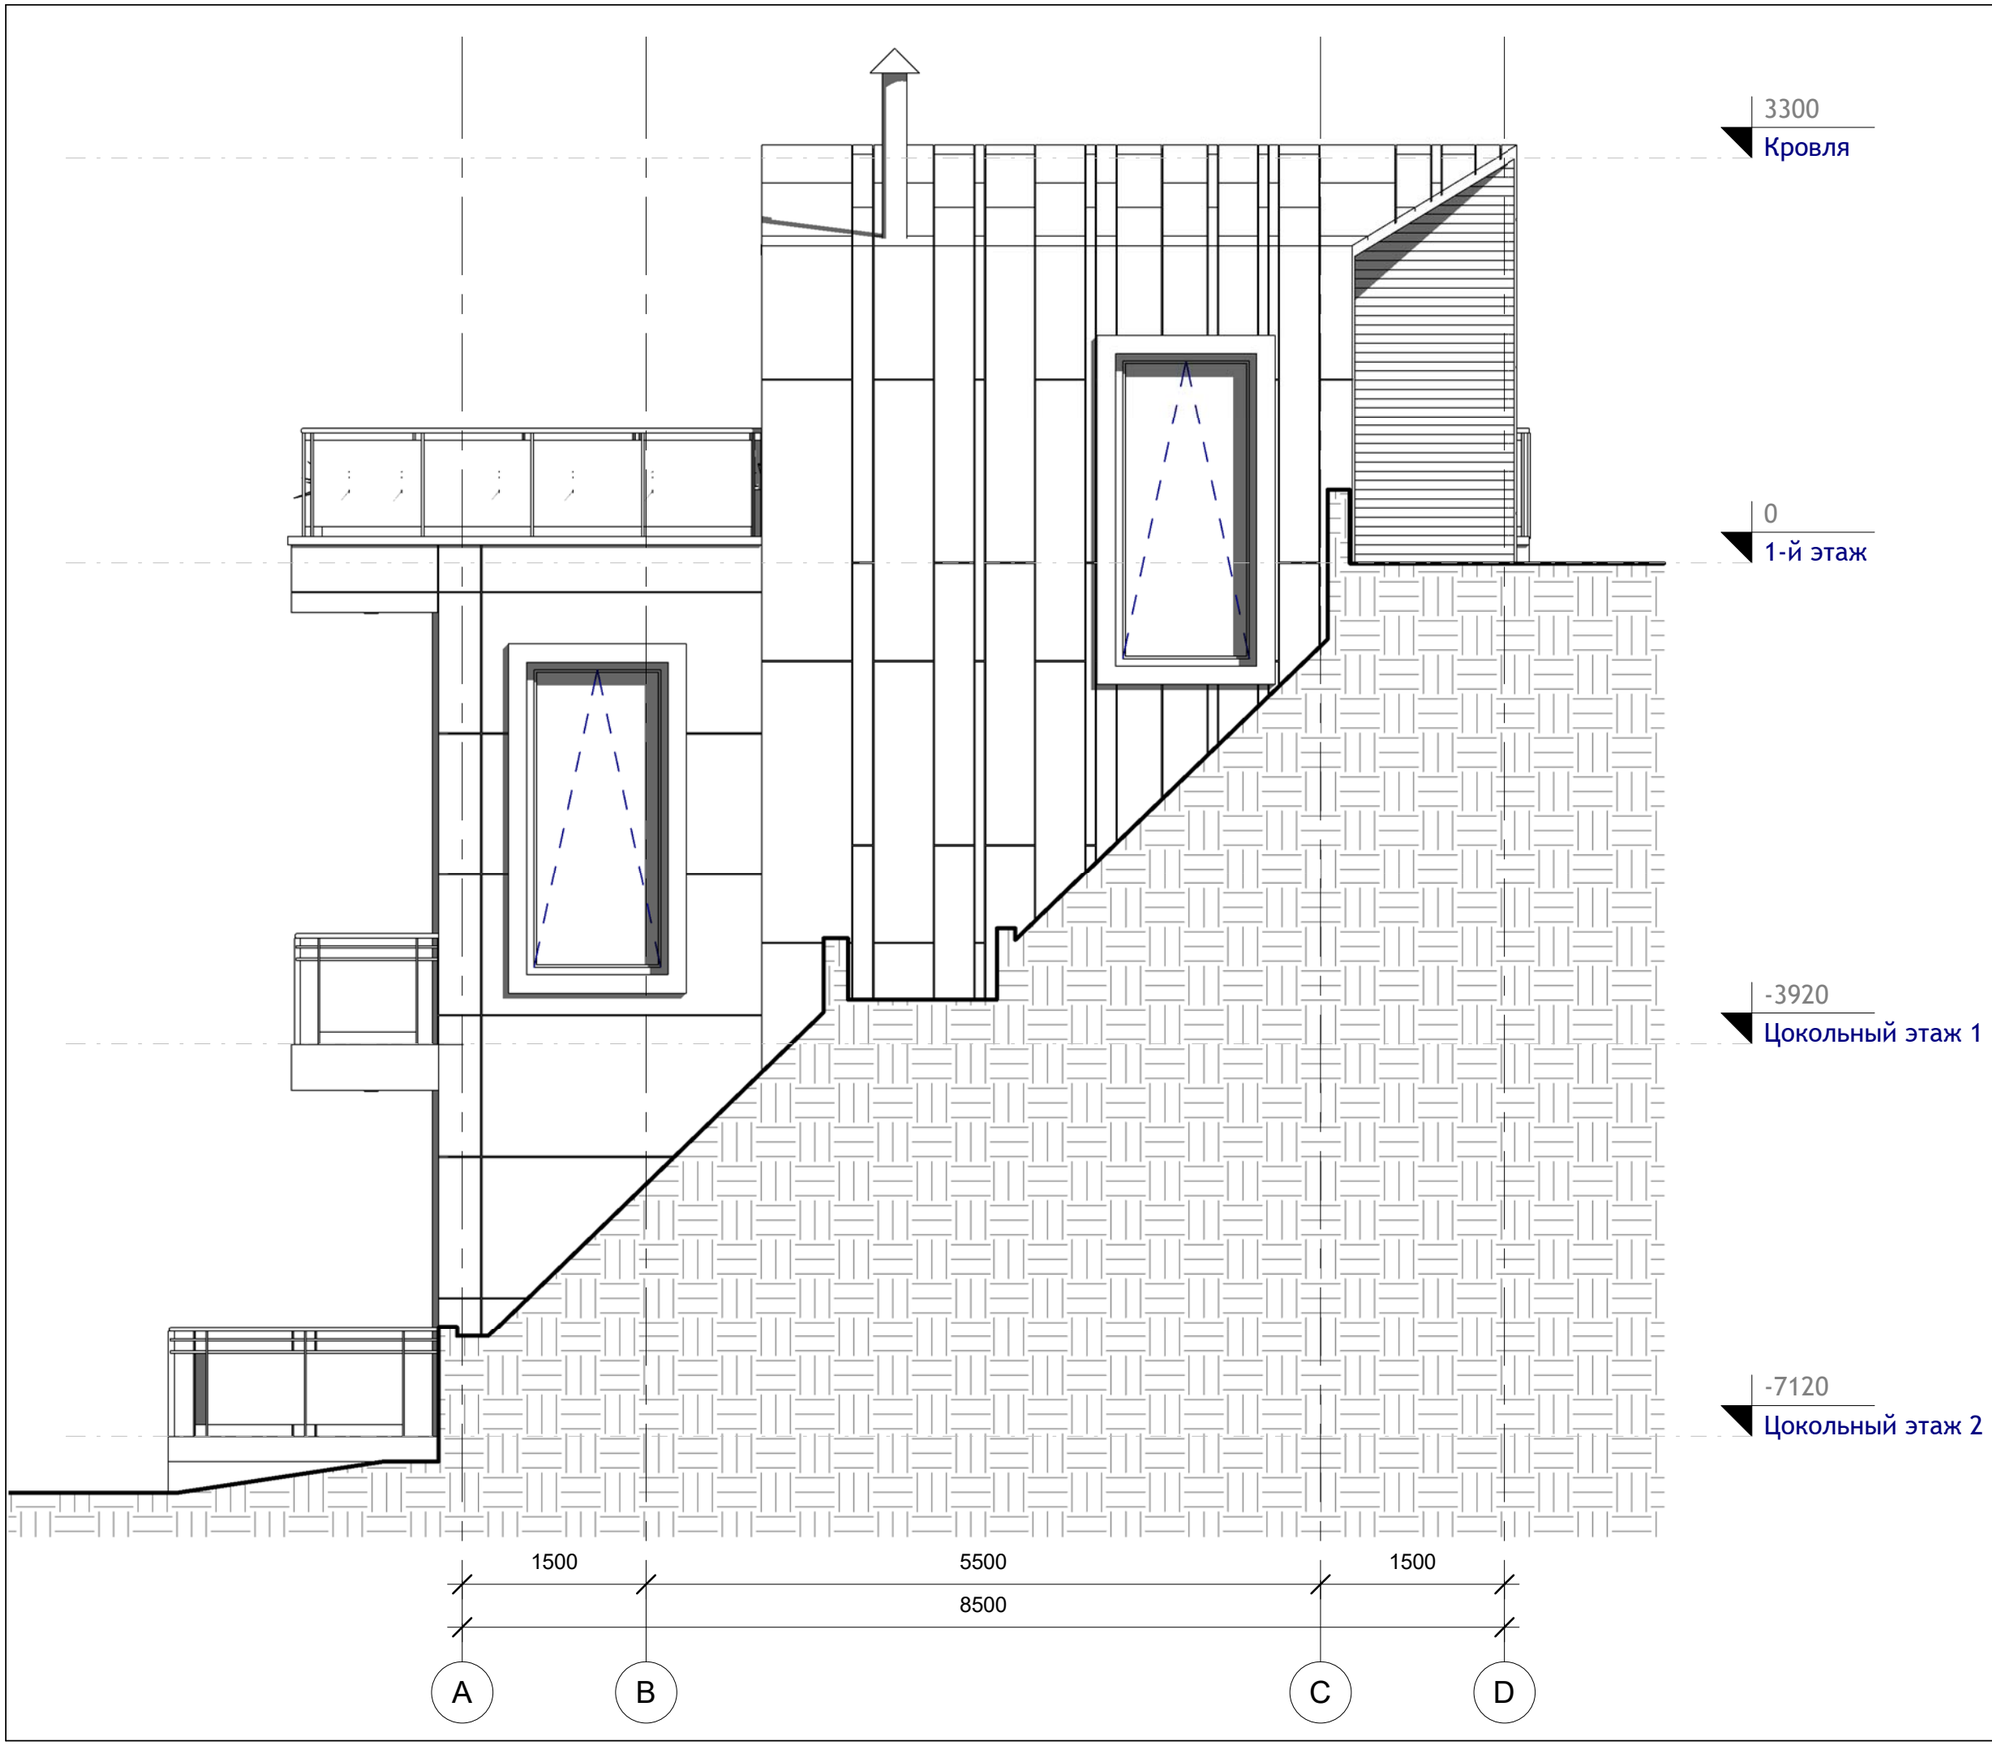

L.B.O.S.
DESIGN

№	Описание	Дата

Batumi Investment
SeaView Garden Villa. №1

Стадия (Stage): Эскиз (Concept)

Фасад в осях A-D

Номер проекта	0001
Дата	01.04.2021
Чертил	Сидорук О.
Проверил	

A109

Масштаб	1 : 50

5/10/2021 9:45:54 AM

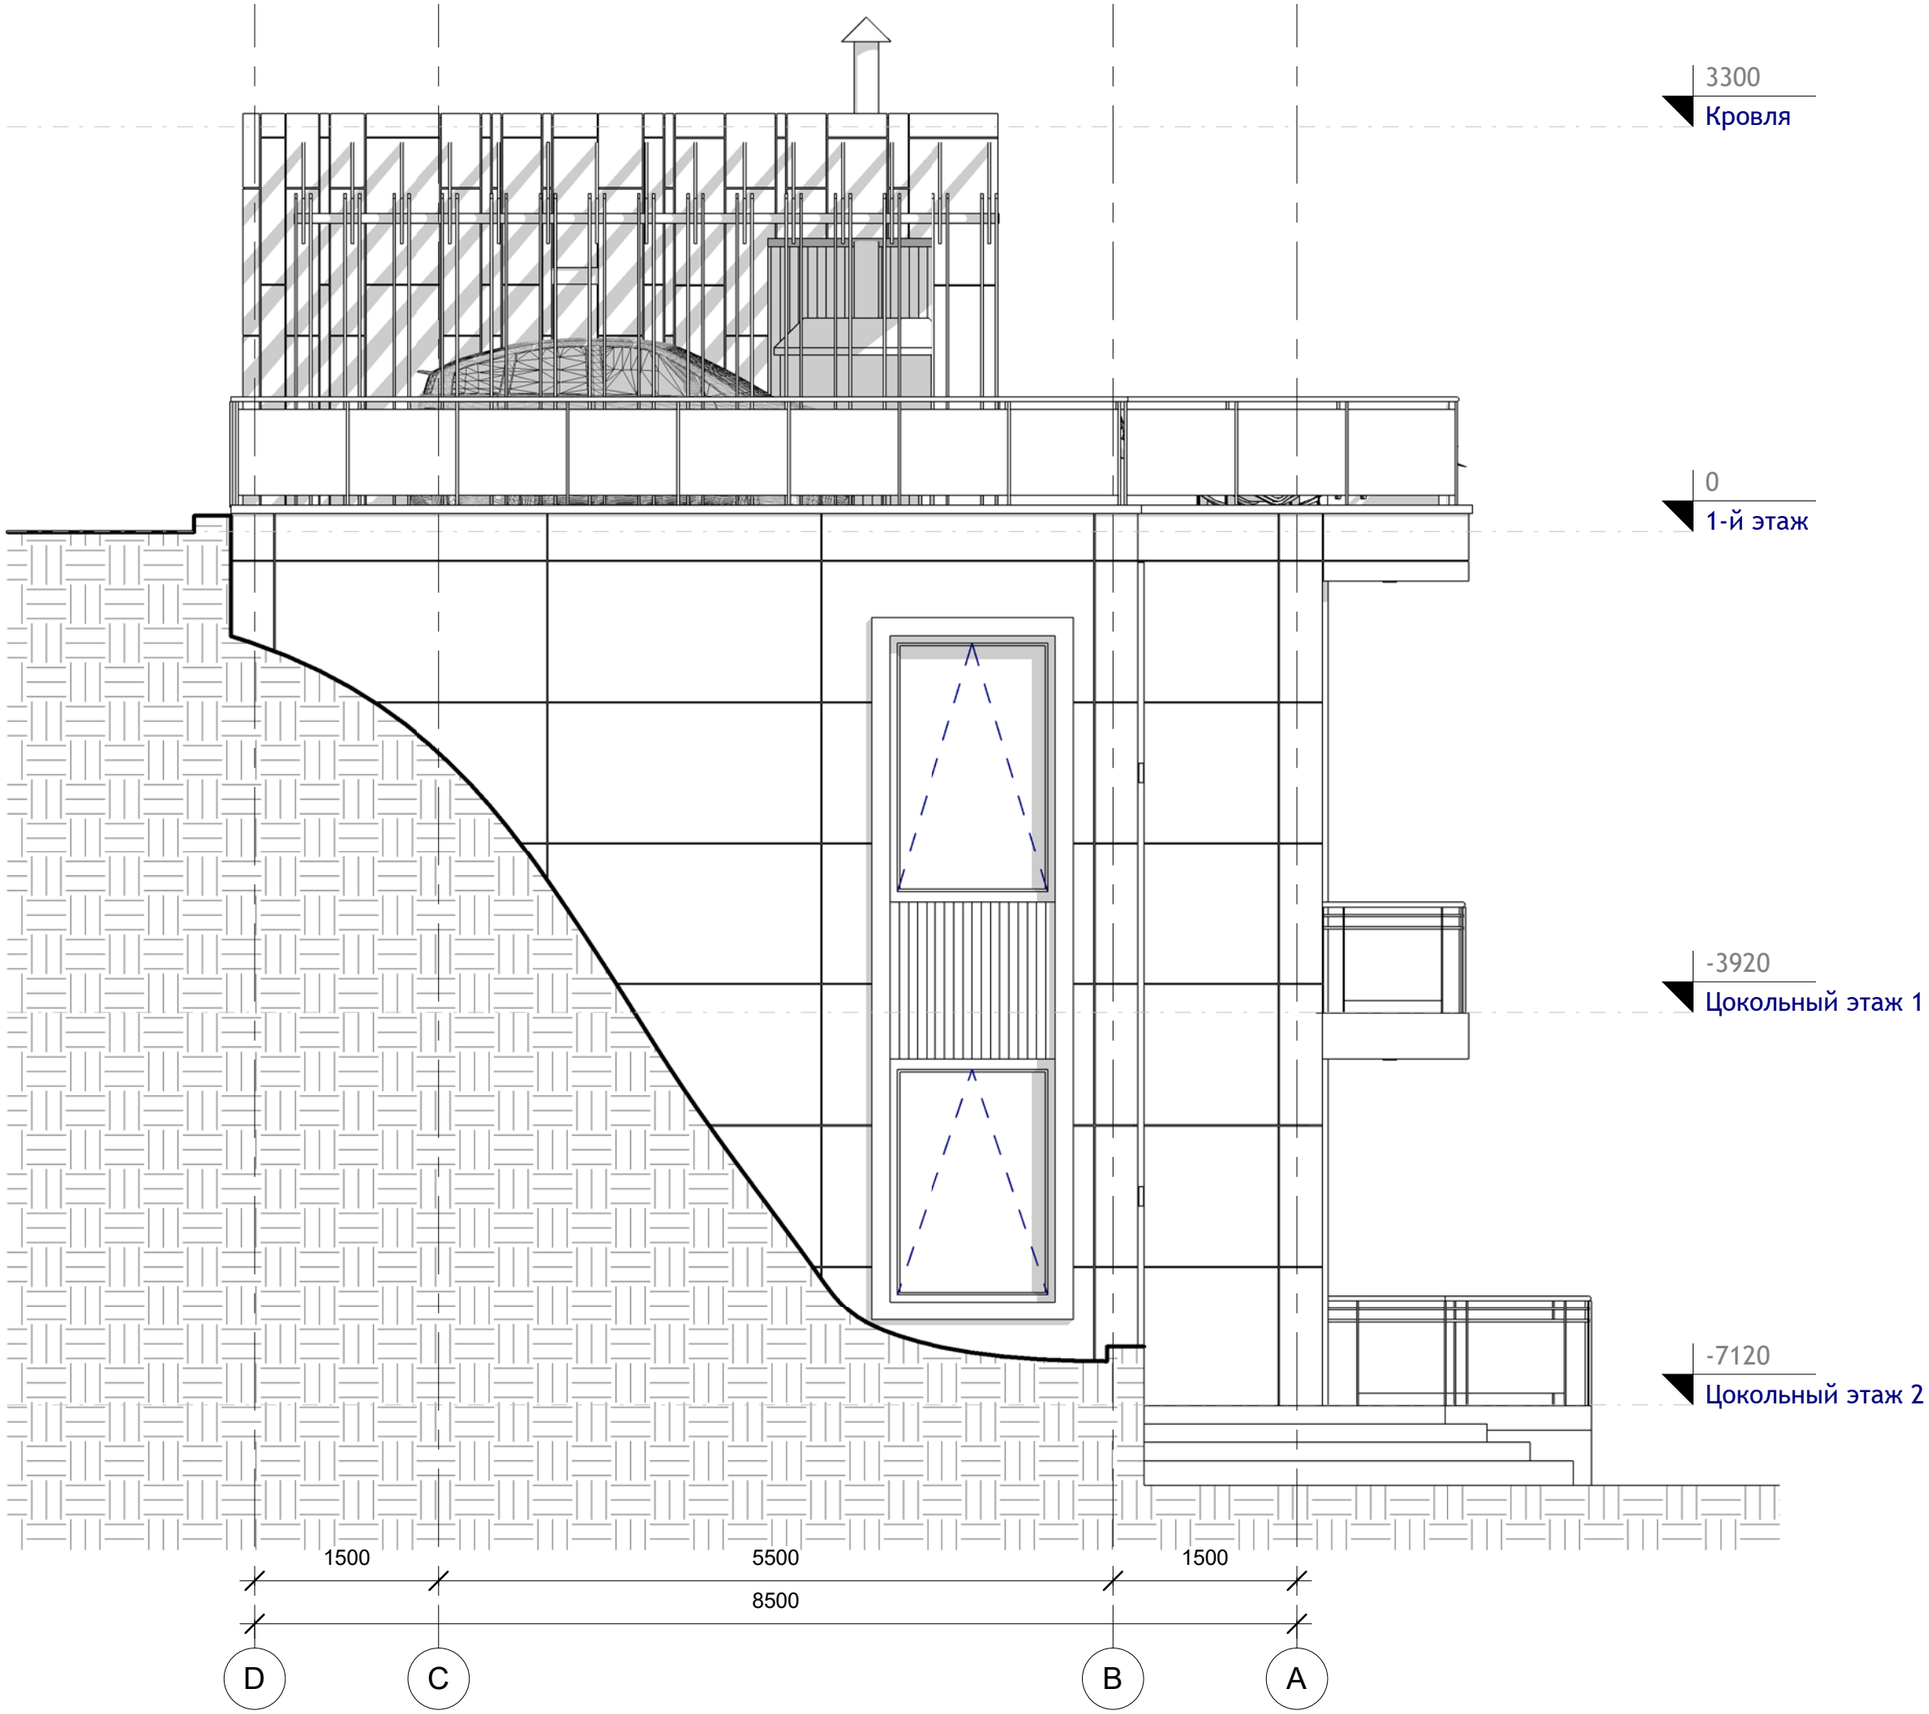

L.B.O.S.
DESIGN

№	Описание	Дата

Batumi Investment
SeaView Garden Villa. №1

Стадия (Stage): Эскиз (Concept)

Фасад в осях D-A

Номер проекта	0001
Дата	01.04.2021
Чертил	Сидорук О.
Проверил	

A110

Масштаб	1 : 50

5/10/2021 9:45:56 AM

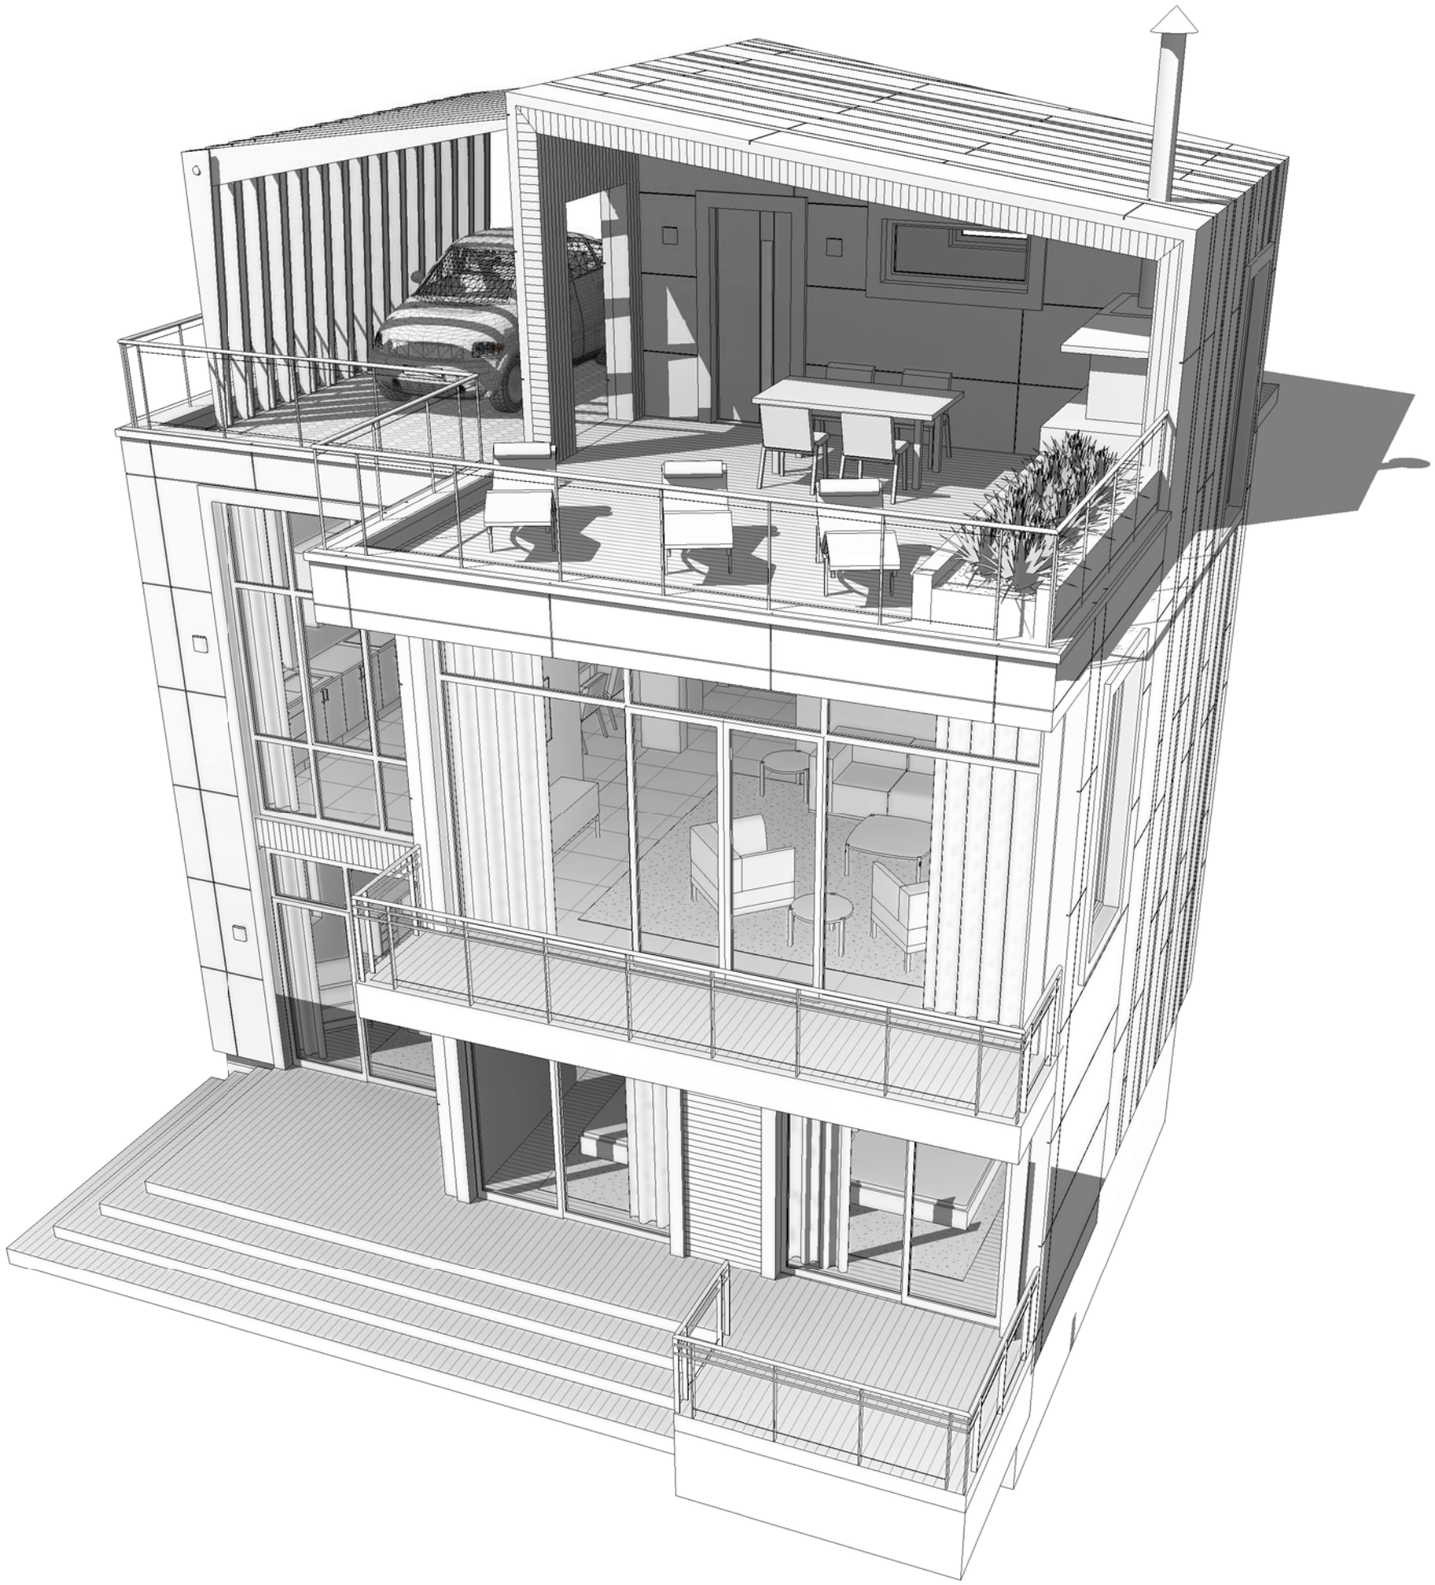

L.B.O.S.
DESIGN

№	Описание	Дата

Batumi Investment
SeaView Garden Villa. №1

Стадия (Stage): Эскиз (Concept)

Перспектива

Номер проекта	0001
Дата	01.04.2021
Чертил	Сидорук О.
Проверил	

A112

Масштаб

5/10/2021 9:45:58 AM