SeaView Garden Villas

Type 2 (280.0 m²)

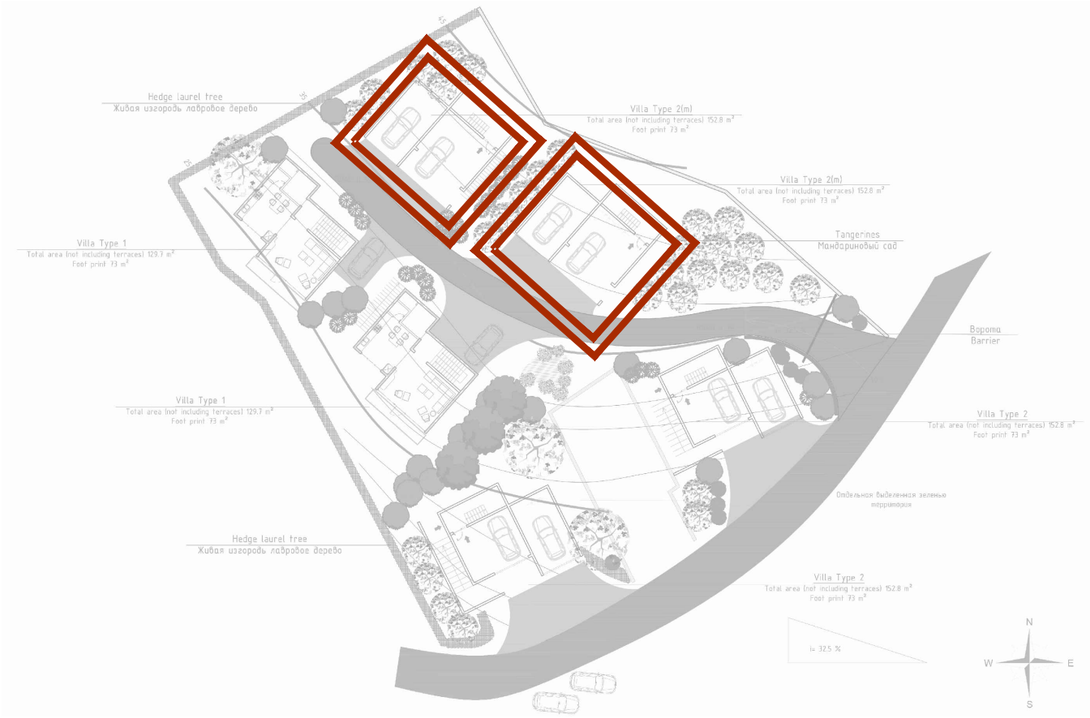

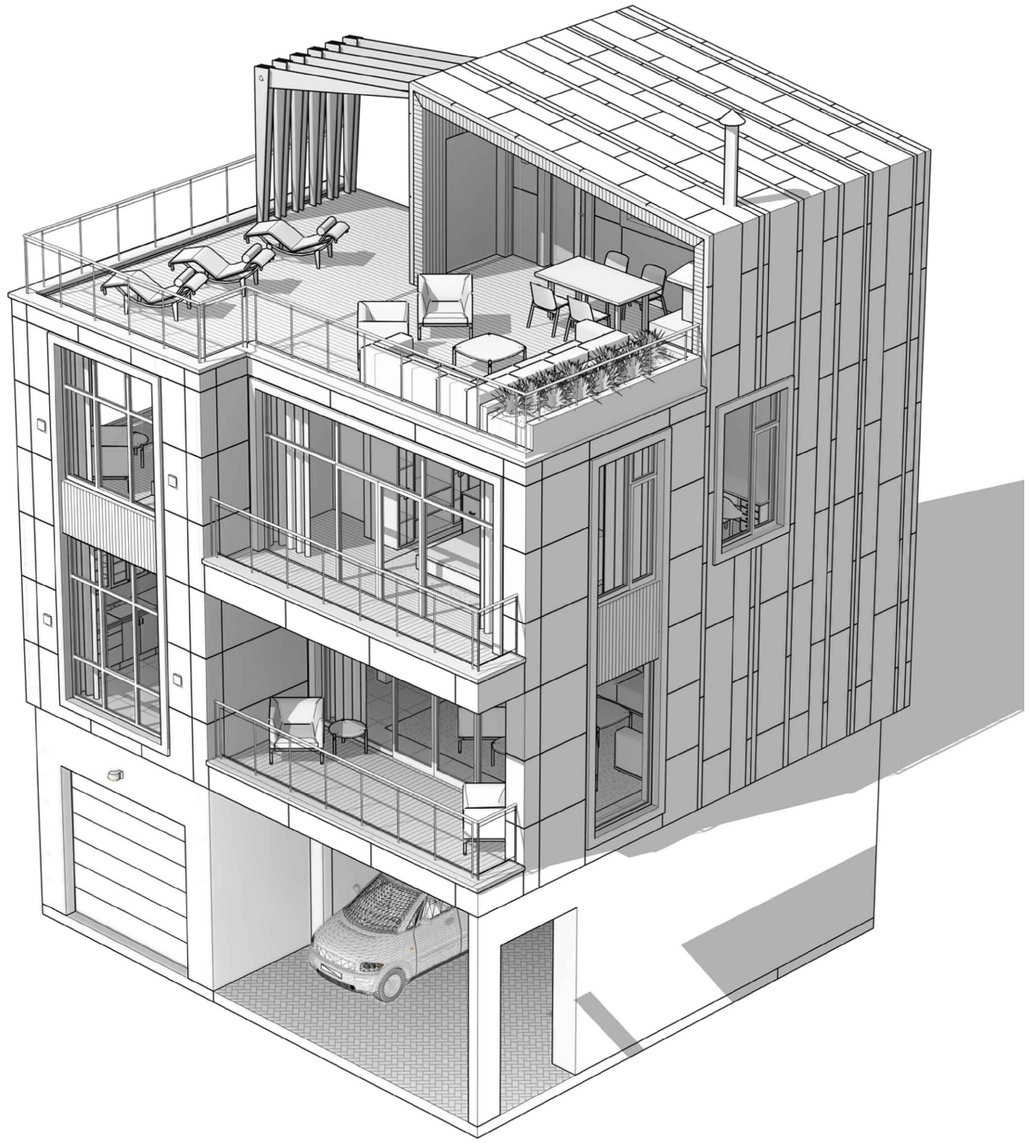

L.B.O.S.
DESIGN

L.B.O.S.
DESIGN

Экспликация помещений. Цокольный этаж		
№	Наименование	Площадь
01	Открытый гараж	27 m²
02	Гараж	26 m²
03	Лестница	12 m²
		64 m²

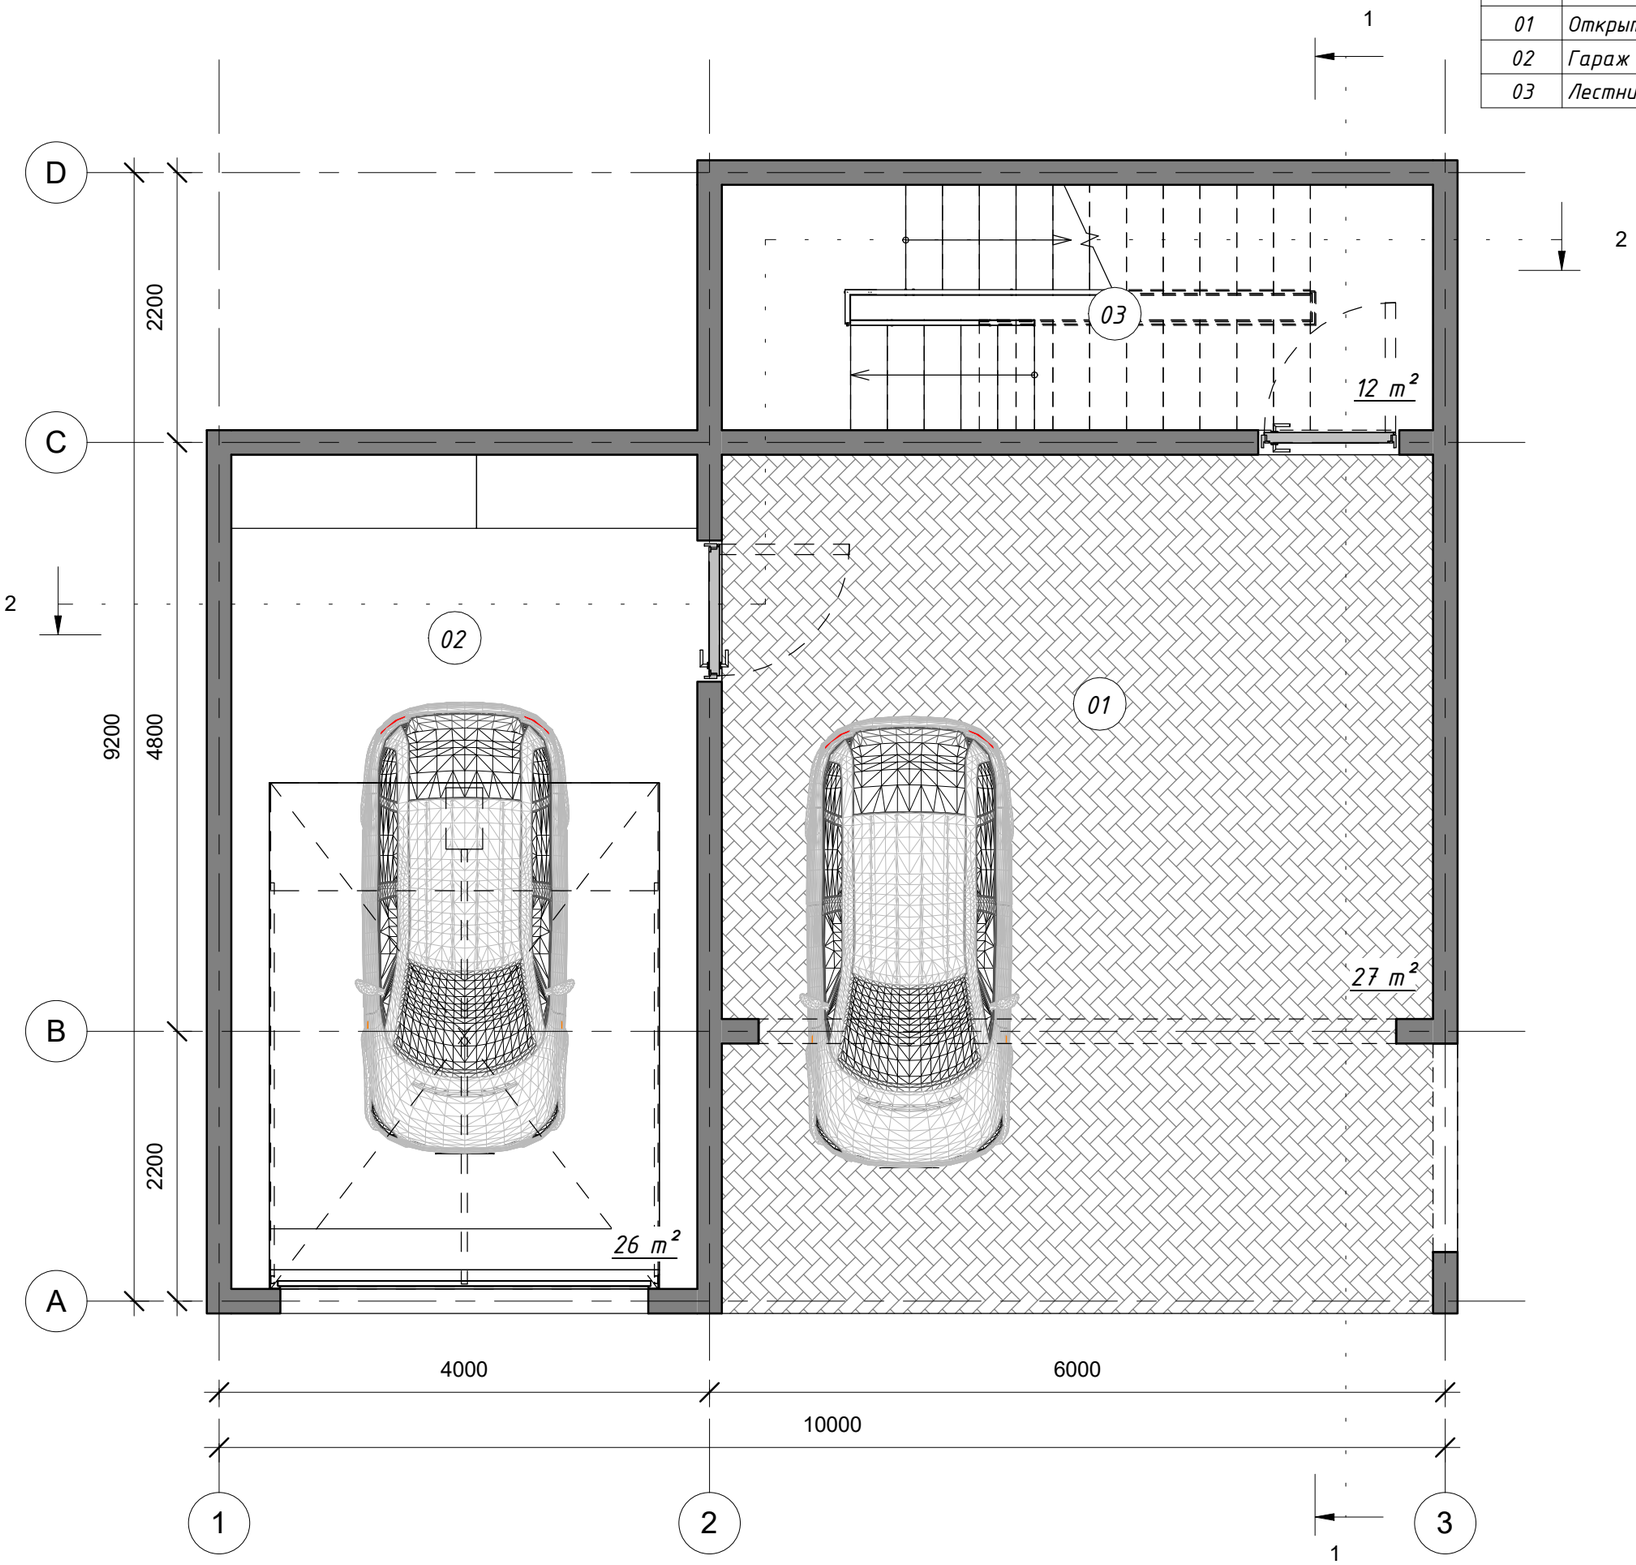

L.B.O.S.
DESIGN

№	Описание	Дата

Batumi Investment
SeaView Garden Villa. №2

Стадия (Stage): Эскиз (Concept)

Цокольный этаж. План

Номер проекта	0001
Дата	03.04.2021
Чертил	Сидорук О.
Проверил	

A101

Масштаб	1 : 50

5/10/2021 10:11:22 AM

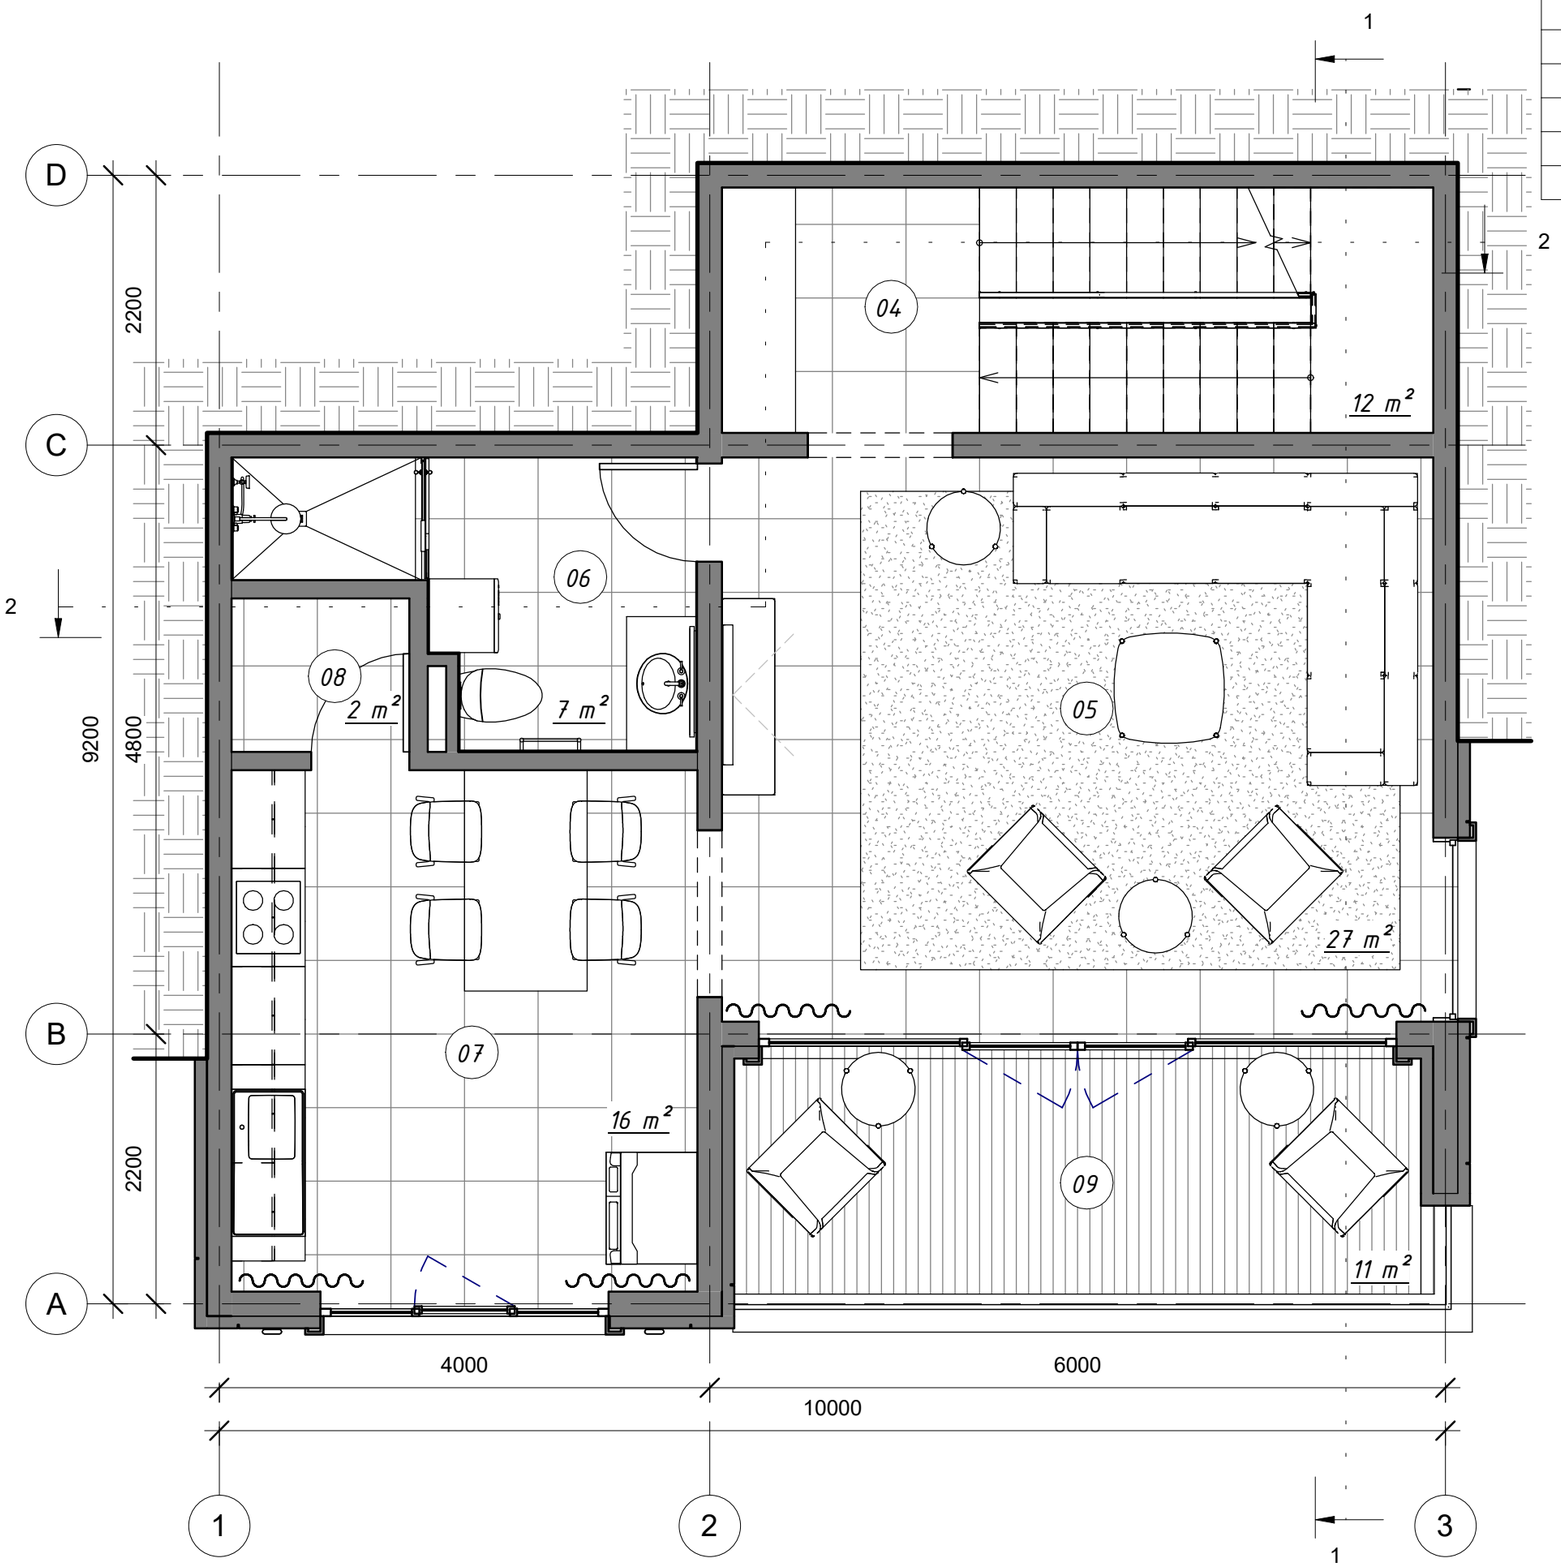

Экспликация помещений. Этаж 1

№	Наименование	Площадь
04	Лестница	12 m²
05	Гостиная	27 m²
06	Ванная комната	7 m²
07	Кухня-столовая	16 m²
08	Котельня	2 m²
09	Терраса	11 m²
		74 m²

L.B.O.S.
DESIGN

№	Описание	Дата

Batumi Investment
SeaView Garden Villa. №2

Стадия (Stage): Эскиз (Concept)

Этаж 1. План

Номер проекта	0001
Дата	03.04.2021
Чертил	Сидорук О.
Проверил	

A102

Масштаб	1 : 50

5/10/2021 10:11:26 AM

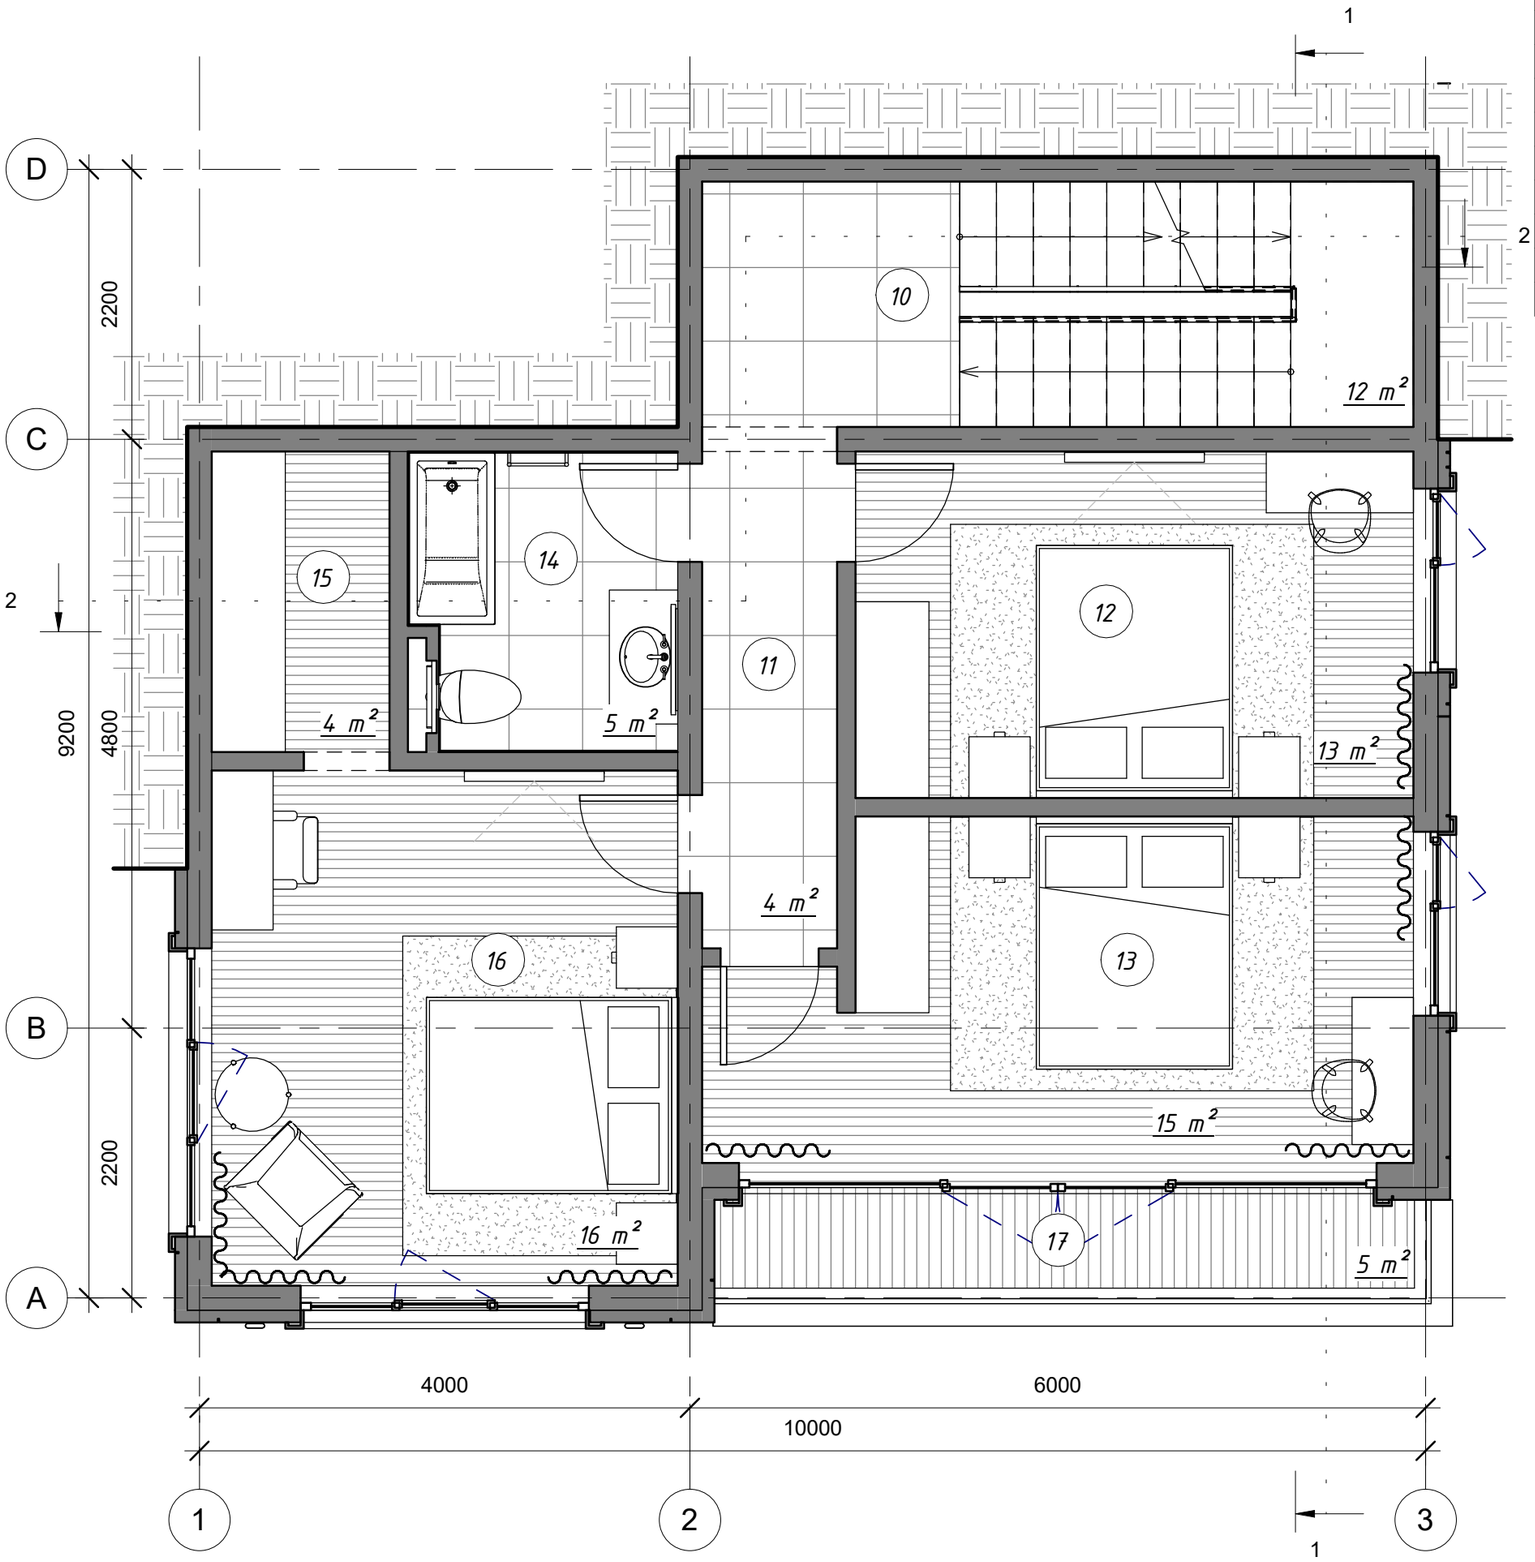

Экспликация помещений. Этаж 2

№	Наименование	Площадь
10	Лестница	12 m²
11	Коридор	4 m²
12	Спальня	13 m²
13	Спальня	15 m²
14	Ванная комната	5 m²
15	Гардероб	4 m²
16	Спальня	16 m²
17	Балкон	5 m²
		73 m²

L.B.O.S.
DESIGN

№	Описание	Дата

Batumi Investment
SeaView Garden Villa. №2

Стадия (Stage): Эскиз (Concept)

Этаж 2. План

Номер проекта	0001
Дата	03.04.2021
Чертил	Сидорук О.
Проверил	

A103

Масштаб	1 : 50

5/10/2021 10:11:28 AM

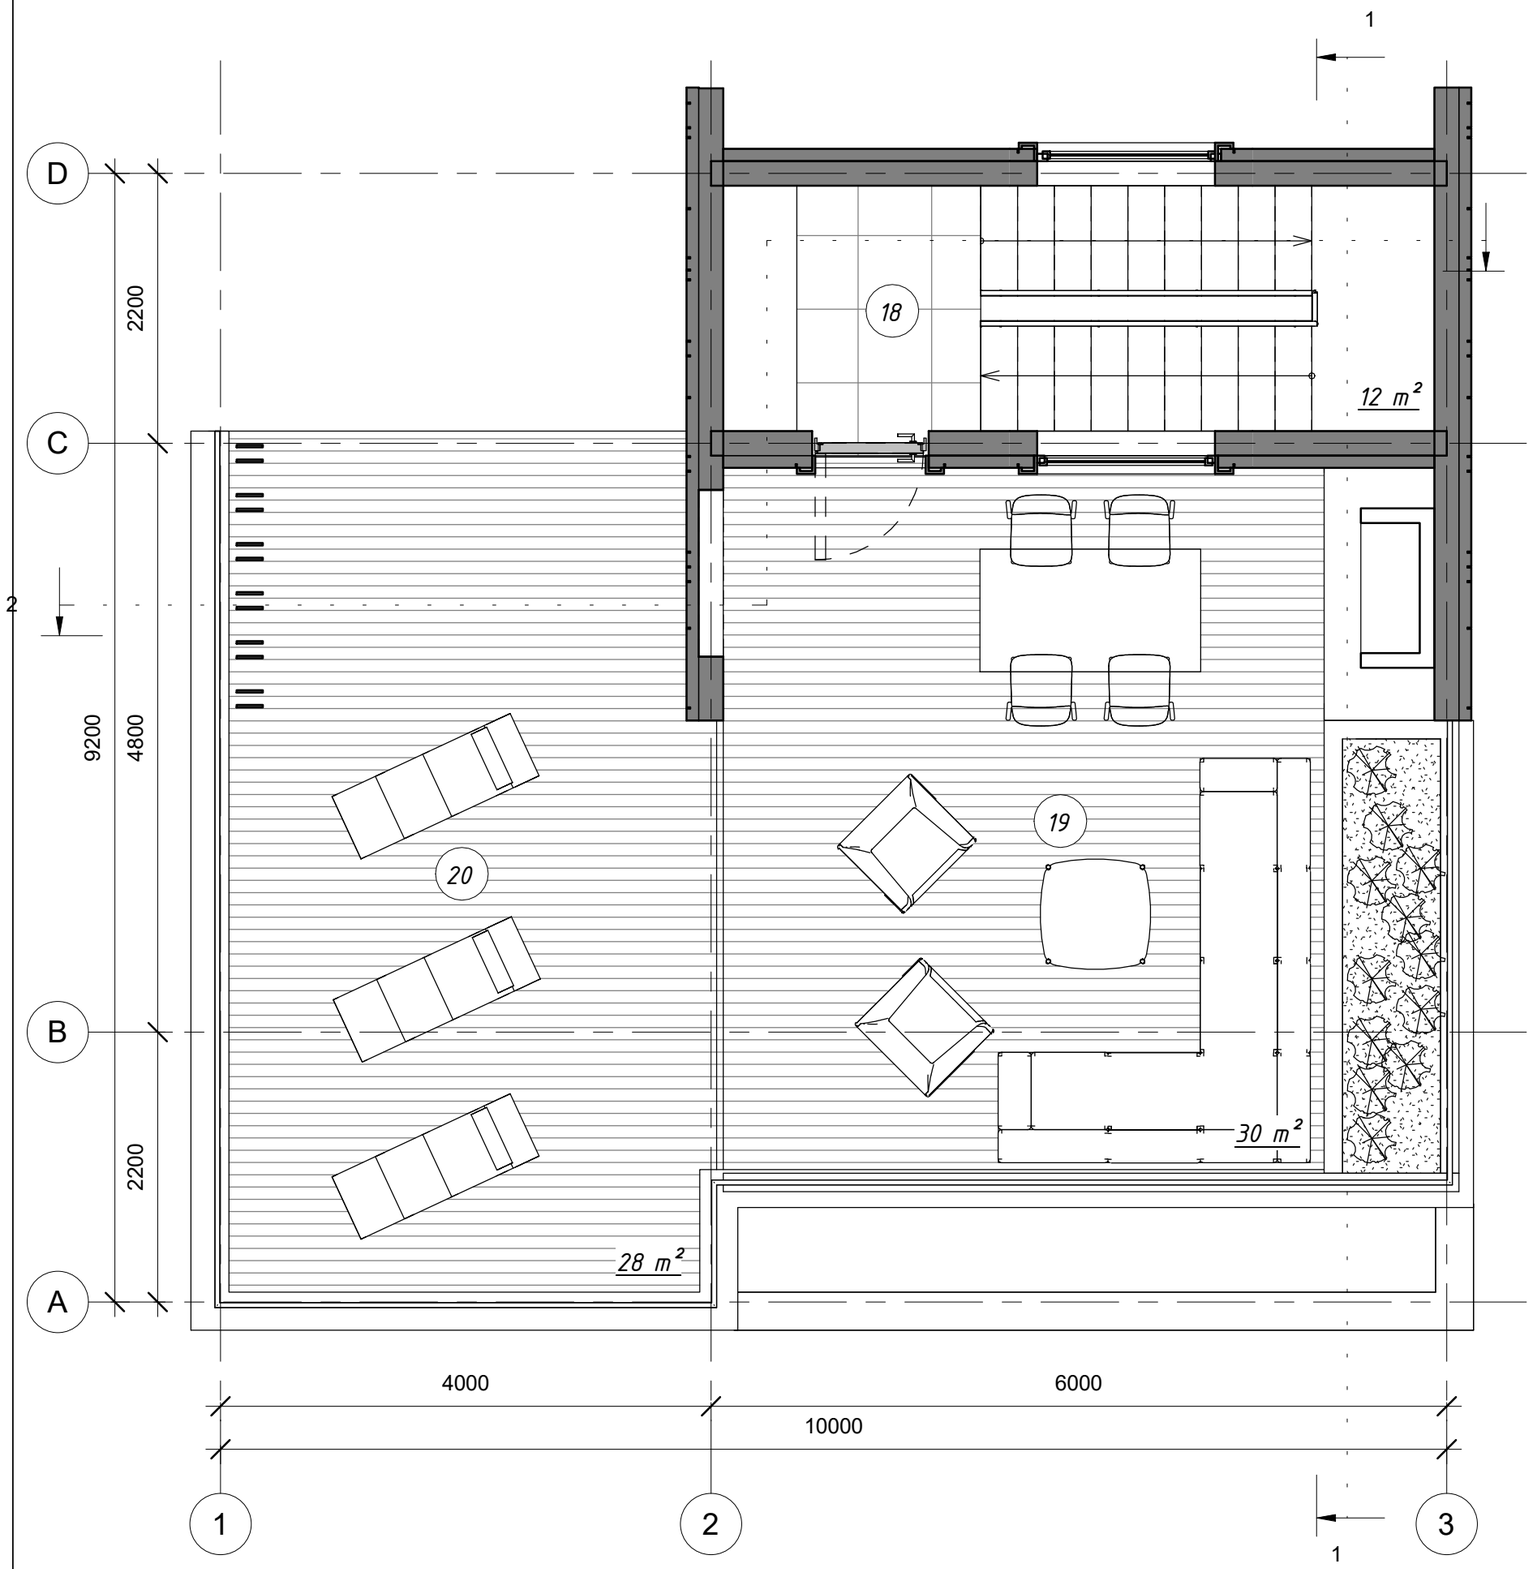

Экспликация помещений. Этаж 3		
№	Наименование	Площадь
18	Лестница	12 m²
19	Терраса	30 m²
20	Терраса	28 m²
		69 m²

L.B.O.S.
DESIGN

№	Описание	Дата

Batumi Investment
SeaView Garden Villa. №2

Стадия (Stage): Эскиз (Concept)

Этаж 3. План

Номер проекта	0001
Дата	03.04.2021
Чертил	Сидорук О.
Проверил	

A104

Масштаб	1 : 50

5/10/2021 10:11:30 AM

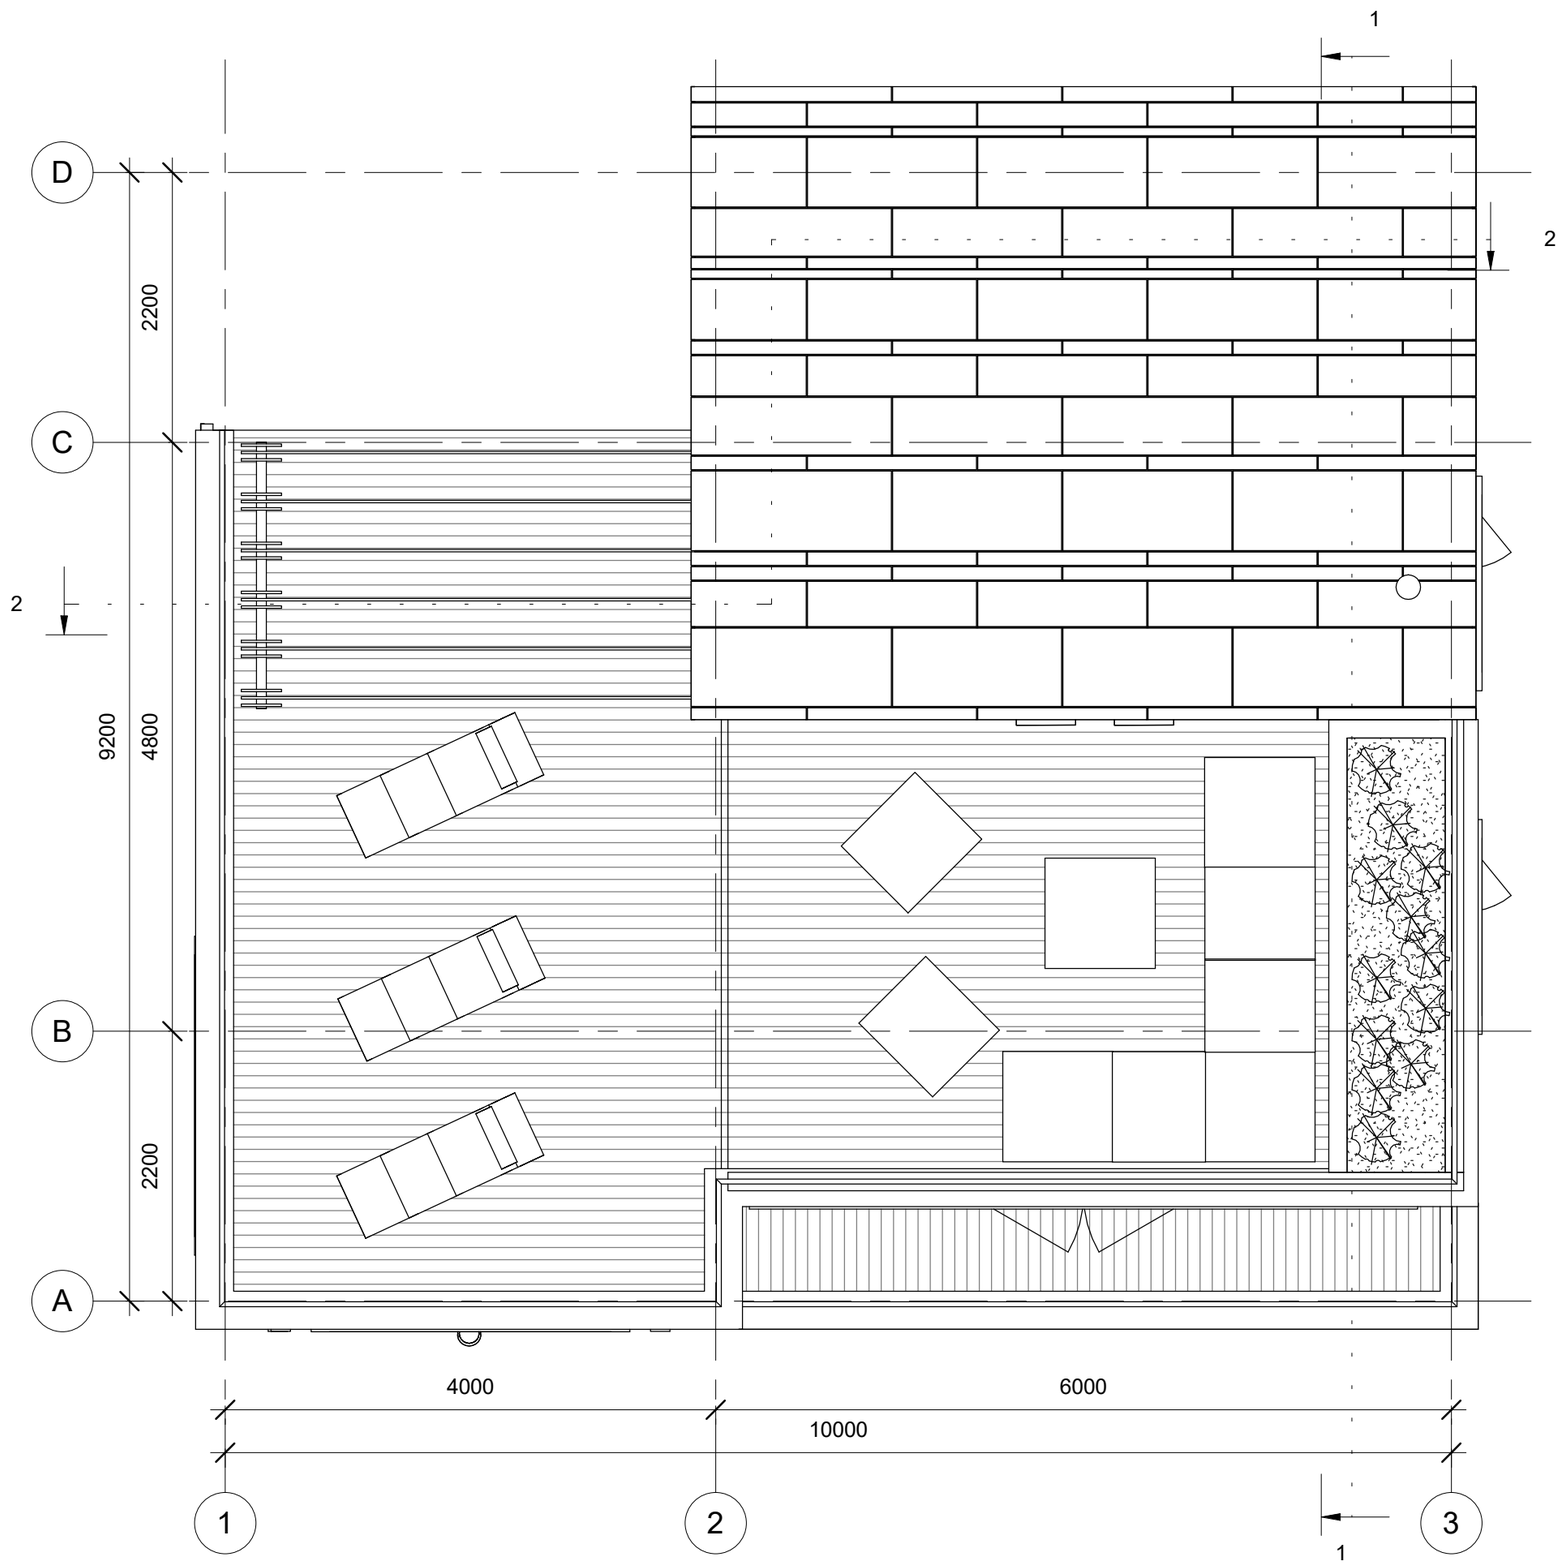

L.B.O.S.
DESIGN

№	Описание	Дата

Batumi Investment
SeaView Garden Villa. №2

Стадия (Stage): Эскиз (Concept)

План кровли

Номер проекта	0001
Дата	03.04.2021
Чертил	Сидорук О.
Проверил	

A105

Масштаб	1 : 50

5/10/2021 10:11:30 AM

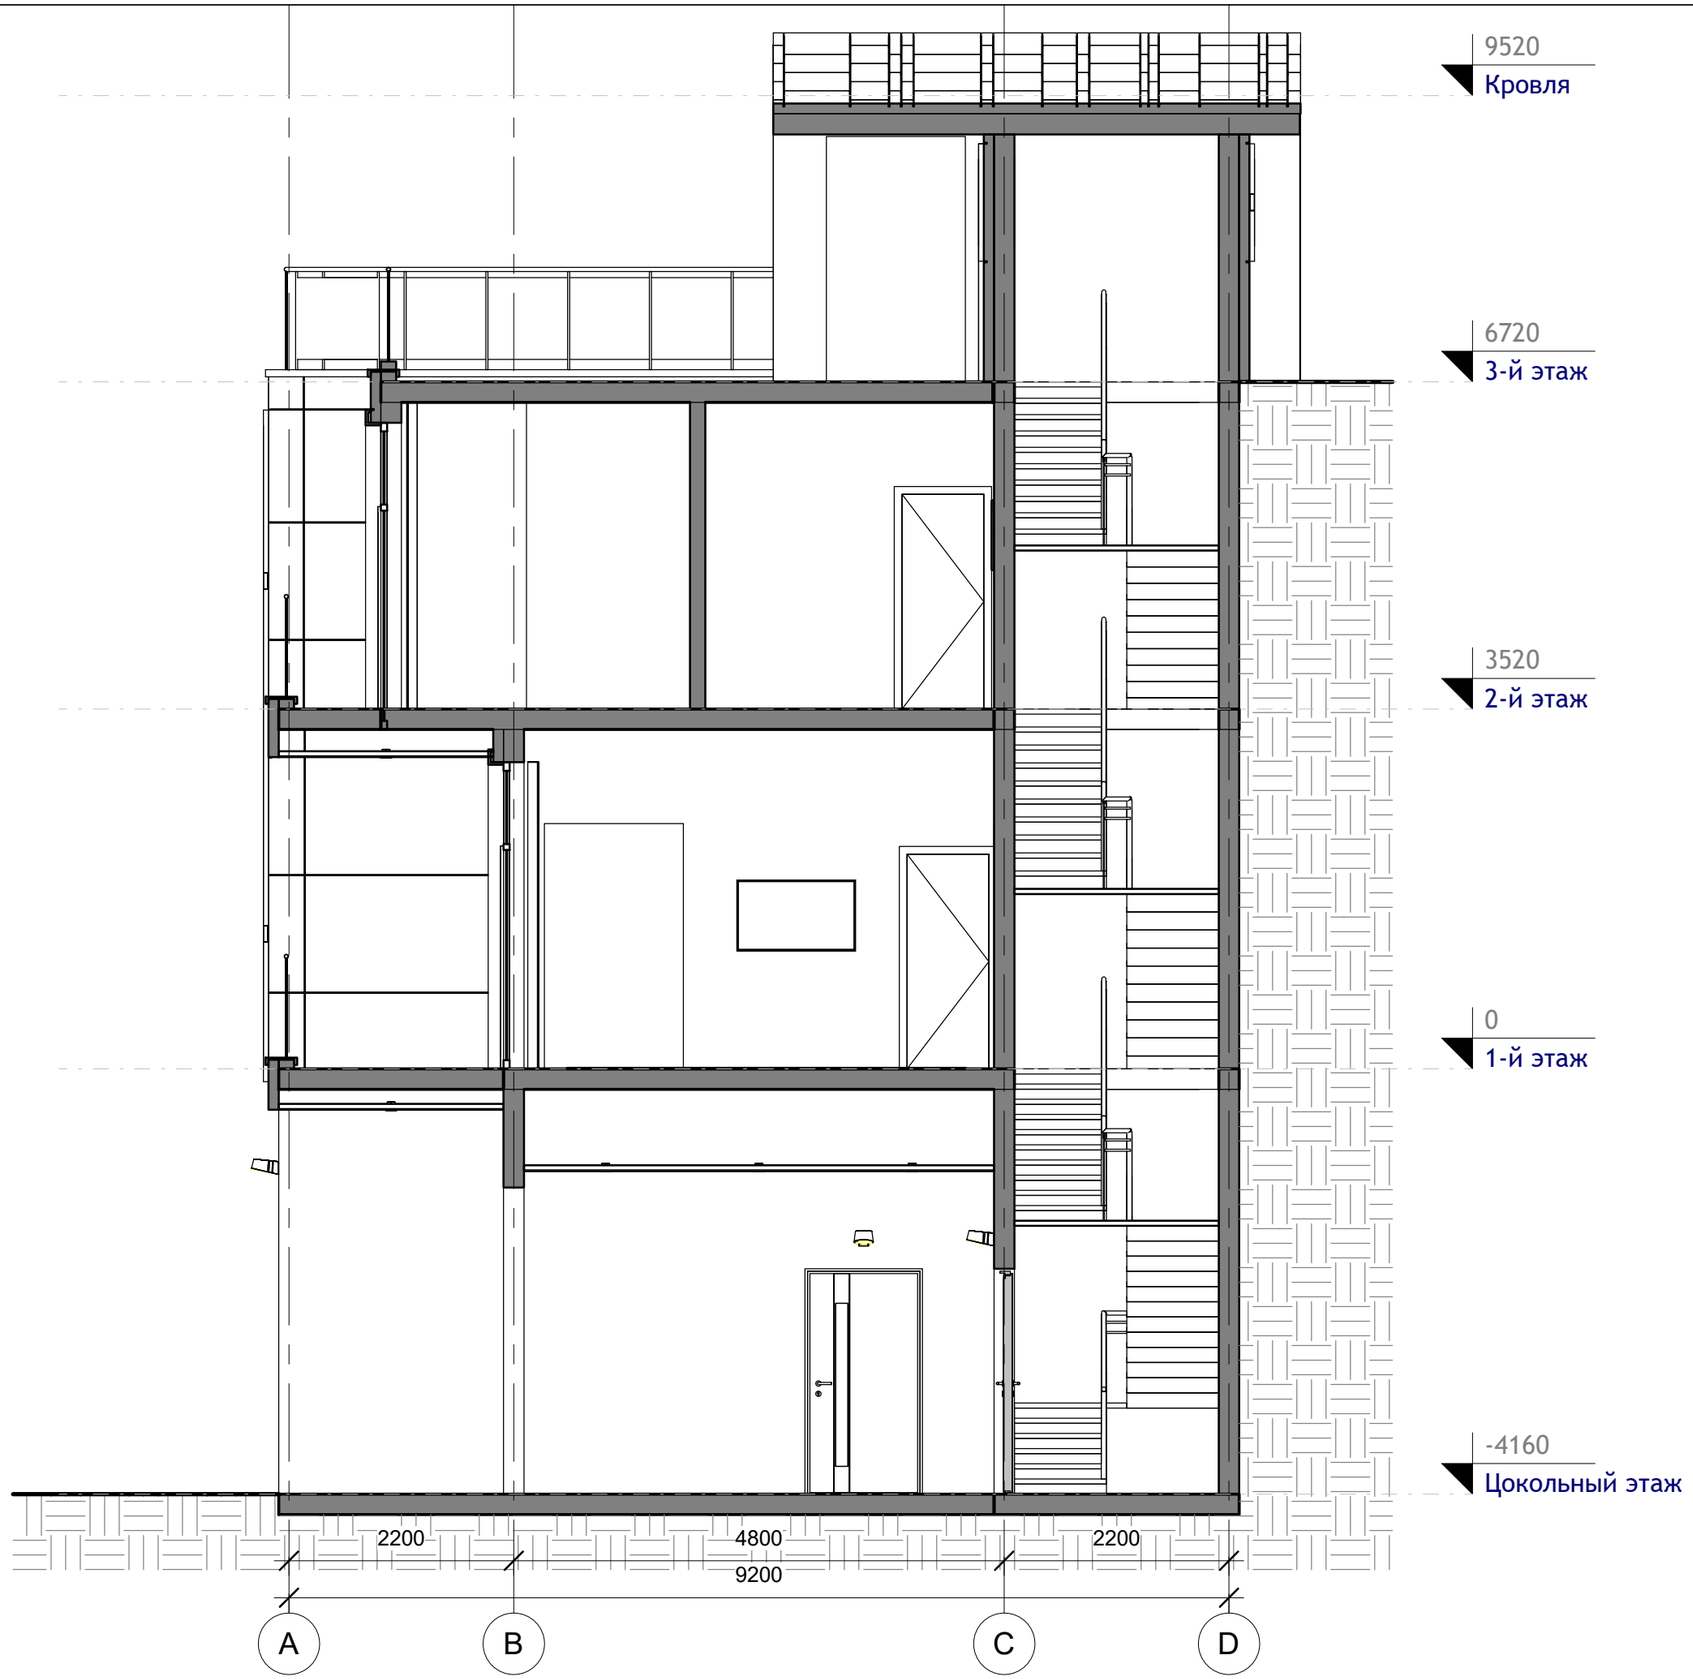

L.B.O.S.
DESIGN

№	Описание	Дата

Batumi Investment
SeaView Garden Villa. №2

Стадия (Stage): Эскиз (Concept)

Разрез 1-1

Номер проекта	0001
Дата	03.04.2021
Чертил	Сидорук О.
Проверил	

A106

Масштаб	1 : 60

5/10/2021 10:11:31 AM

L.B.O.S.
DESIGN

№	Описание	Дата

Batumi Investment
SeaView Garden Villa. №2

Стадия (Stage): Эскиз (Concept)

Разрез 2-2

Номер проекта	0001
Дата	03.04.2021
Чертил	Сидорук О.
Проверил	

A107

Масштаб	1 : 60

5/10/2021 10:11:32 AM

L.B.O.S.
DESIGN

№	Описание	Дата

Batumi Investment
SeaView Garden Villa. №2

Стадия (Stage): Эскиз (Concept)

Фасад в осях 1-3

Номер проекта	0001
Дата	03.04.2021
Чертил	Сидорук О.
Проверил	

A108

Масштаб	1 : 60

5/10/2021 10:11:36 AM

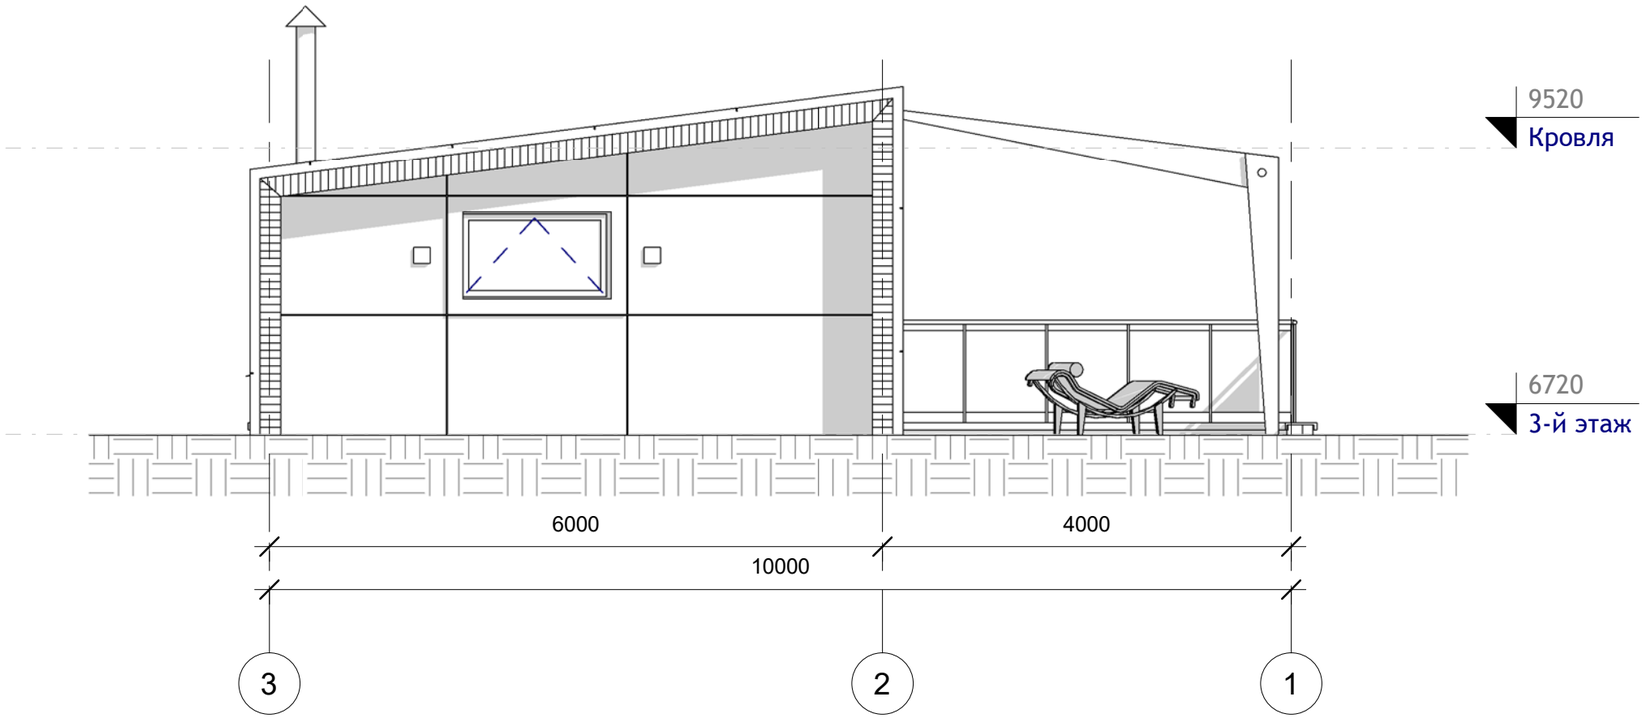

L.B.O.S.
DESIGN

№	Описание	Дата

Batumi Investment
SeaView Garden Villa. №2

Стадия (Stage): Эскиз (Concept)

Фасад в осях 3-1

Номер проекта	0001
Дата	03.04.2021
Чертил	Сидорук О.
Проверил	

A109

Масштаб	1 : 60

5/10/2021 10:11:37 AM

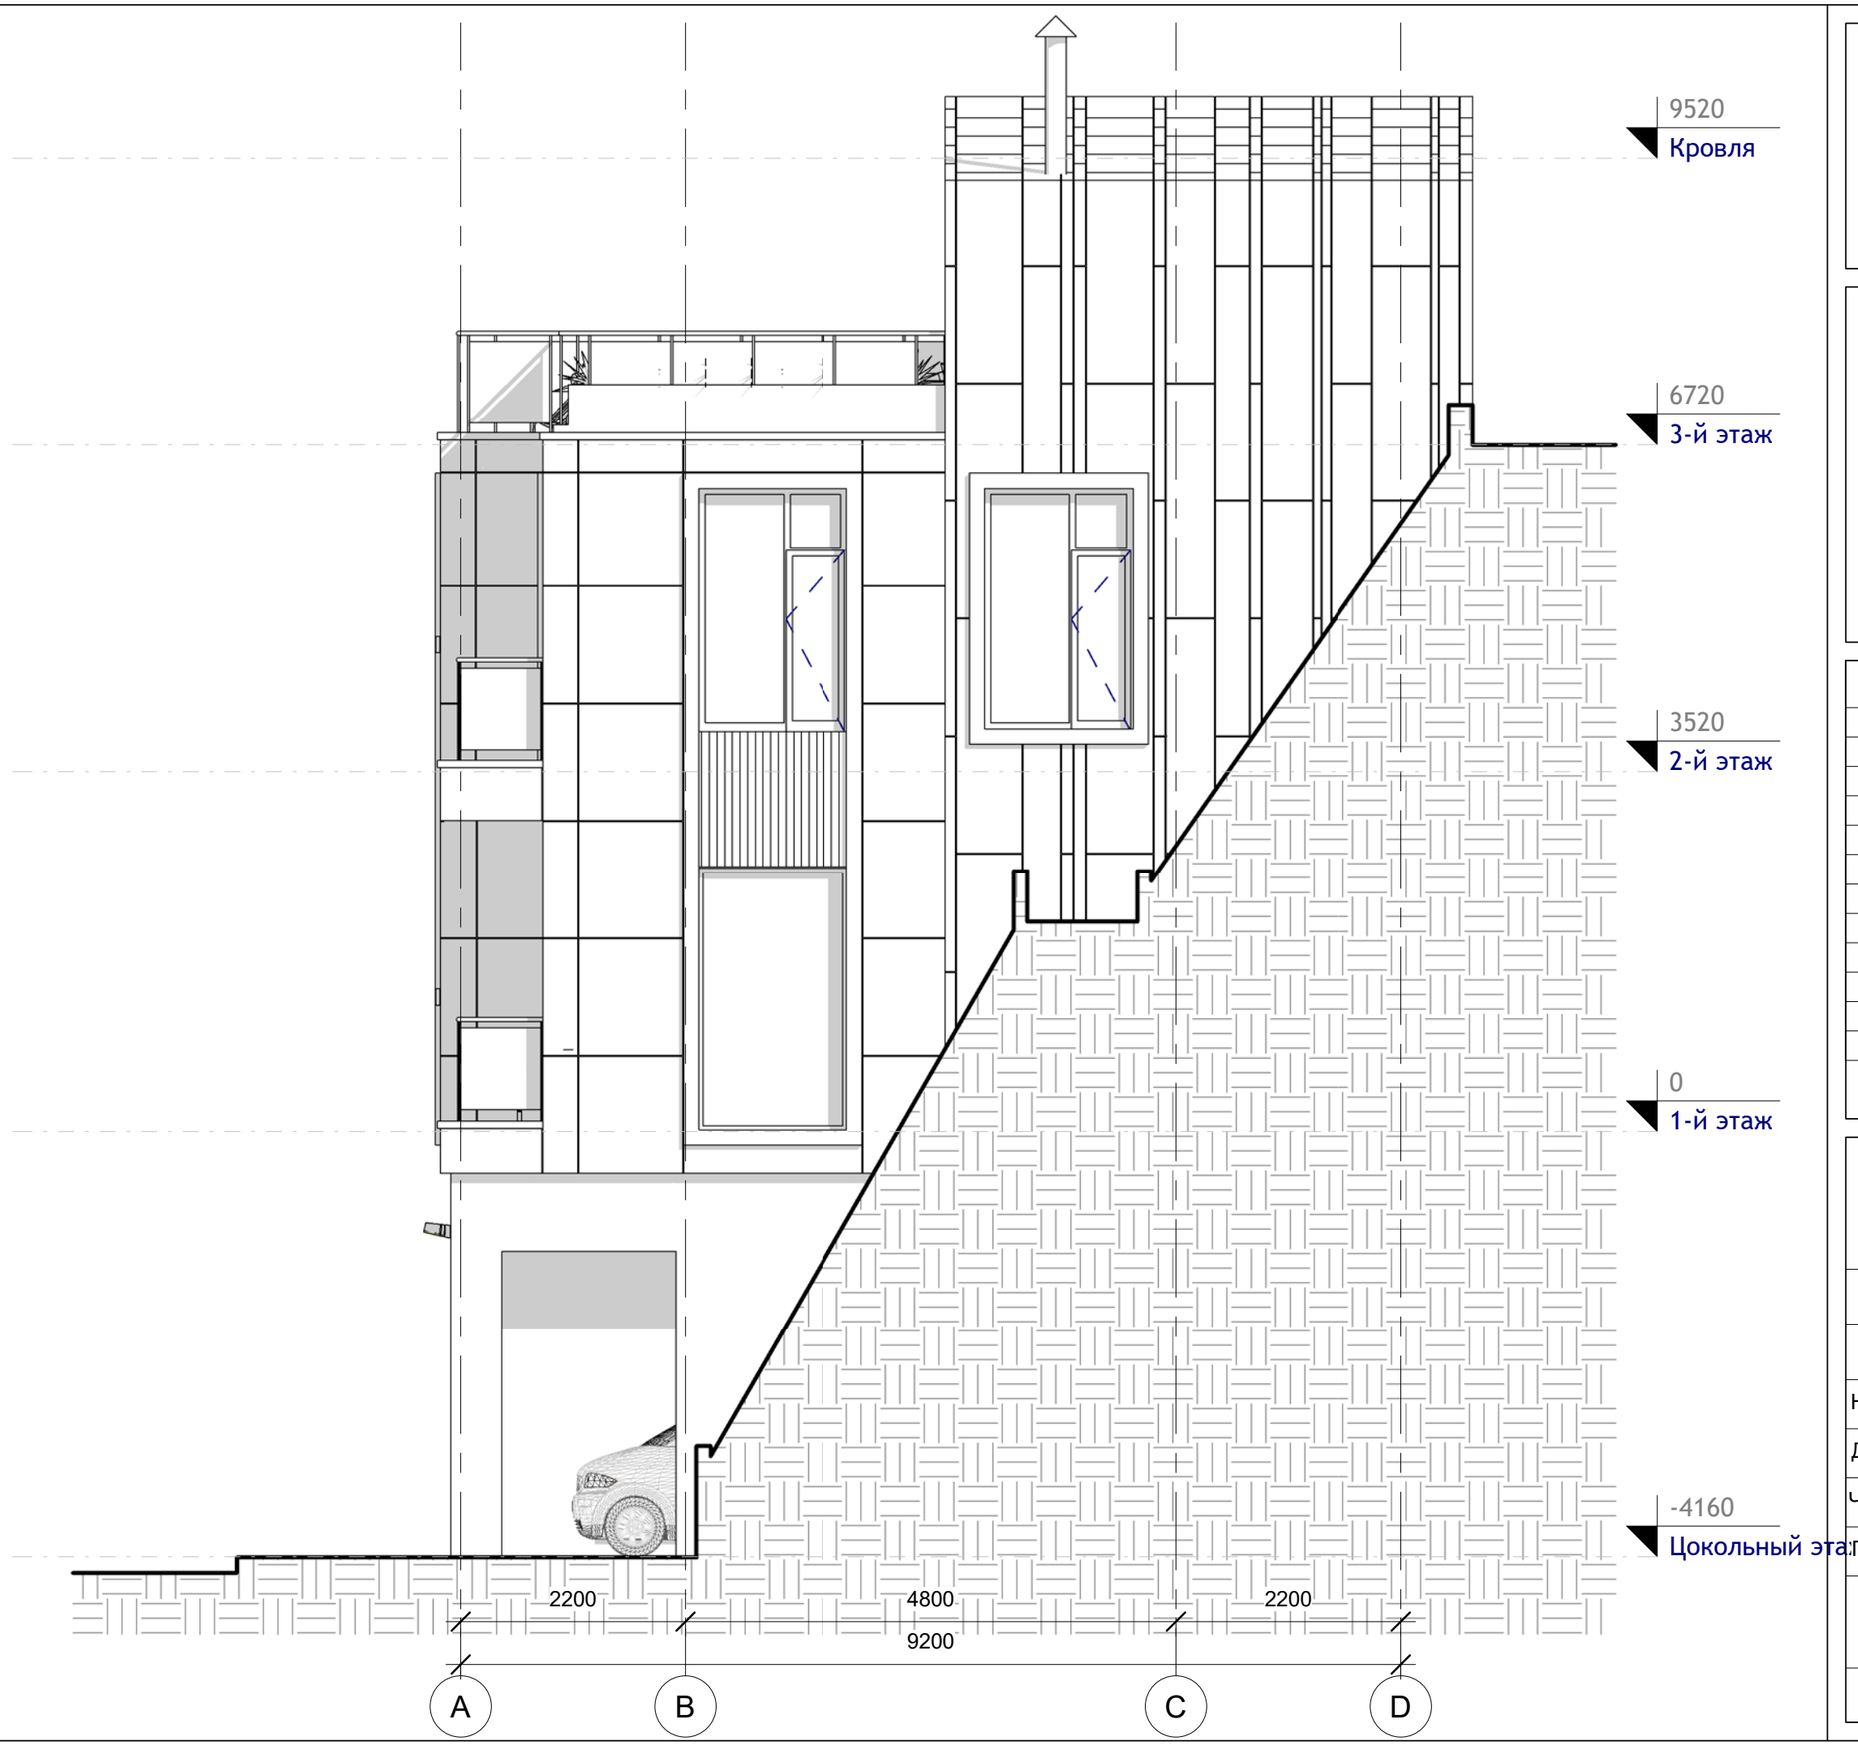

L.B.O.S.
DESIGN

№	Описание	Дата

Batumi Investment
SeaView Garden Villa. №2

Стадия (Stage): Эскиз (Concept)

Фасад в осях A-D

Номер проекта	0001
Дата	03.04.2021
Чертил	Сидорук О.
Проверил	

A110

Масштаб	1 : 60

5/10/2021 10:11:41 AM

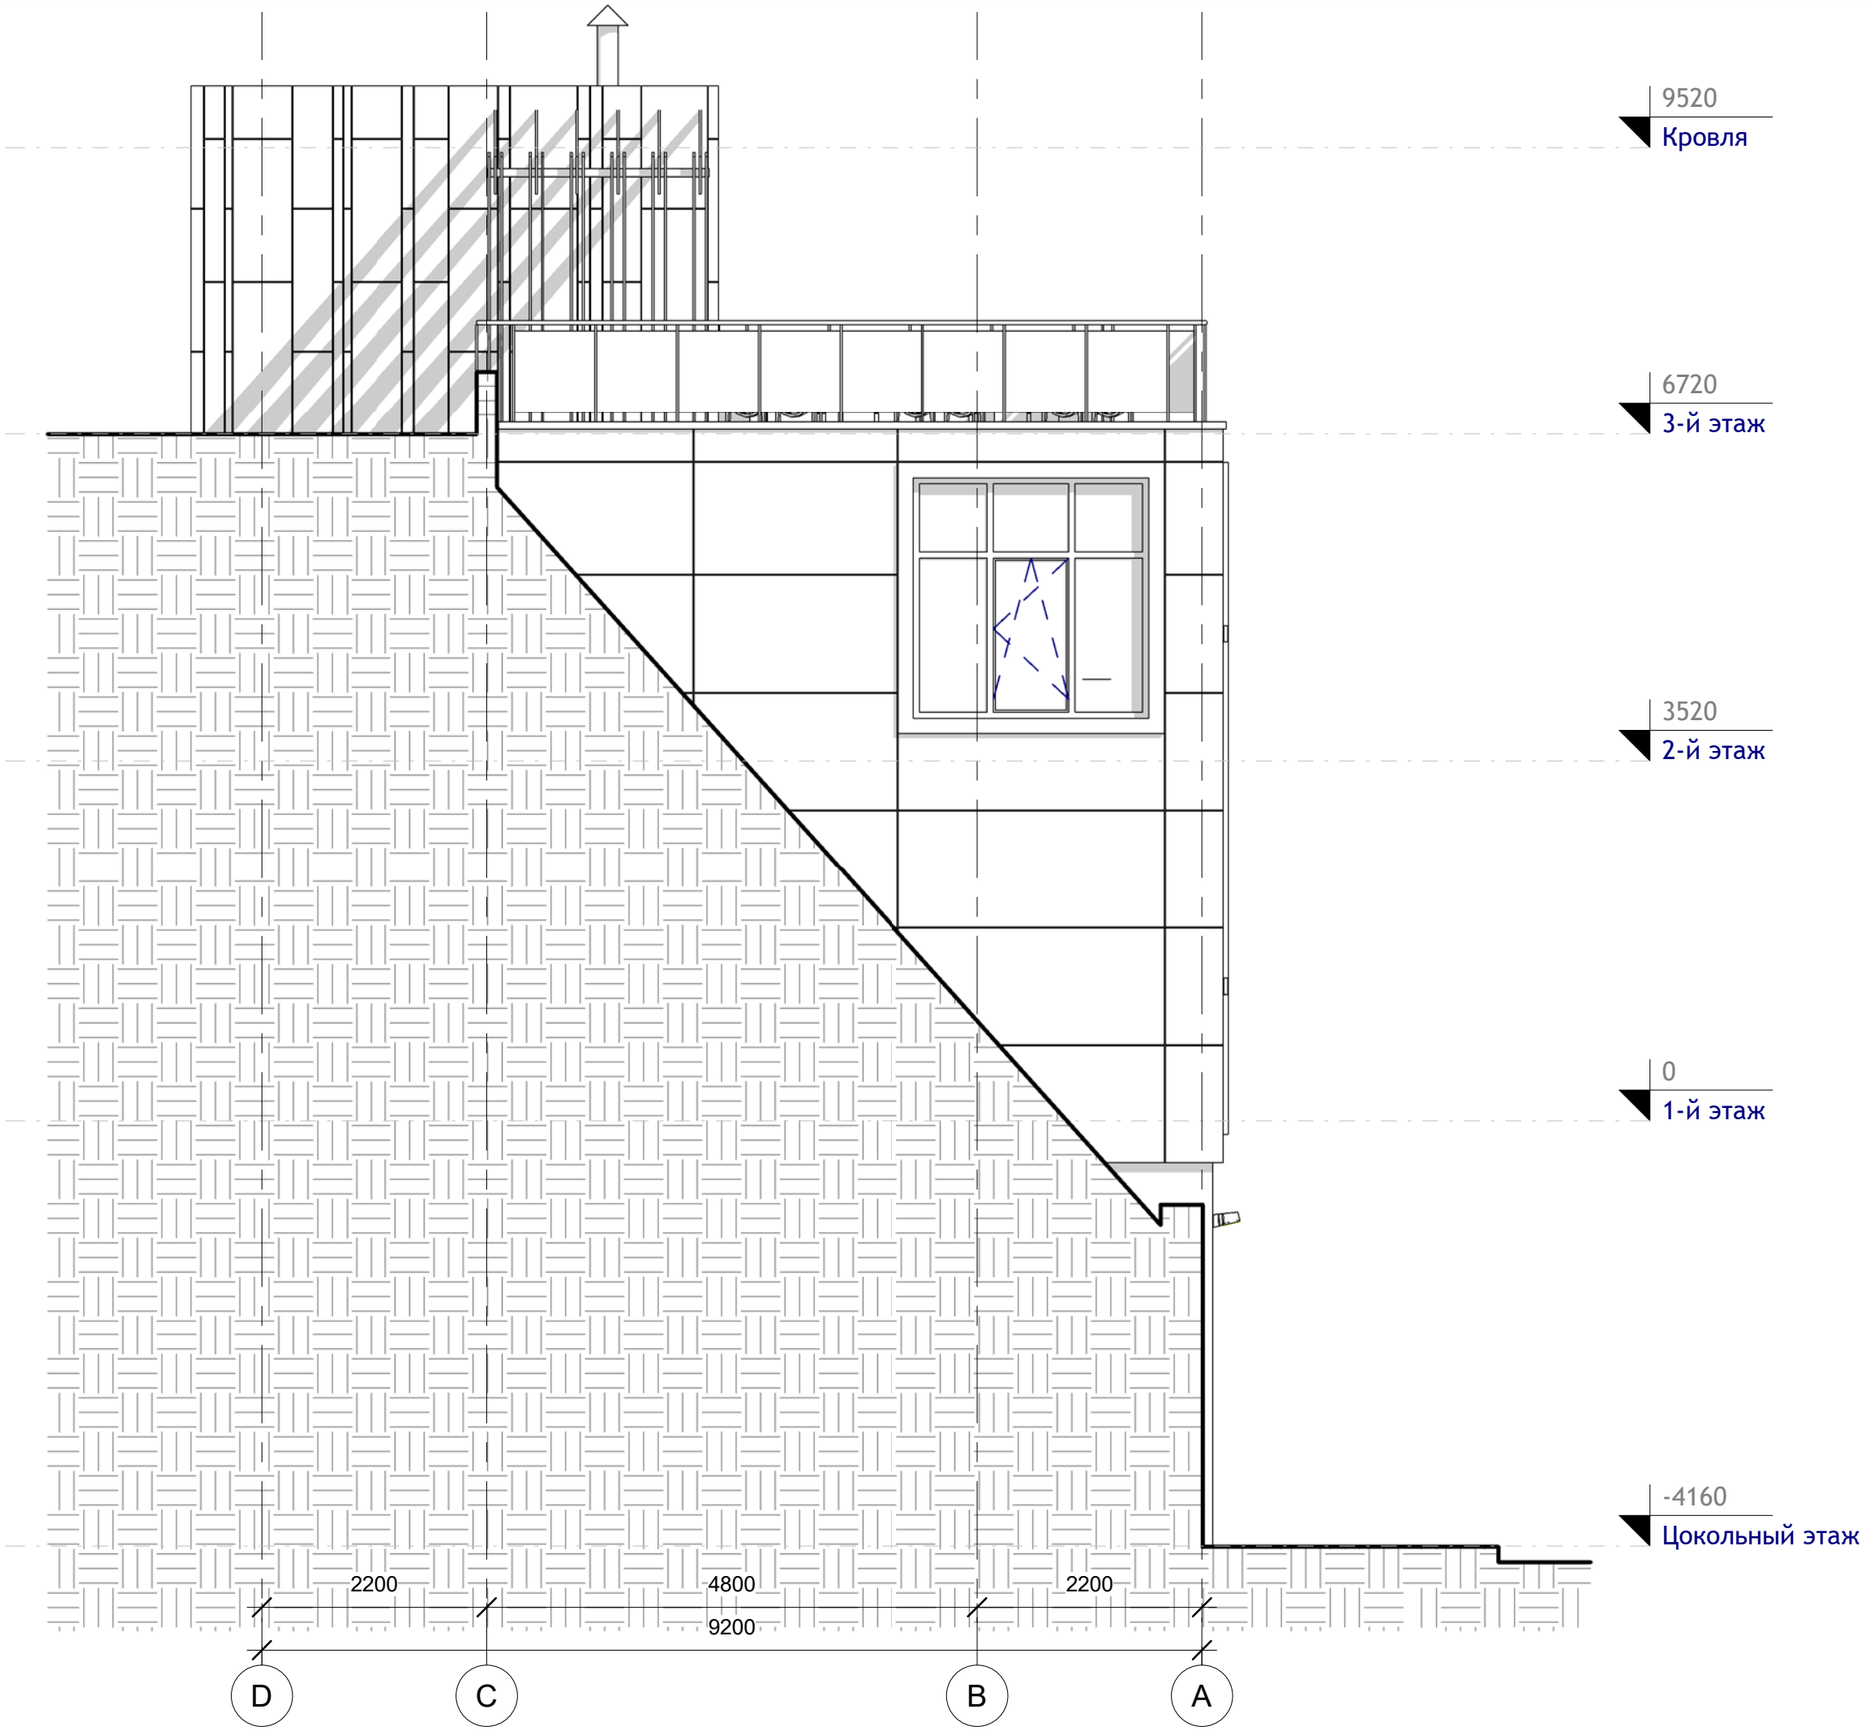

L.B.O.S.
DESIGN

№	Описание	Дата

Batumi Investment
SeaView Garden Villa. №2

Стадия (Stage): Эскиз (Concept)

Фасад в осях D-A

Номер проекта	0001
Дата	03.04.2021
Чертил	Сидорук О.
Проверил	

A111

Масштаб	1 : 60

5/10/2021 10:11:45 AM

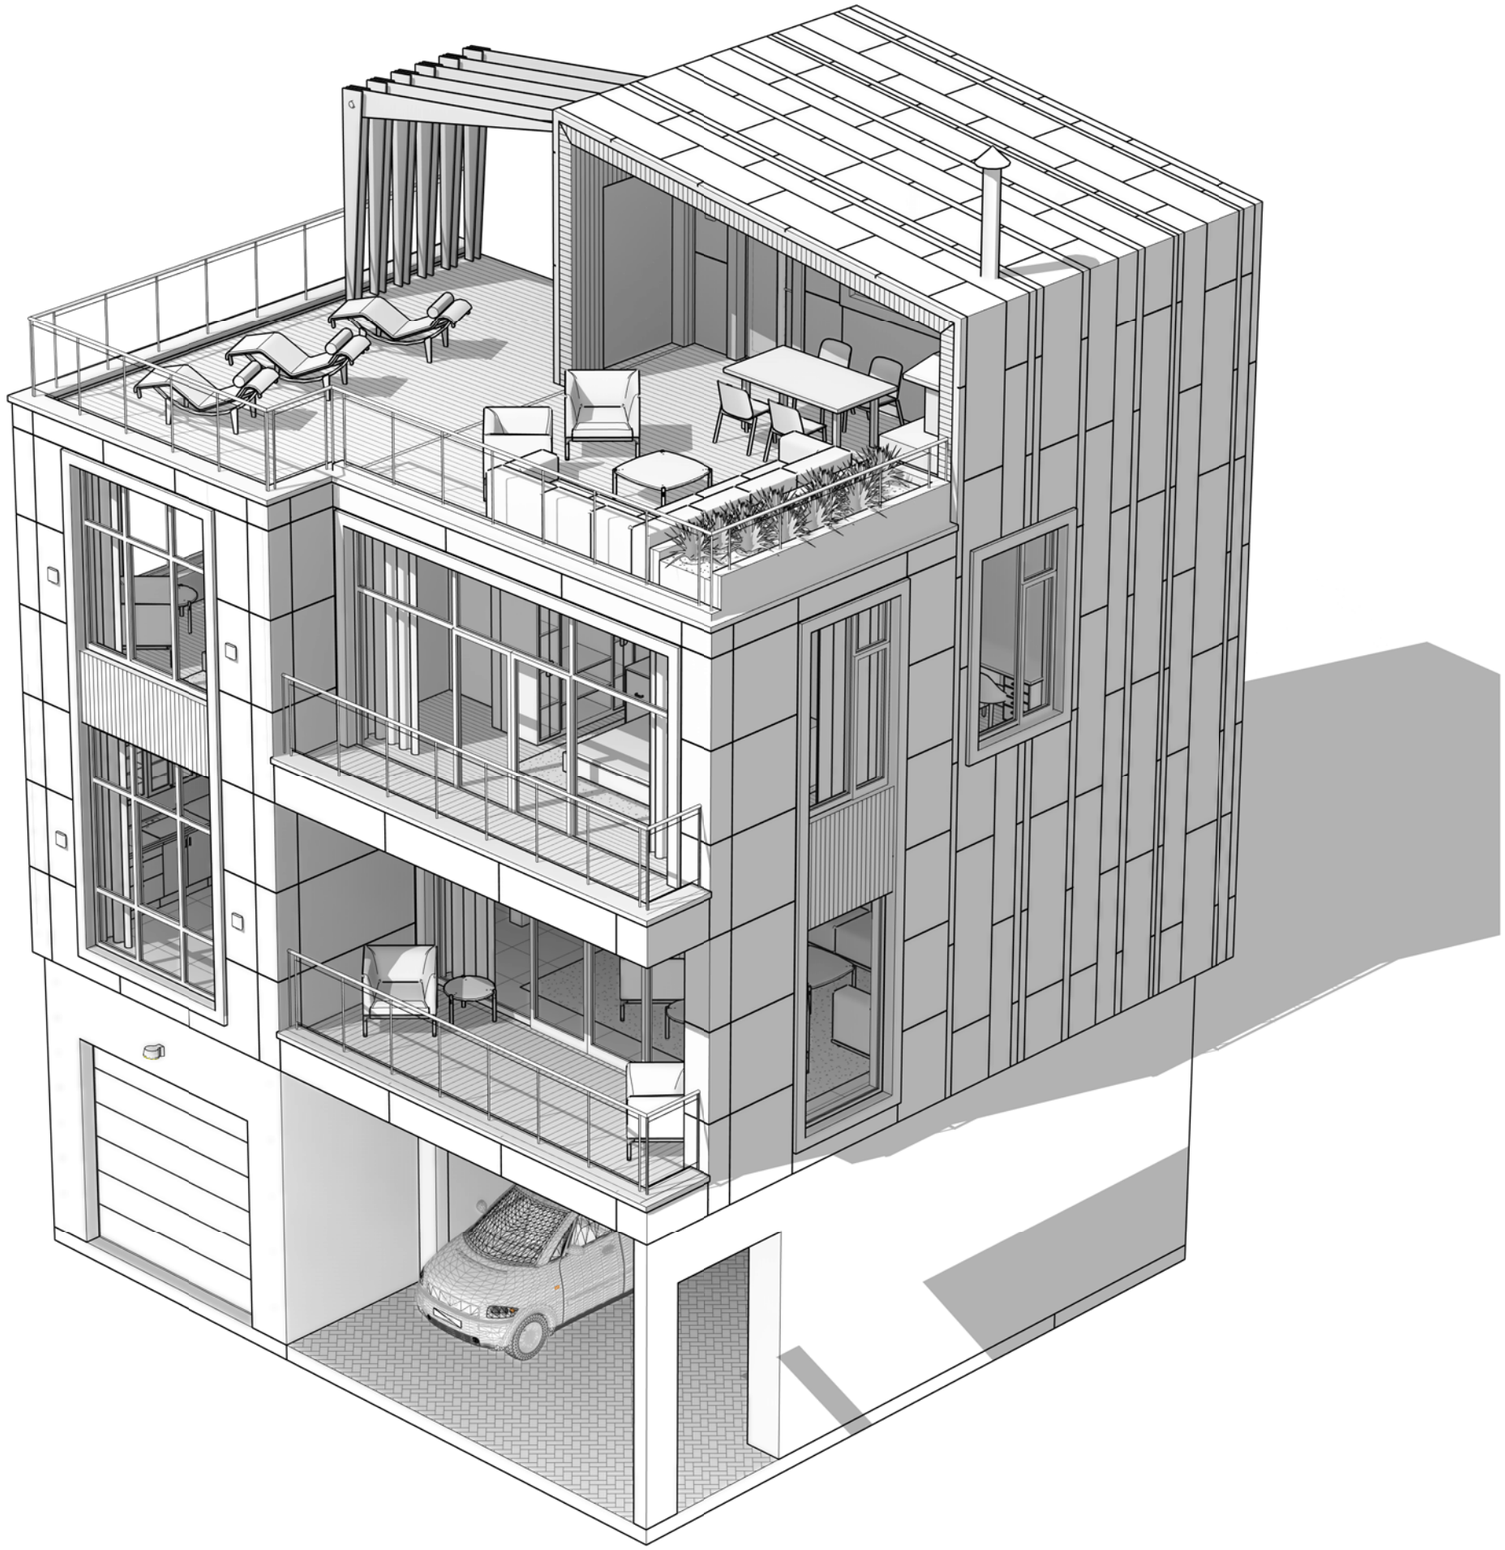

L.B.O.S.
DESIGN

№	Описание	Дата

Batumi Investment
SeaView Garden Villa. №2

Стадия (Stage): Эскиз (Concept)

Перспектива

Номер проекта	0001
Дата	03.04.2021
Чертил	Разработал
Проверил	

A112

Масштаб

5/10/2021 10:11:53 AM