SeaView Garden Villas

Type 3 (288.0 m²)

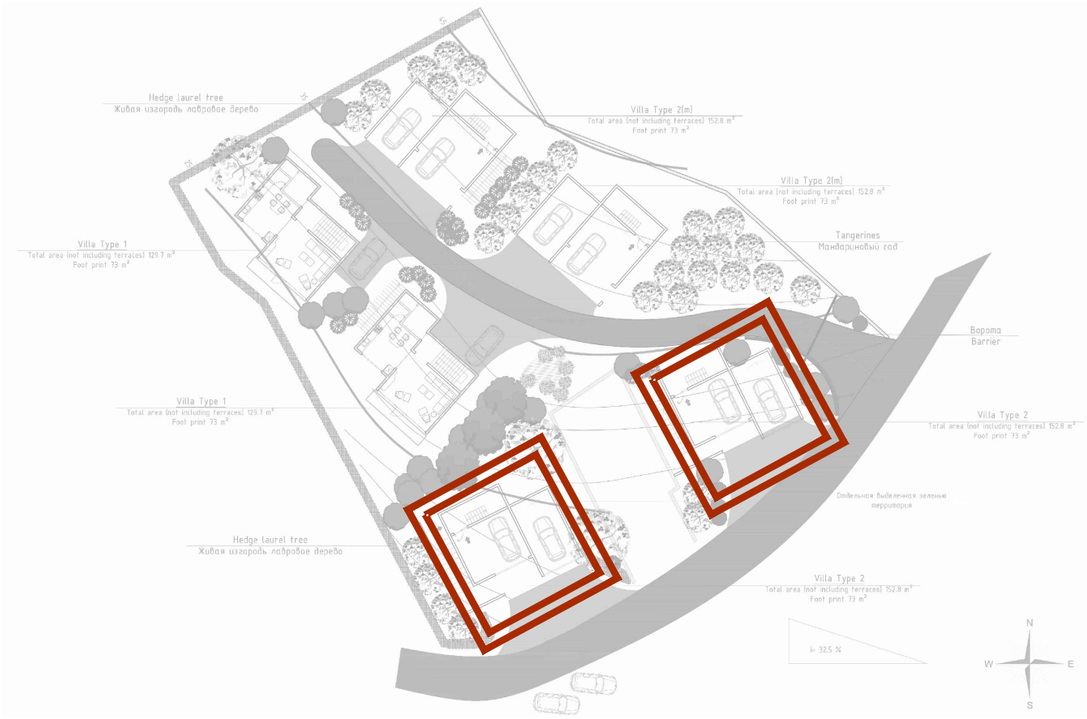

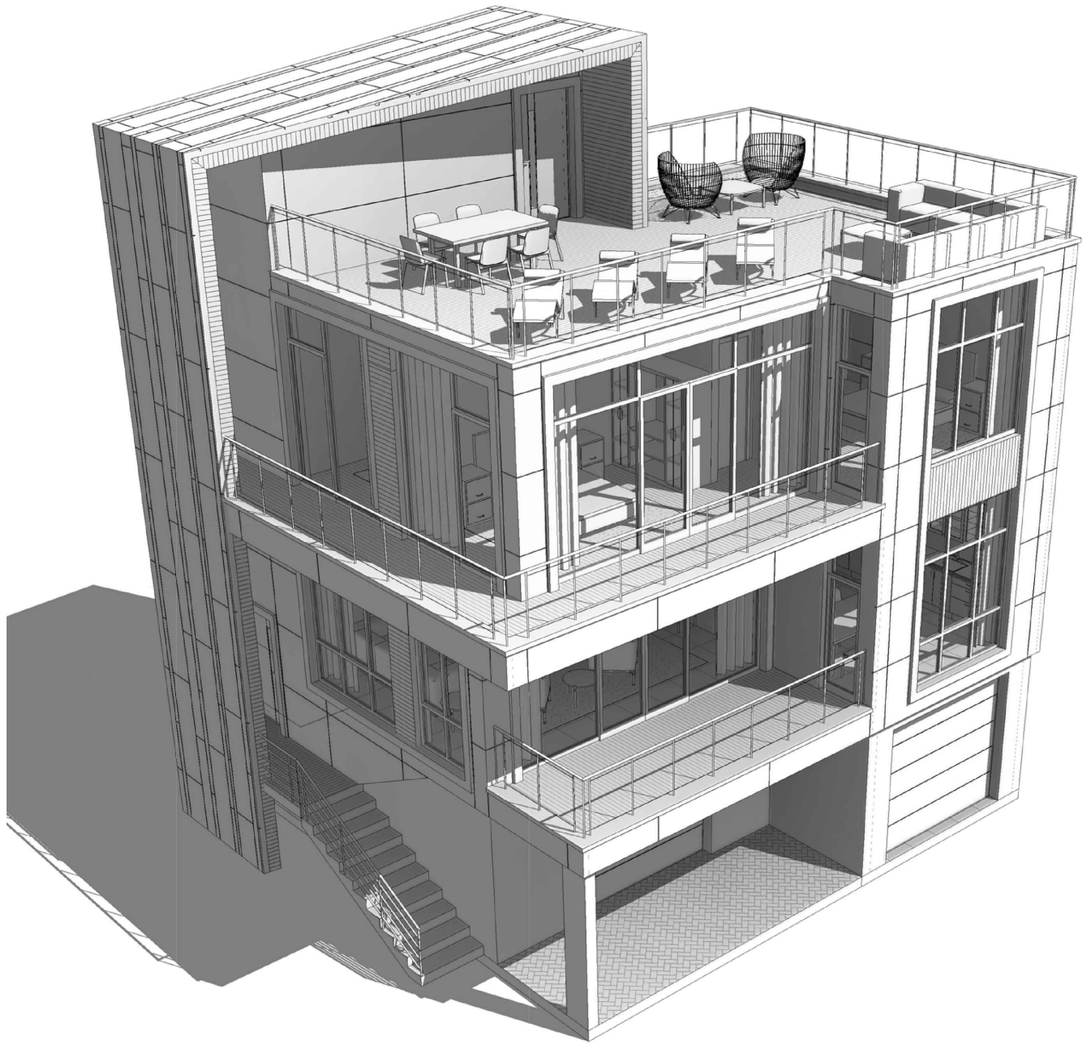

L.B.O.S.
DESIGN

L.B.O.S.
DESIGN

Экспликация помещений. Цокольный этаж		
№	Наименование	Площадь
01	Лестница	11.6 m^2
02	Гараж	25.8 m^2
03	Гараж	26.7 m^2
		64.1 m^2

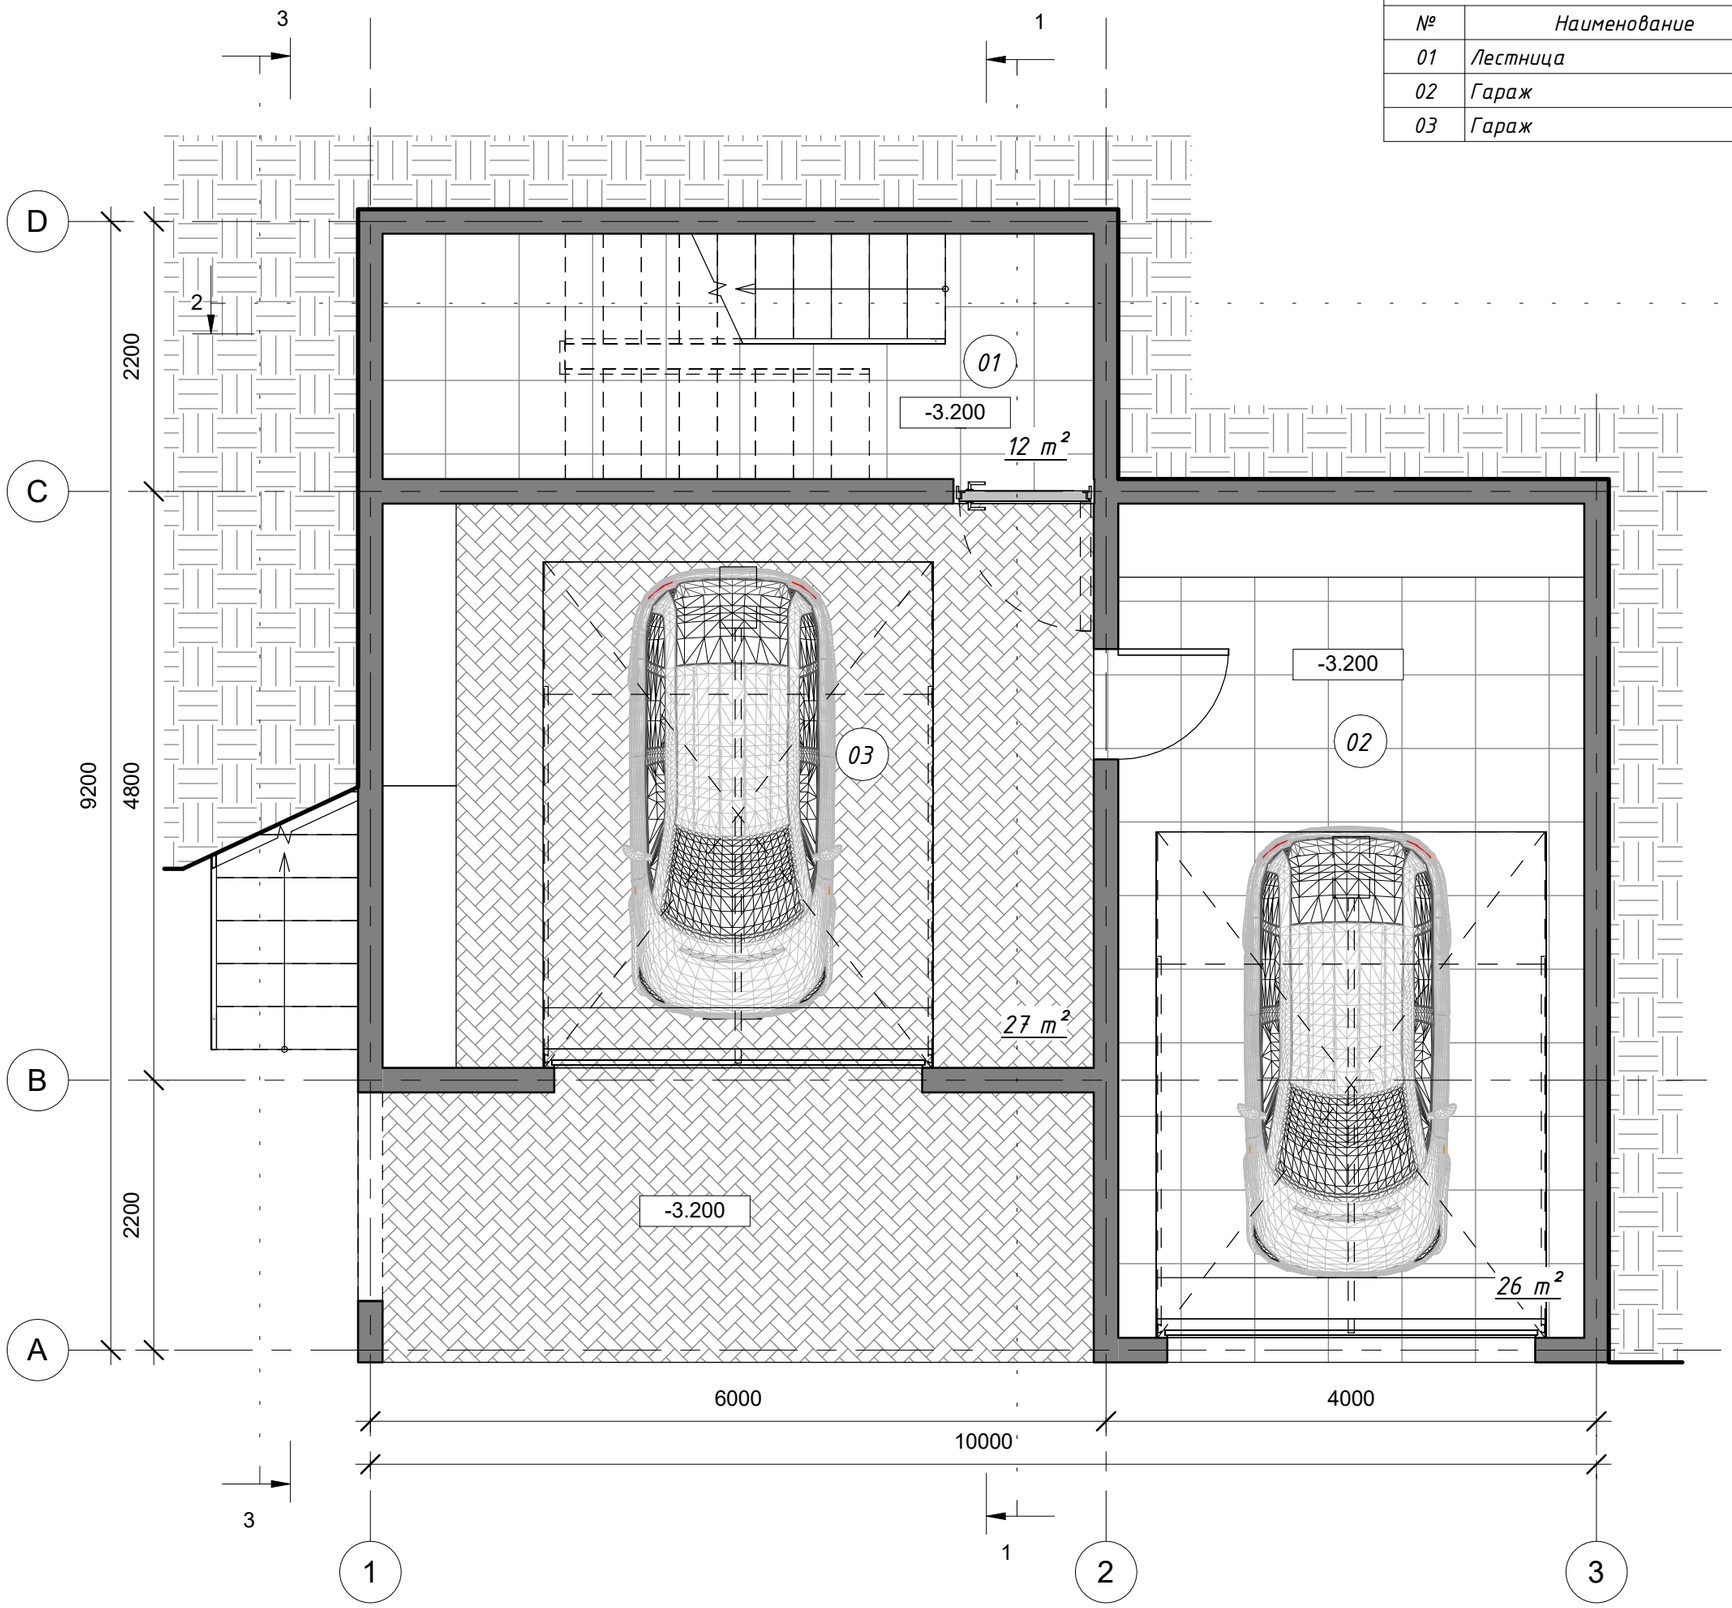

L.B.O.S.
DESIGN

№	Описание	Дата

Batumi Investment
SeaView Garden Villa. №3

Стадия (Stage): Эскиз (Concept)

План цокольного этажа.

Номер проекта	0001
Дата	29.04.2021
Чертил	Сидорук О.
Проверил	

A101

Масштаб	1 : 50

5/10/2021 6:29:55 PM

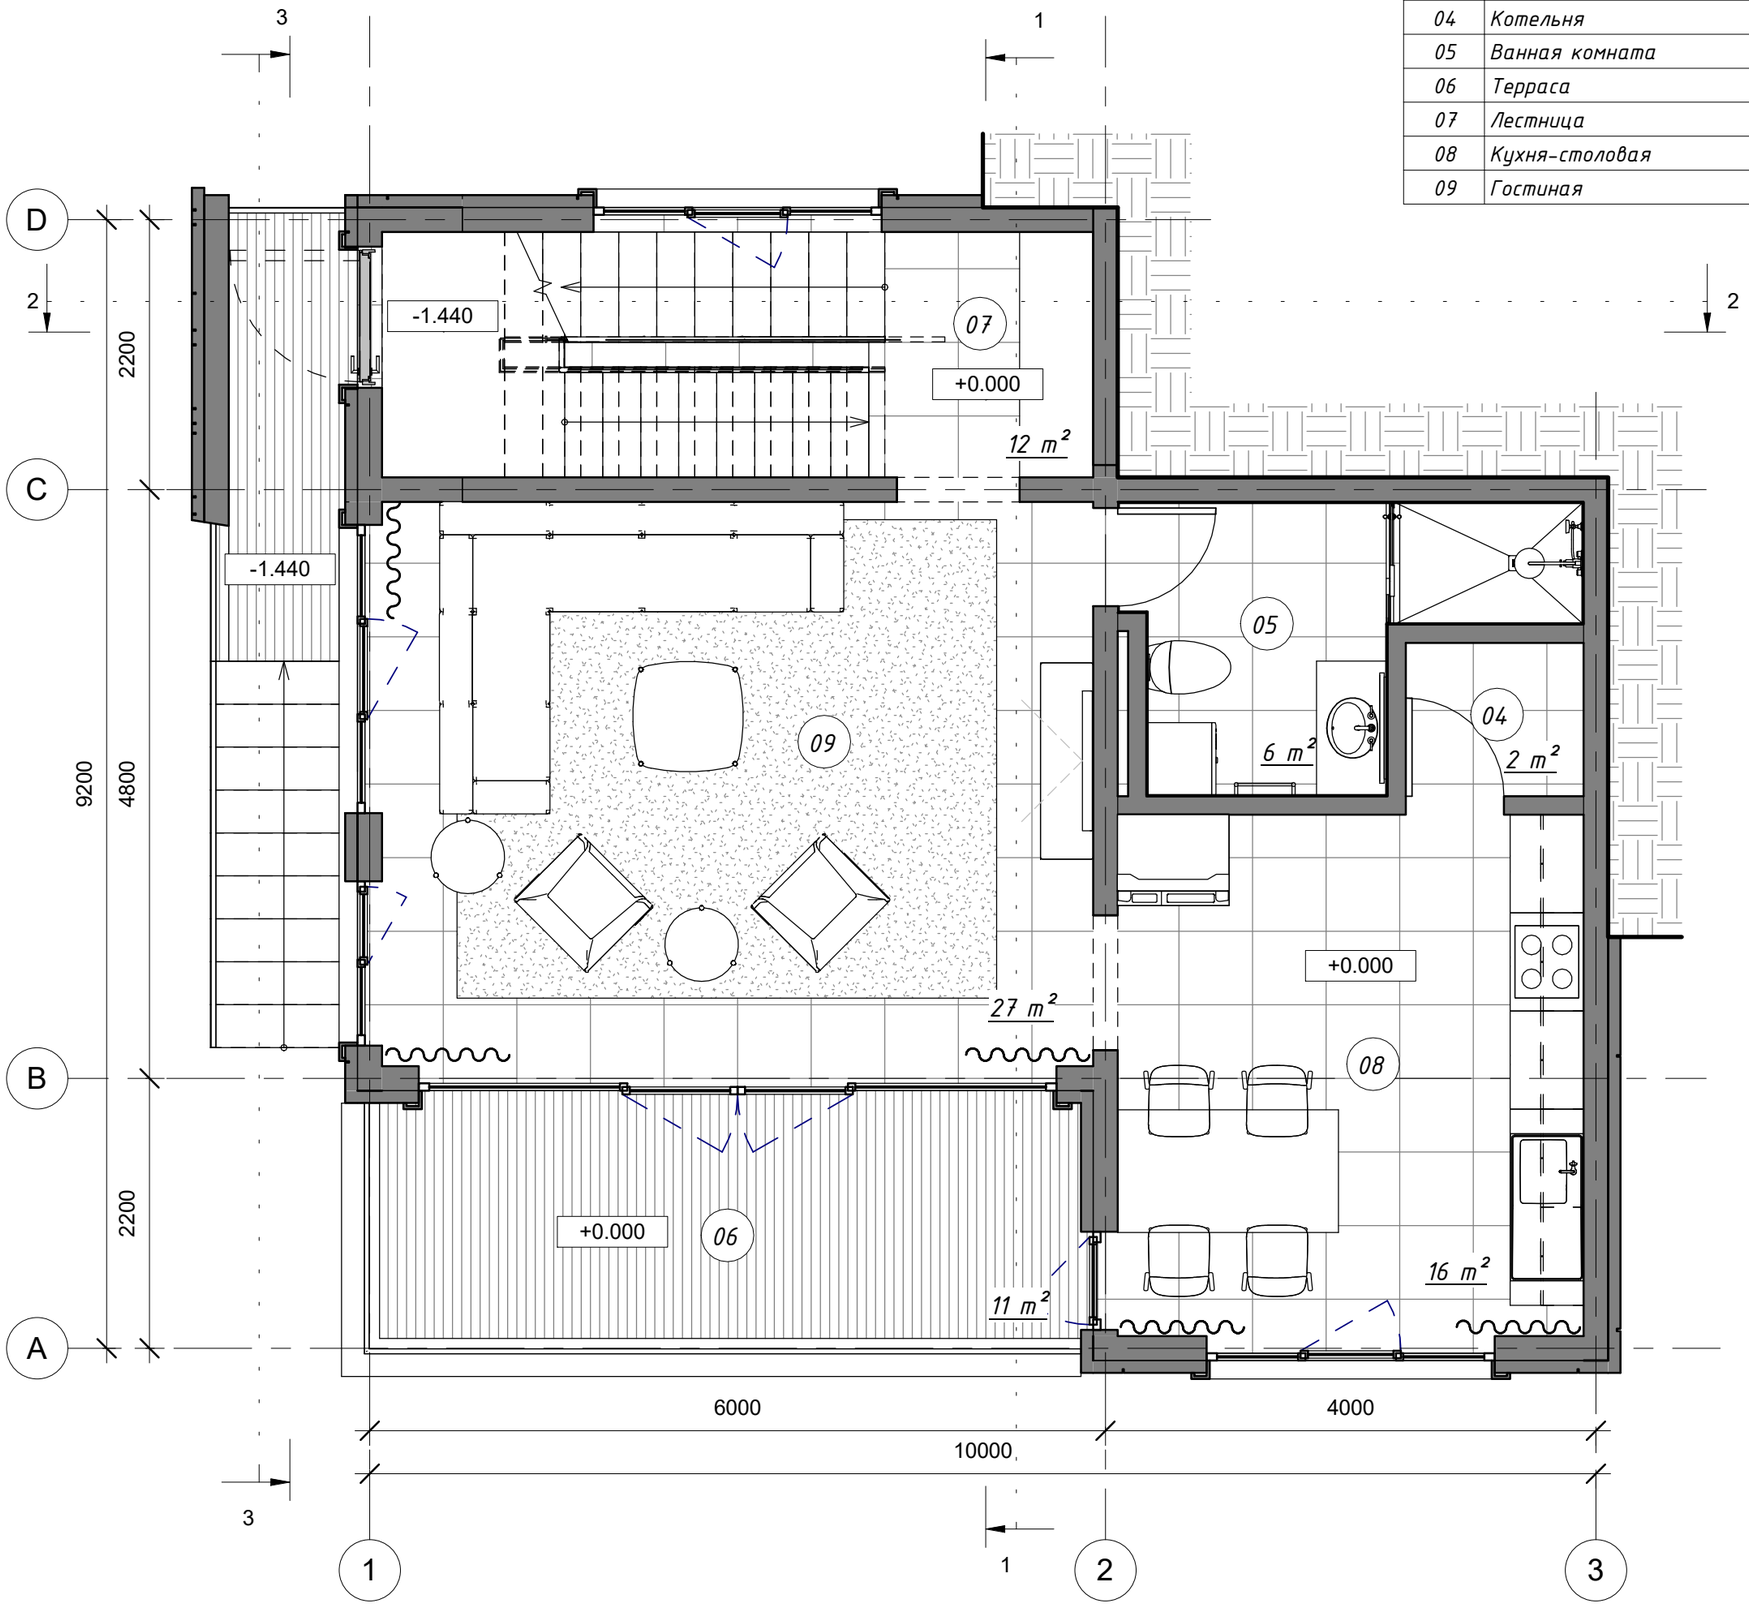

Экспликация помещений. Этаж 1		
№	Наименование	Площадь
04	Котельня	1.8 m²
05	Ванная комната	6.4 m²
06	Терраса	11.2 m²
07	Лестница	11.6 m²
08	Кухня-столовая	16.2 m²
09	Гостиная	26.7 m²
		73.9 m²

L.B.O.S.
DESIGN

№	Описание	Дата

Batumi Investment
SeaView Garden Villa. №3

Стадия (Stage): Эскиз (Concept)

План 1-го этажа.

Номер проекта	0001
Дата	29.04.2021
Чертил	Сидорук О.
Проверил	

A102

Масштаб	1 : 50

5/10/2021 6:29:58 PM

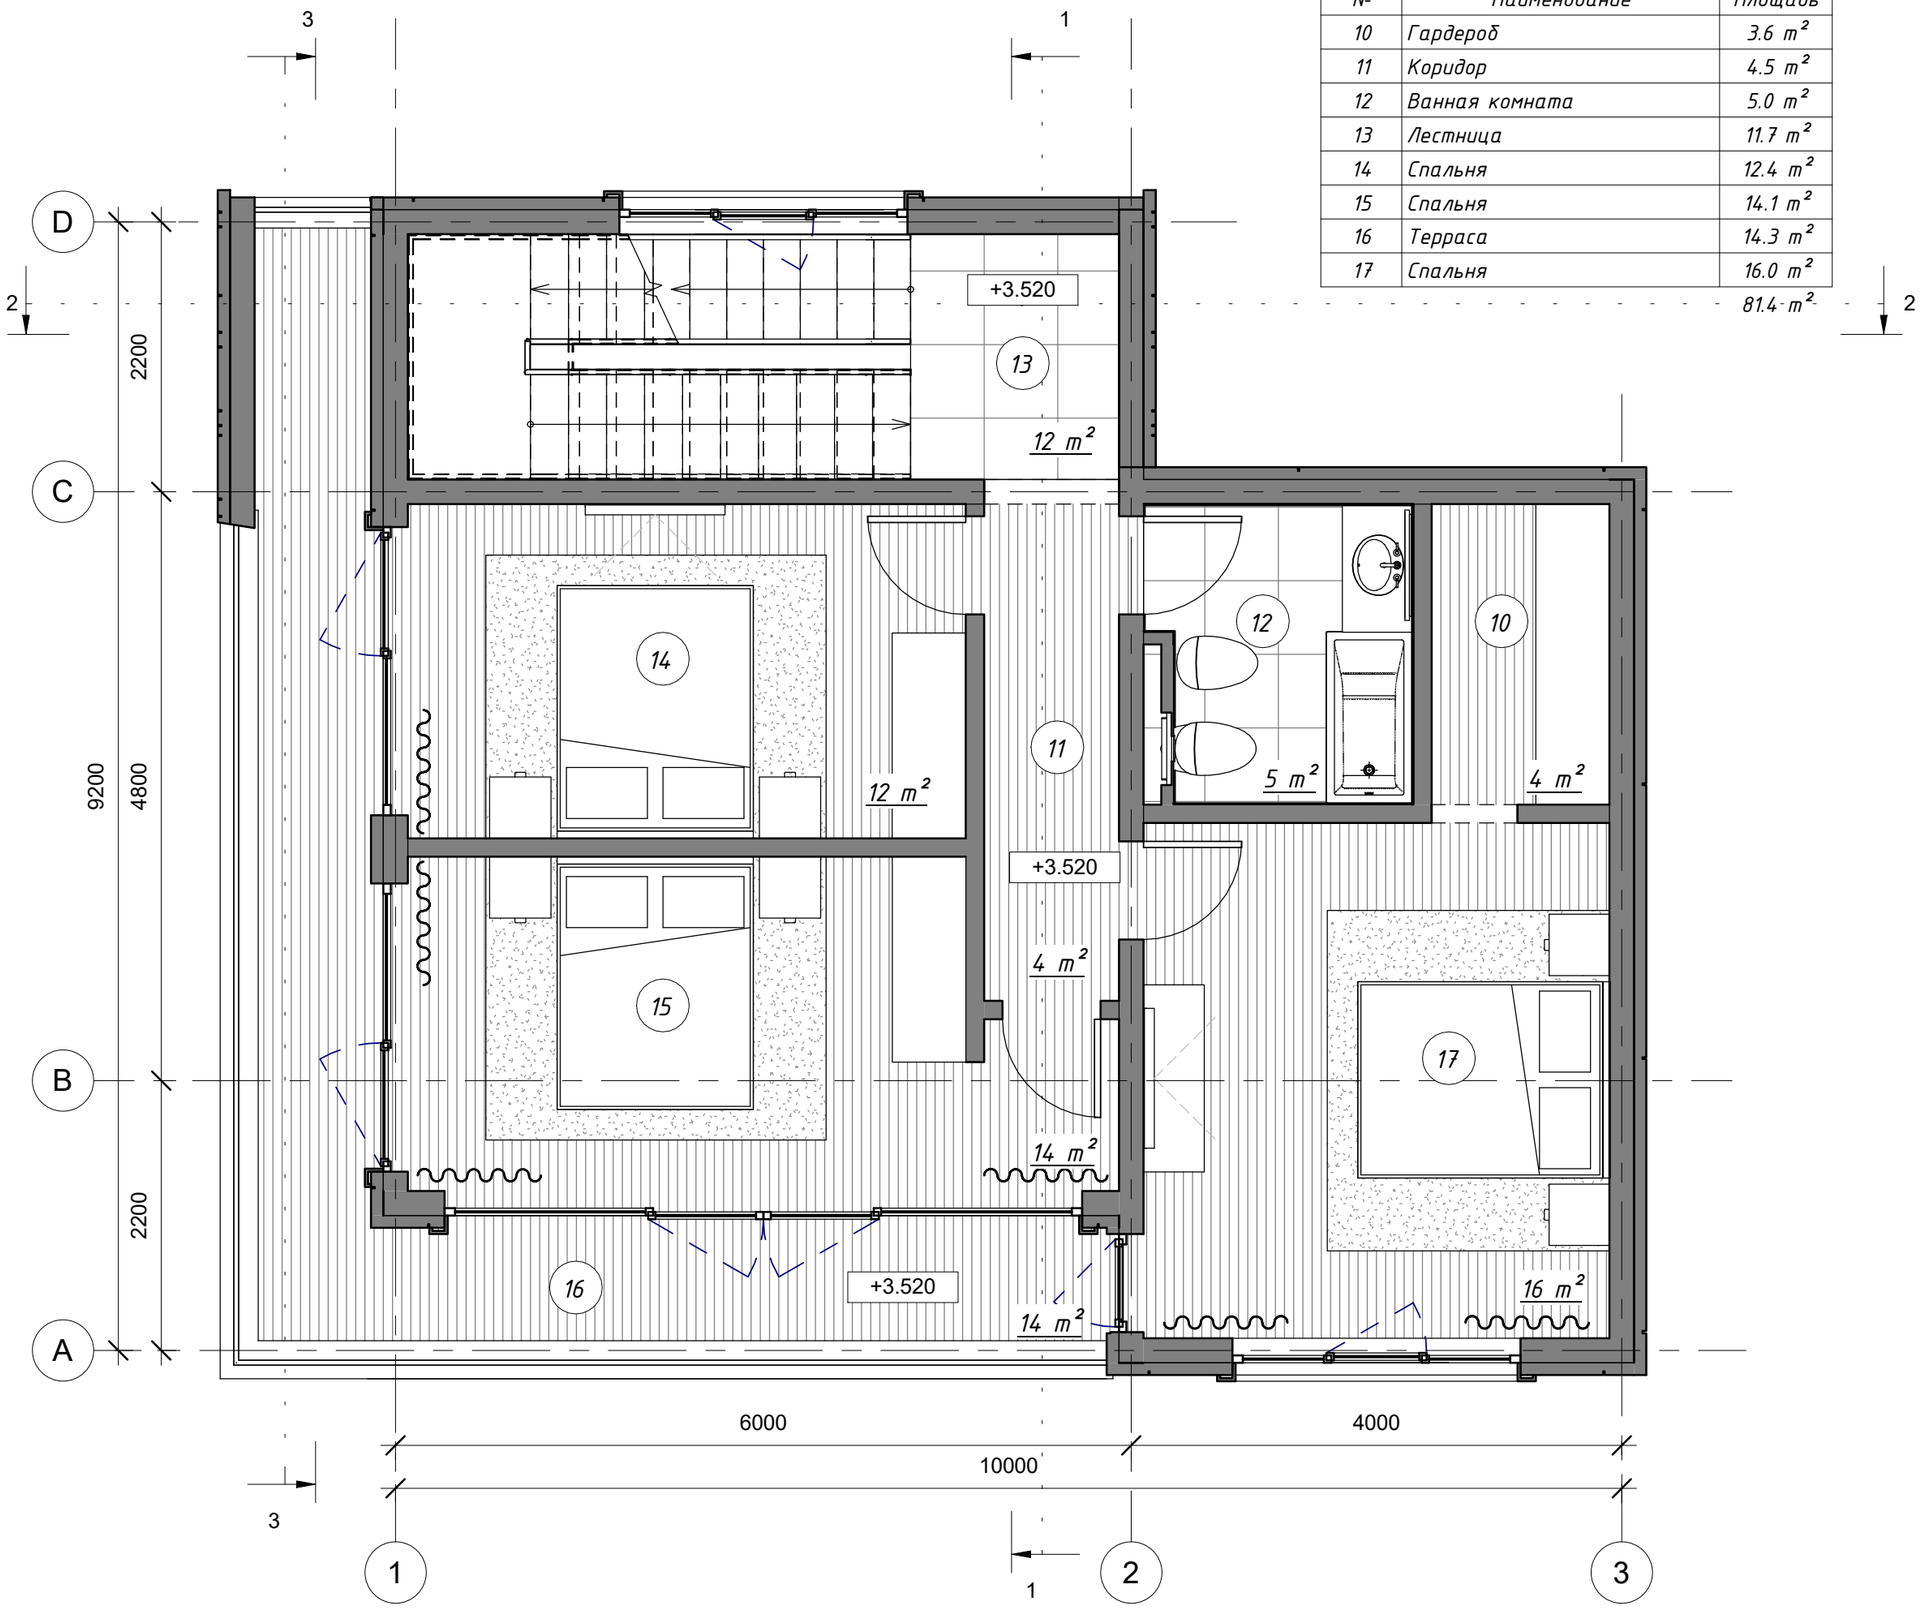

Экспликация помещений. Этаж 2		
№	Наименование	Площадь
10	Гардероб	3.6 m²
11	Коридор	4.5 m²
12	Ванная комната	5.0 m²
13	Лестница	11.7 m²
14	Спальня	12.4 m²
15	Спальня	14.1 m²
16	Терраса	14.3 m²
17	Спальня	16.0 m²
		81.4 m²

L.B.O.S.
DESIGN

№	Описание	Дата

Batumi Investment
SeaView Garden Villa. №3

Стадия (Stage): Эскиз (Concept)

План 2-го этажа.

Номер проекта	0001
Дата	29.04.2021
Чертил	Сидорук О.
Проверил	

A103

Масштаб	1 : 50

5/10/2021 6:29:59 PM

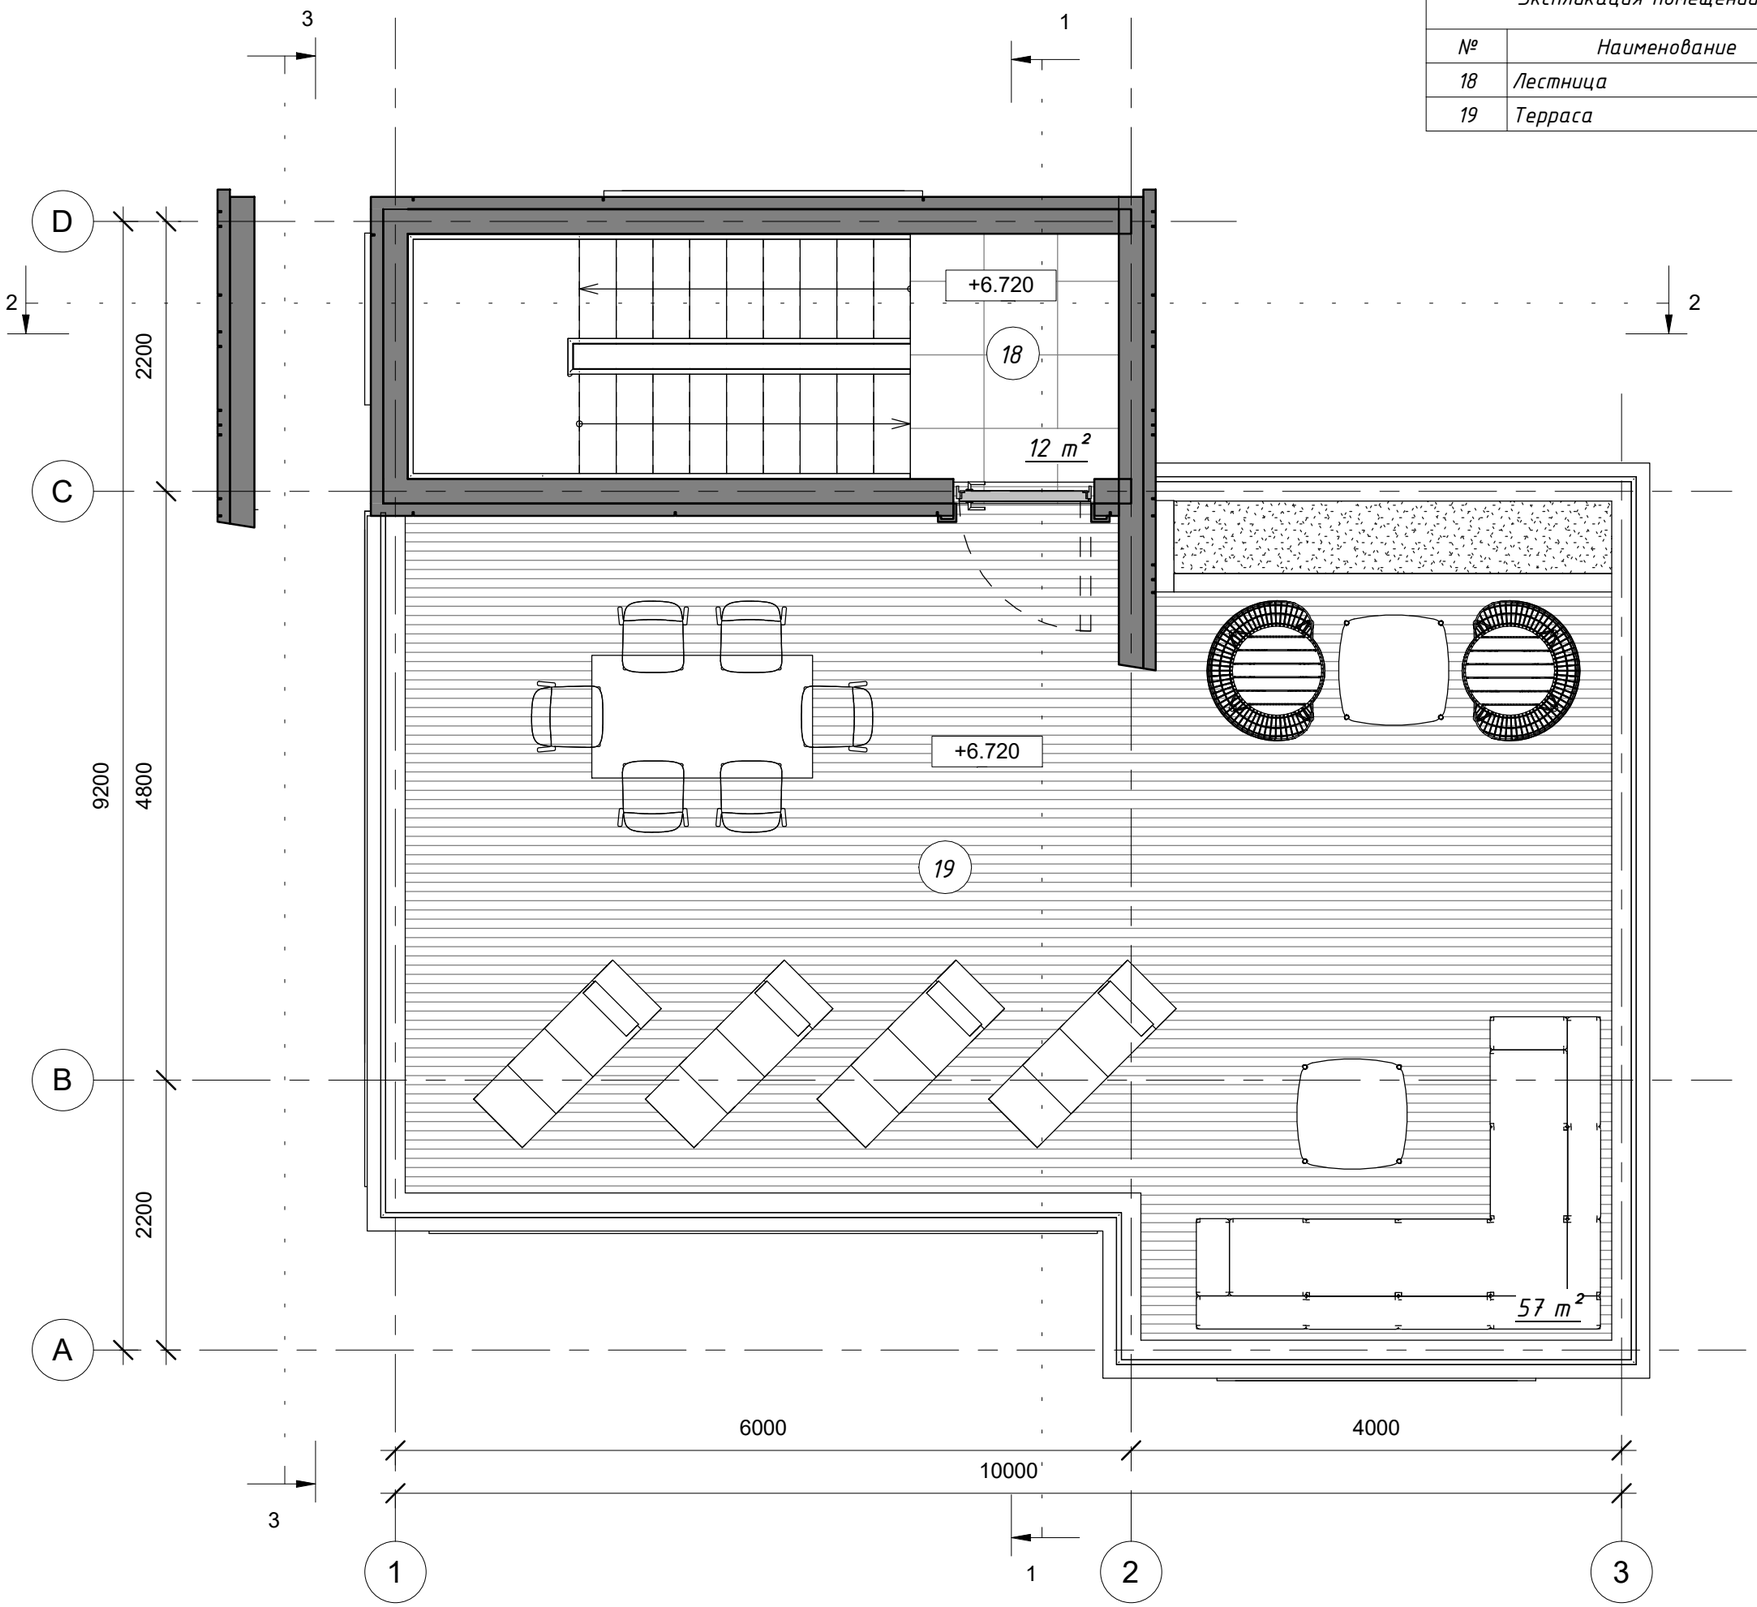

Экспликация помещений. Этаж 3		
№	Наименование	Площадь
18	Лестница	11.6 m²
19	Терраса	57.0 m²
		68.6 m²

L.B.O.S.
DESIGN

№	Описание	Дата

Batumi Investment
SeaView Garden Villa. №3

Стадия (Stage): Эскиз (Concept)

План 3-го этажа.

Номер проекта	0001
Дата	29.04.2021
Чертил	Сидорук О.
Проверил	

A104

Масштаб	1 : 50

5/10/2021 6:30:25 PM

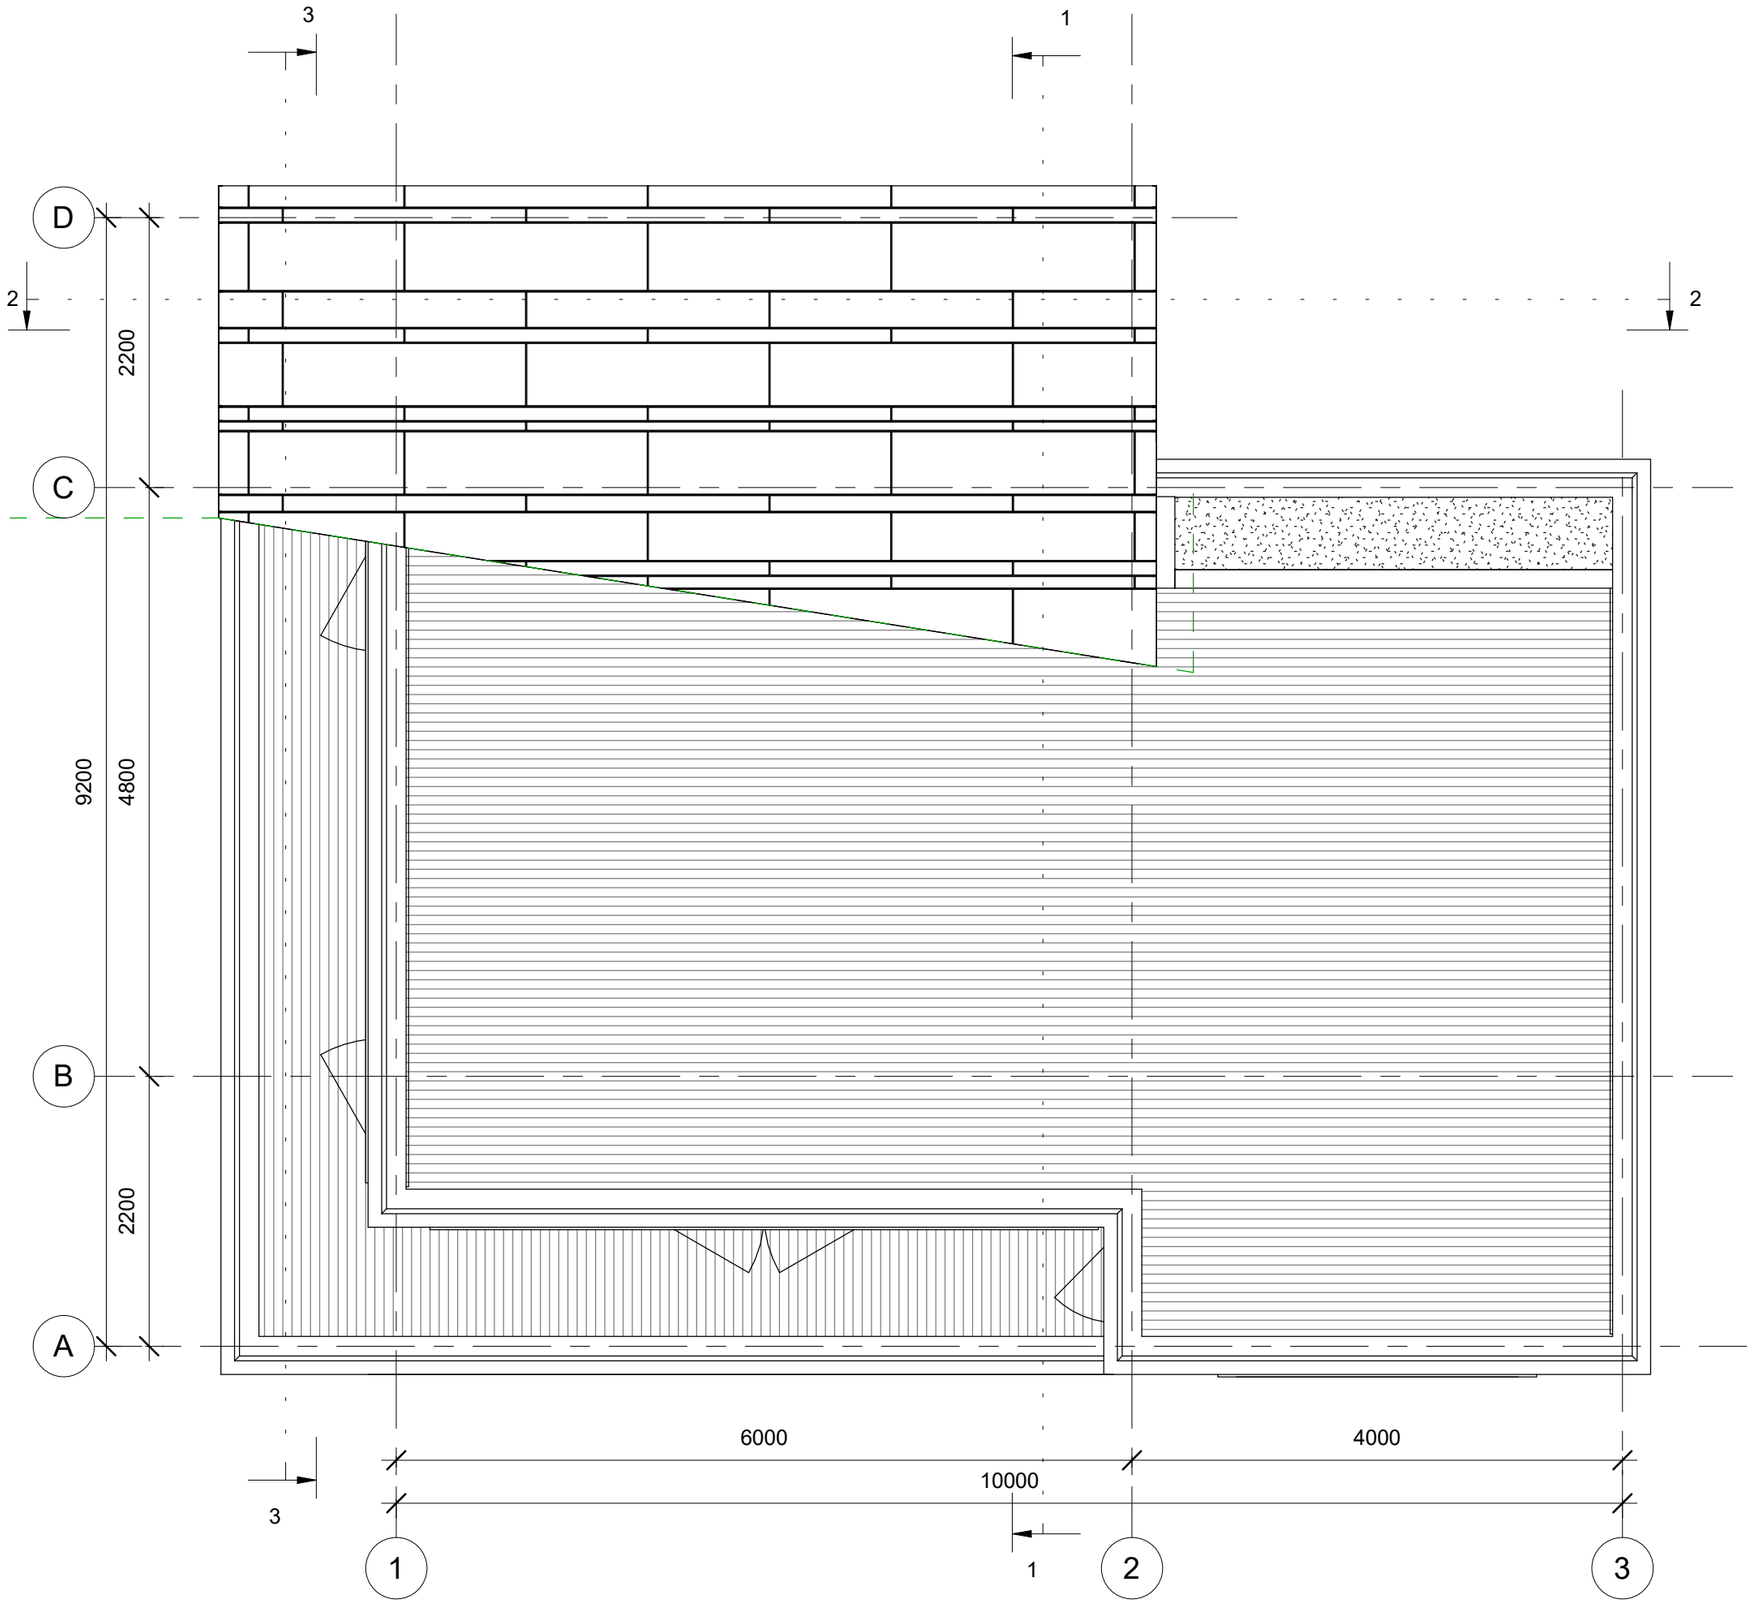

L.B.O.S.
DESIGN

№	Описание	Дата

Batumi Investment
SeaView Garden Villa. №3

Стадия (Stage): Эскиз (Concept)

План кровли.

Номер проекта	0001
Дата	29.04.2021
Чертил	Сидорук О.
Проверил	

A105

Масштаб	1 : 50

5/10/2021 6:30:27 PM

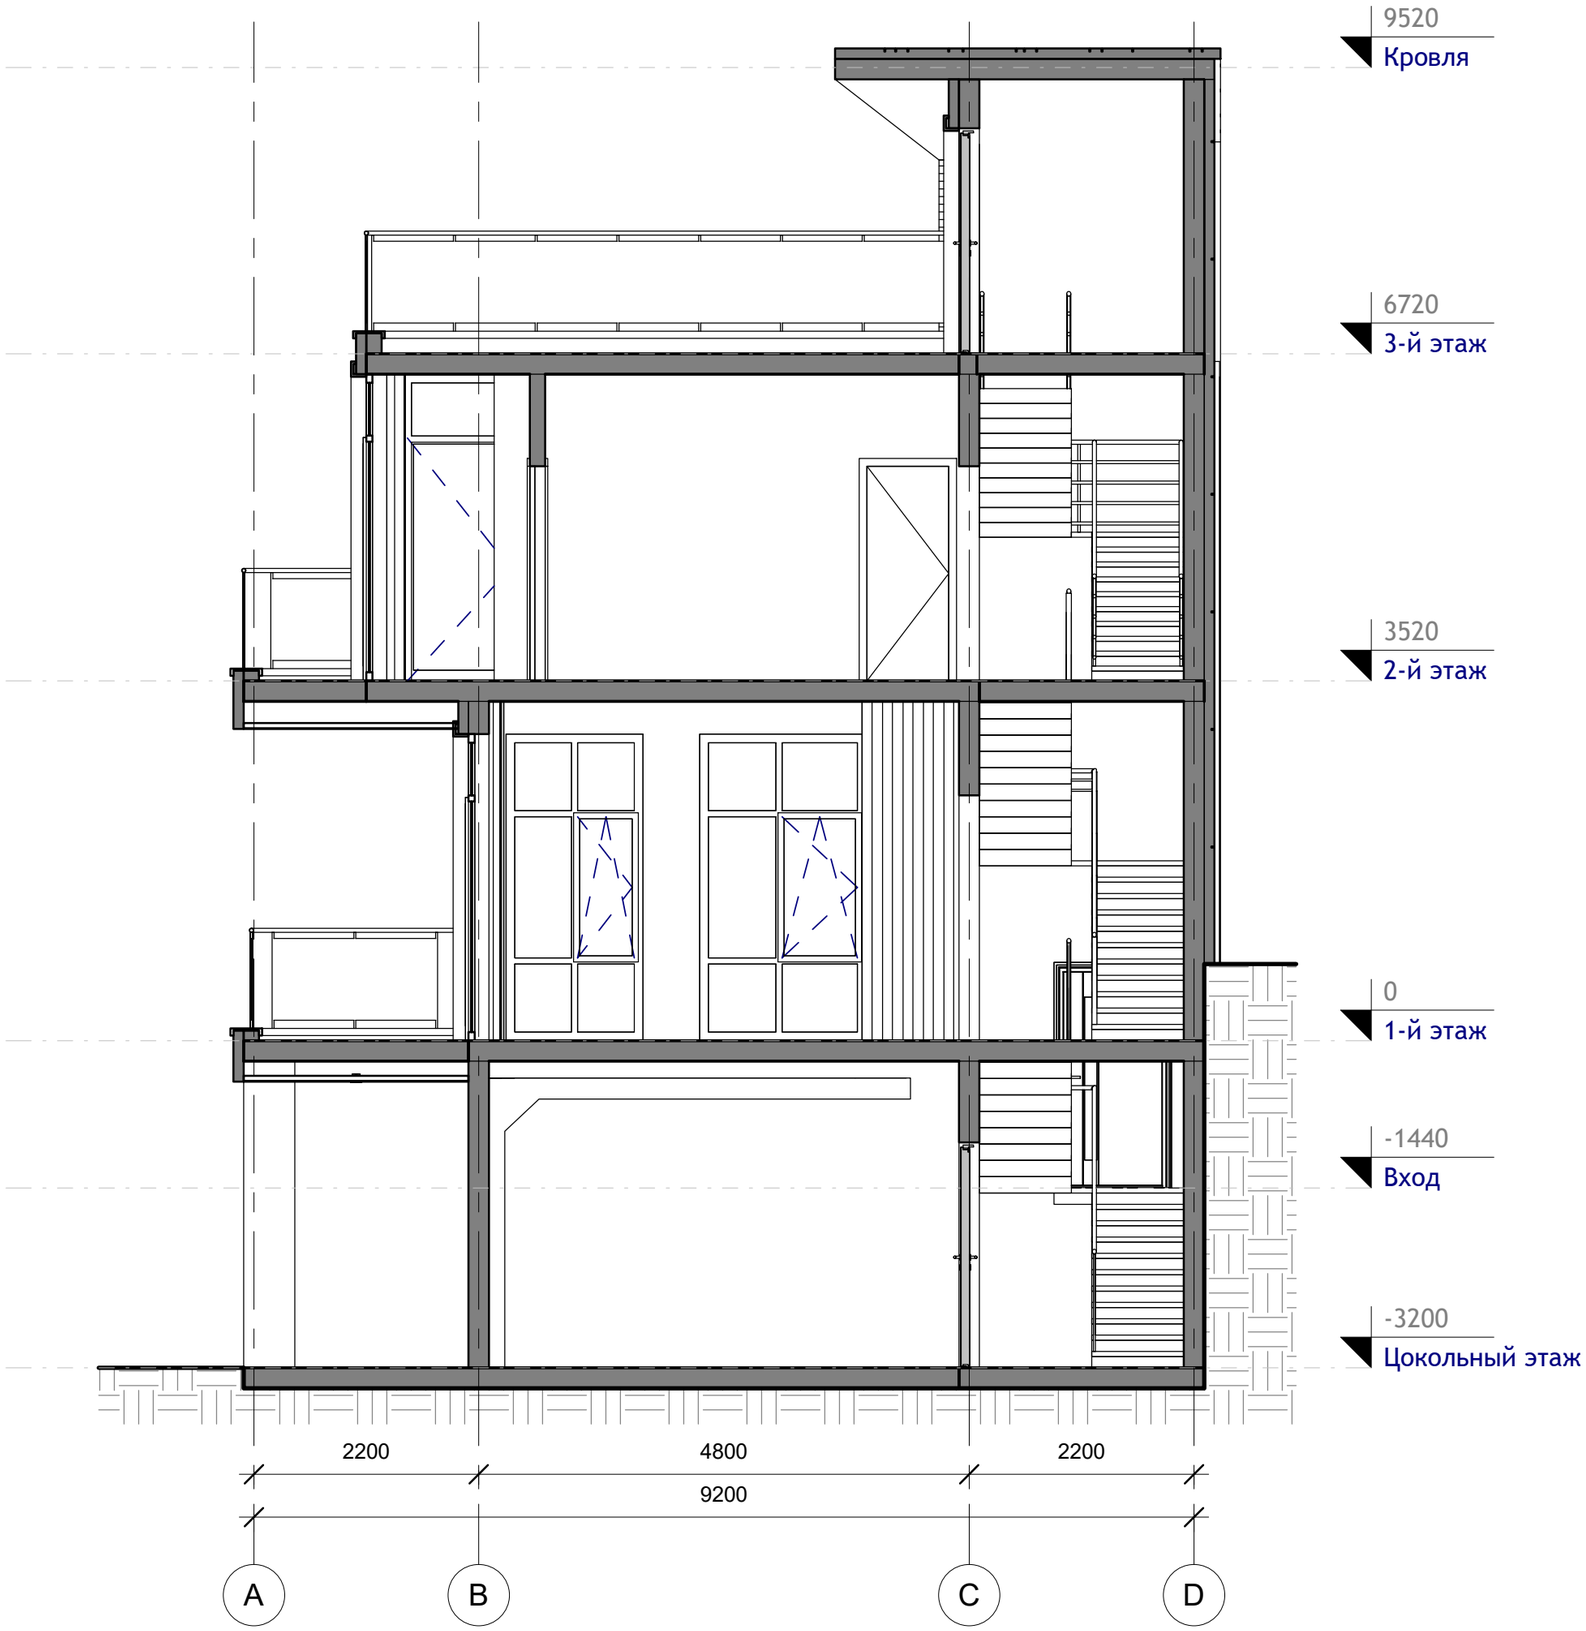

L.B.O.S.
DESIGN

№	Описание	Дата

Batumi Investment
SeaView Garden Villa. №3

Стадия (Stage): Эскиз (Concept)

Разрез 1-1

Номер проекта	0001
Дата	29.04.2021
Чертил	Сидорук О.
Проверил	

A106

Масштаб	1 : 60

5/10/2021 6:30:28 PM

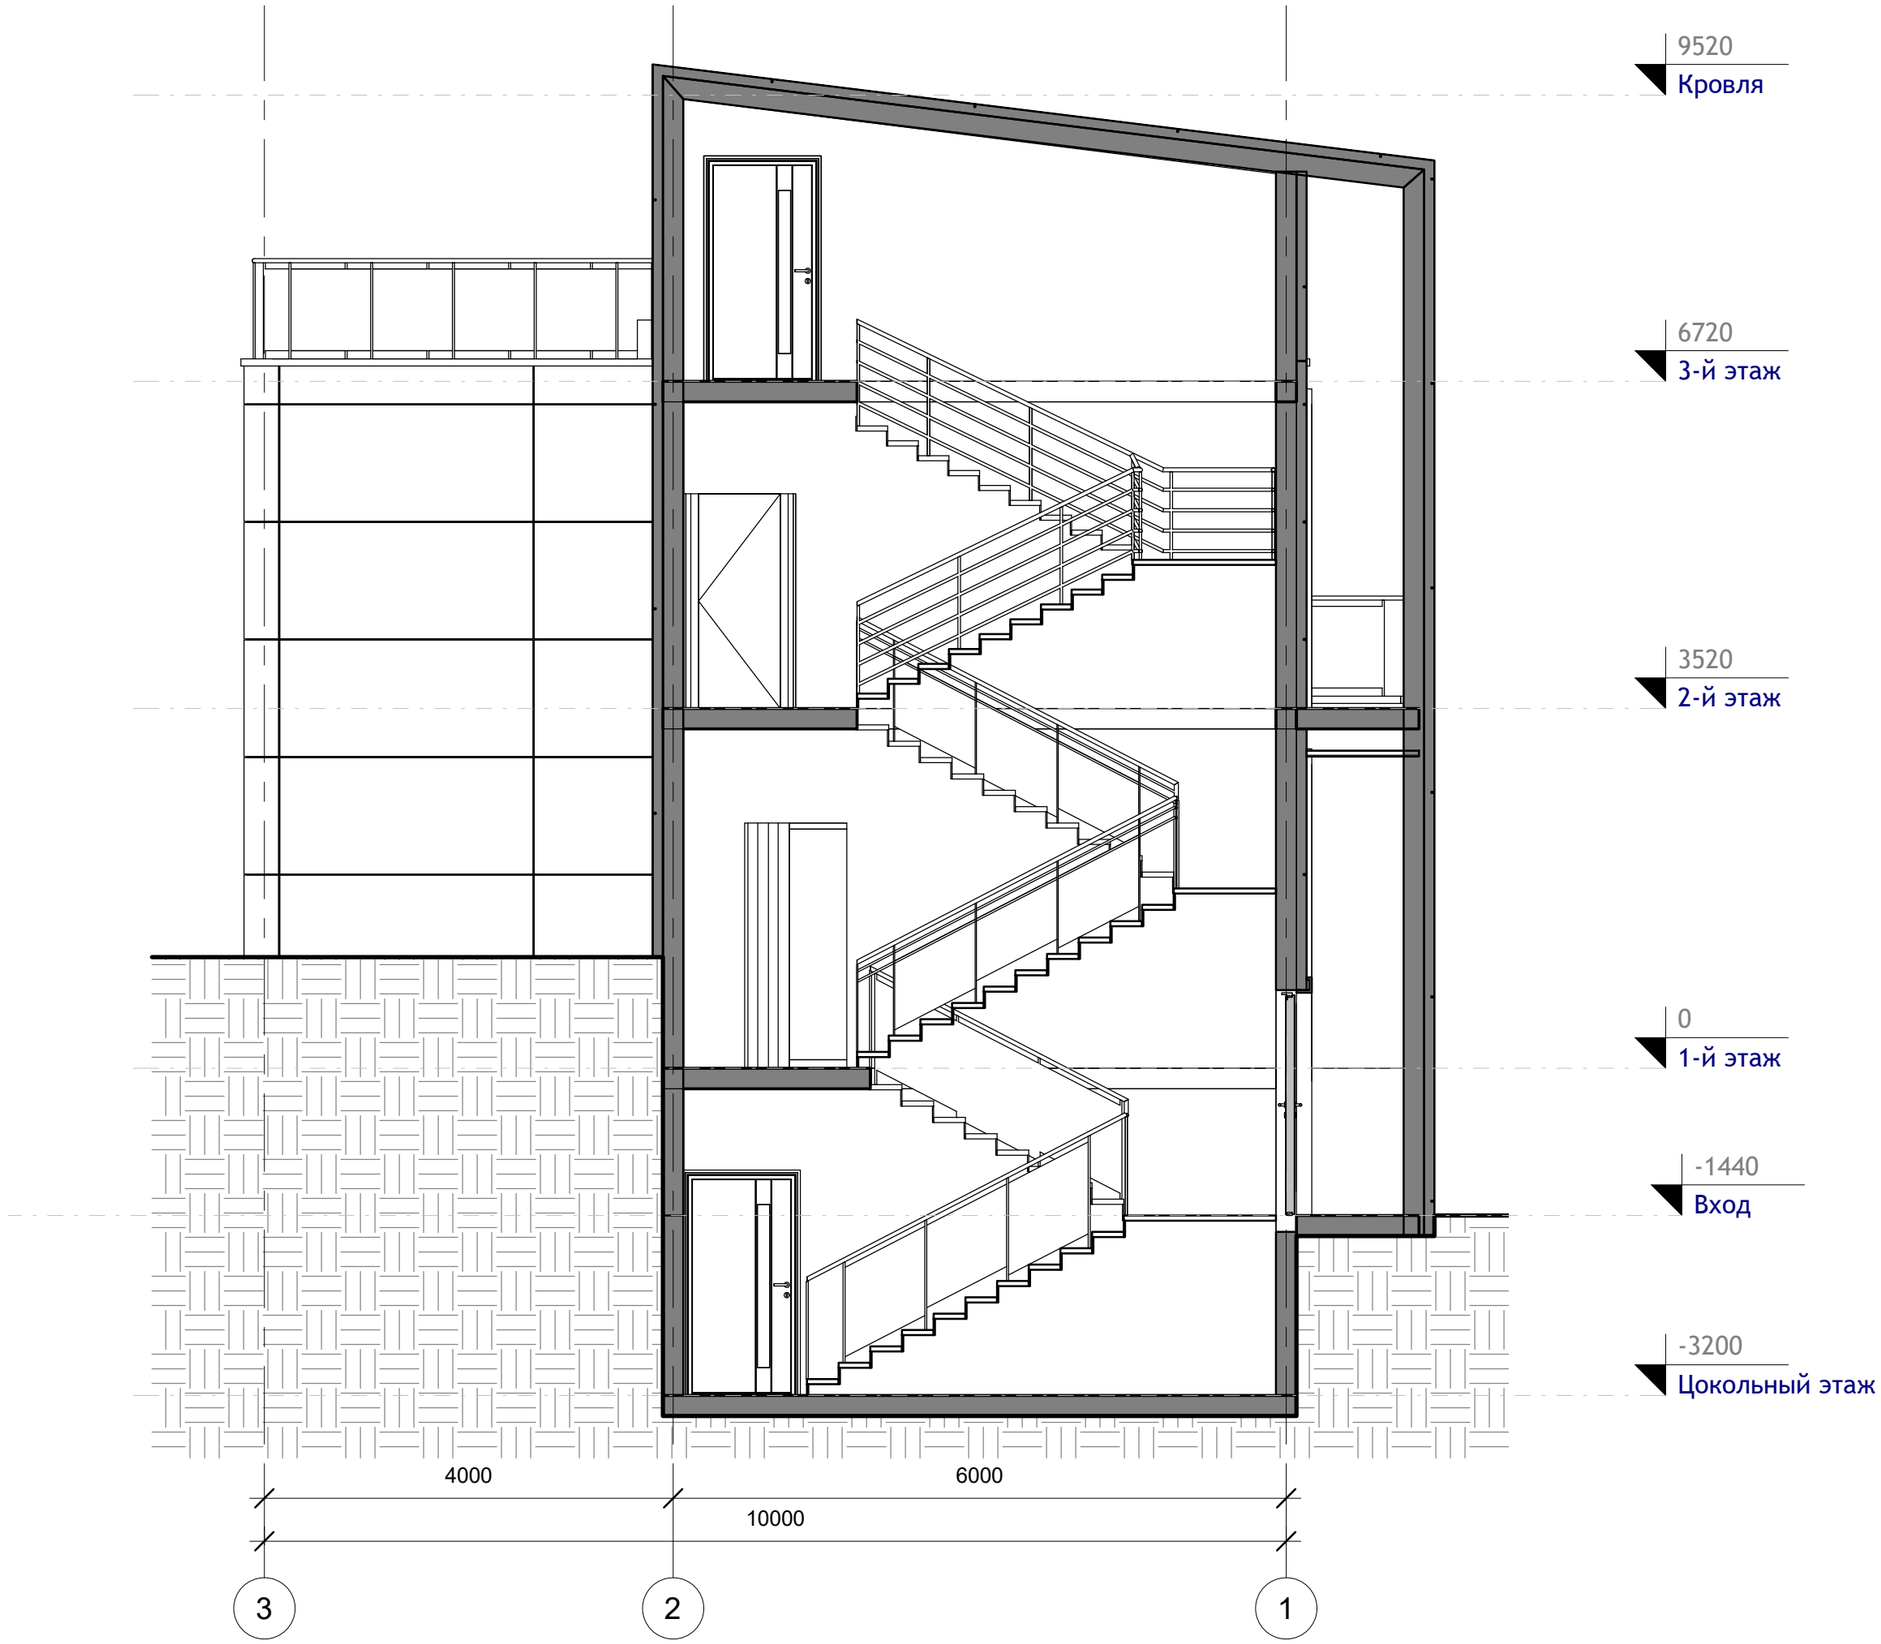

L.B.O.S.
DESIGN

№	Описание	Дата

Batumi Investment
SeaView Garden Villa. №3

Стадия (Stage): Эскиз (Concept)

Разрез 2-2

Номер проекта	0001
Дата	29.04.2021
Чертил	Сидорук О.
Проверил	

A107

Масштаб	1 : 60

5/10/2021 6:30:28 PM

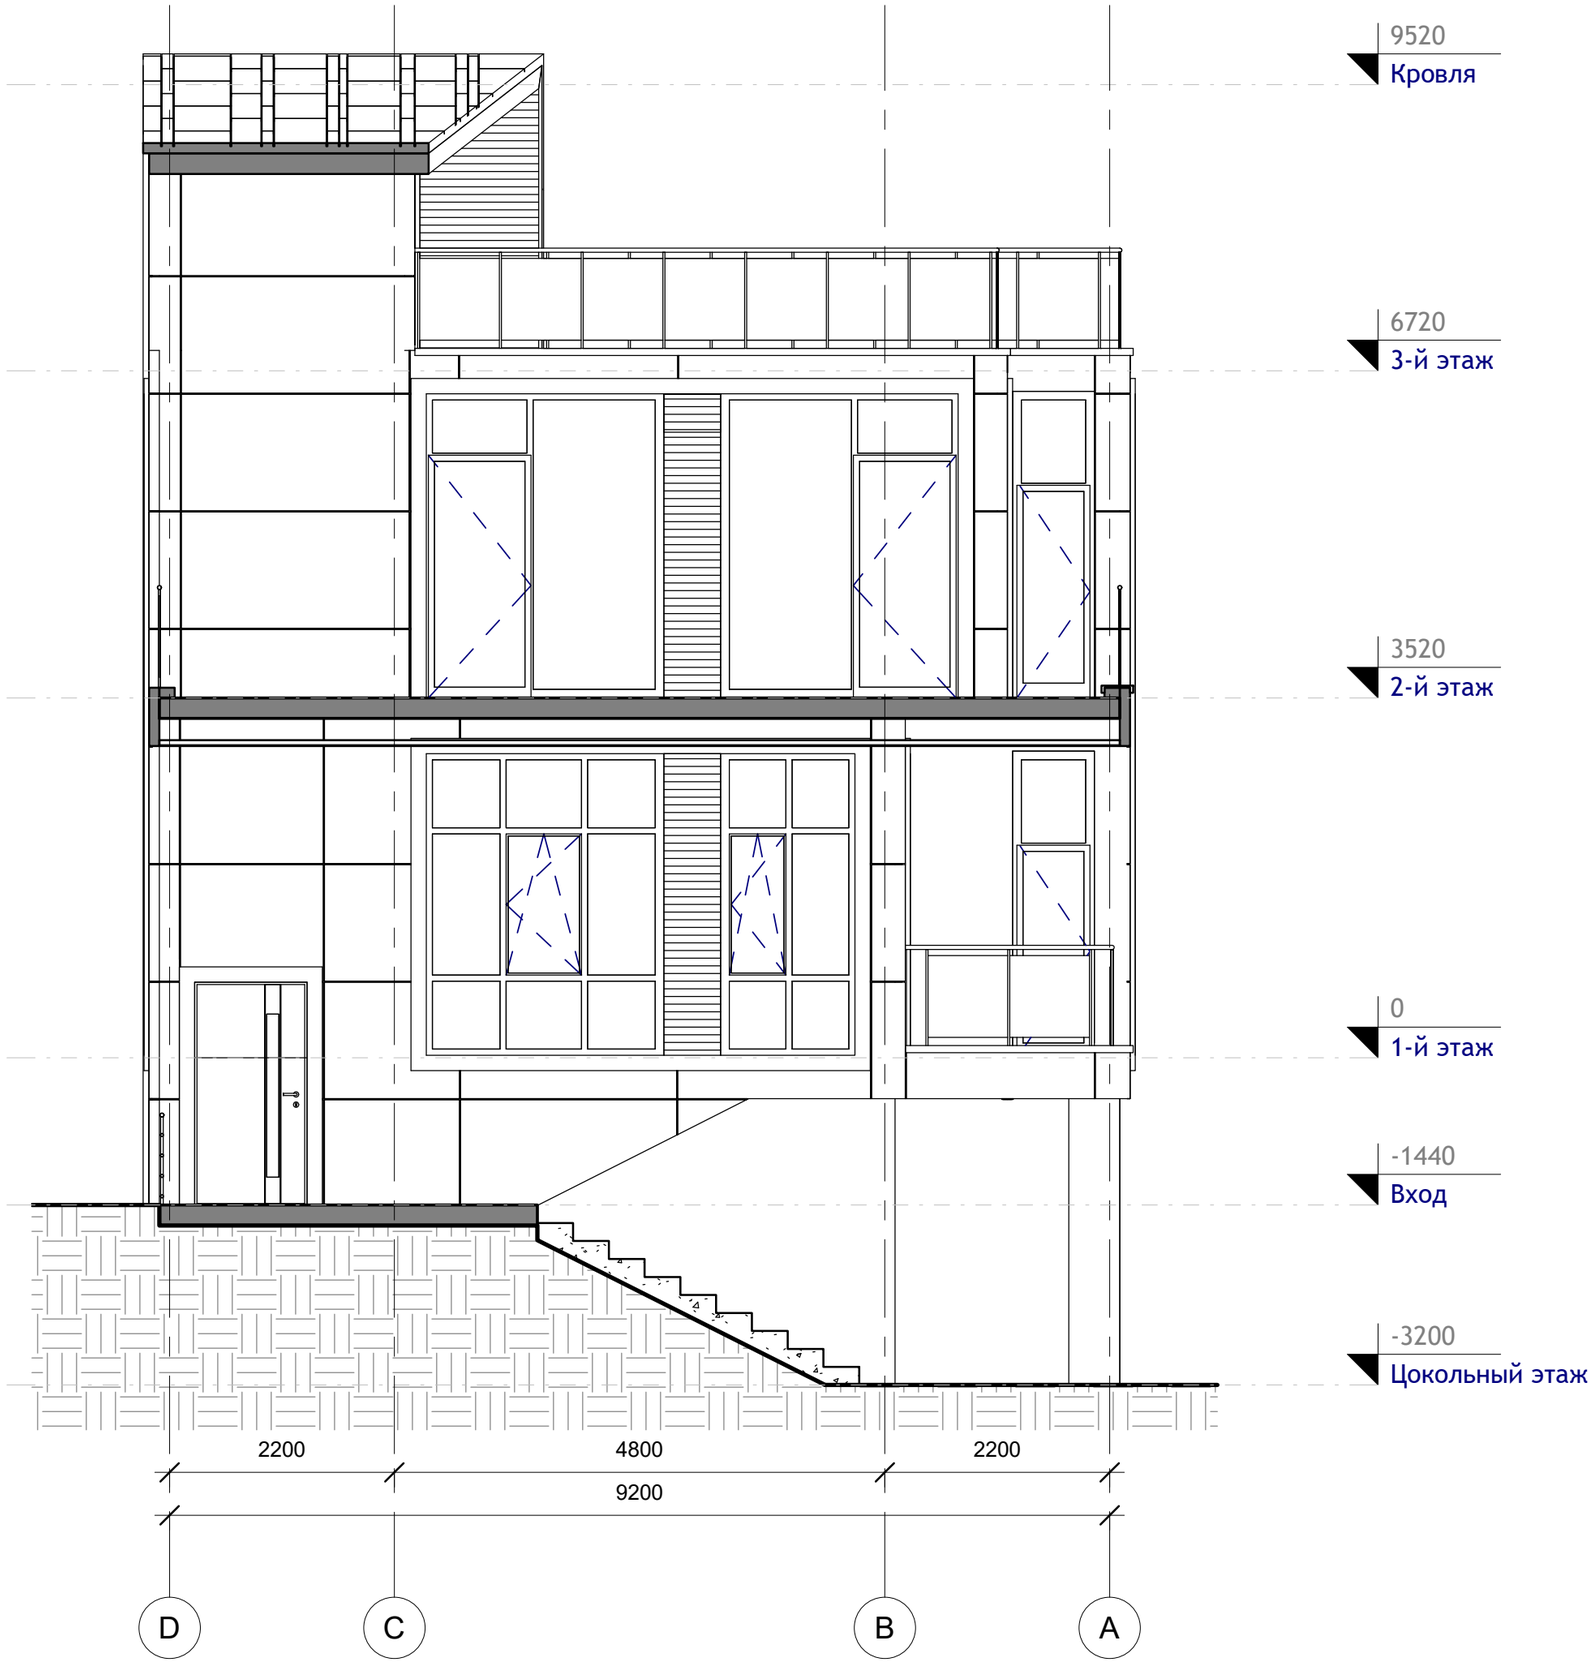

L.B.O.S.
DESIGN

№	Описание	Дата

Batumi Investment
SeaView Garden Villa. №3

Стадия (Stage): Эскиз (Concept)

Разрез 3-3

Номер проекта	0001
Дата	29.04.2021
Чертил	Сидорук О.
Проверил	

A108

Масштаб	1 : 60

5/10/2021 6:30:29 PM

L.B.O.S.
DESIGN

№	Описание	Дата

Batumi Investment
SeaView Garden Villa. №3

Стадия (Stage): Эскиз (Concept)

Фасад в осях 1-3

Номер проекта	0001
Дата	29.04.2021
Чертил	Сидорук О.
Проверил	

A109

Масштаб	1 : 60

5/10/2021 6:30:38 PM

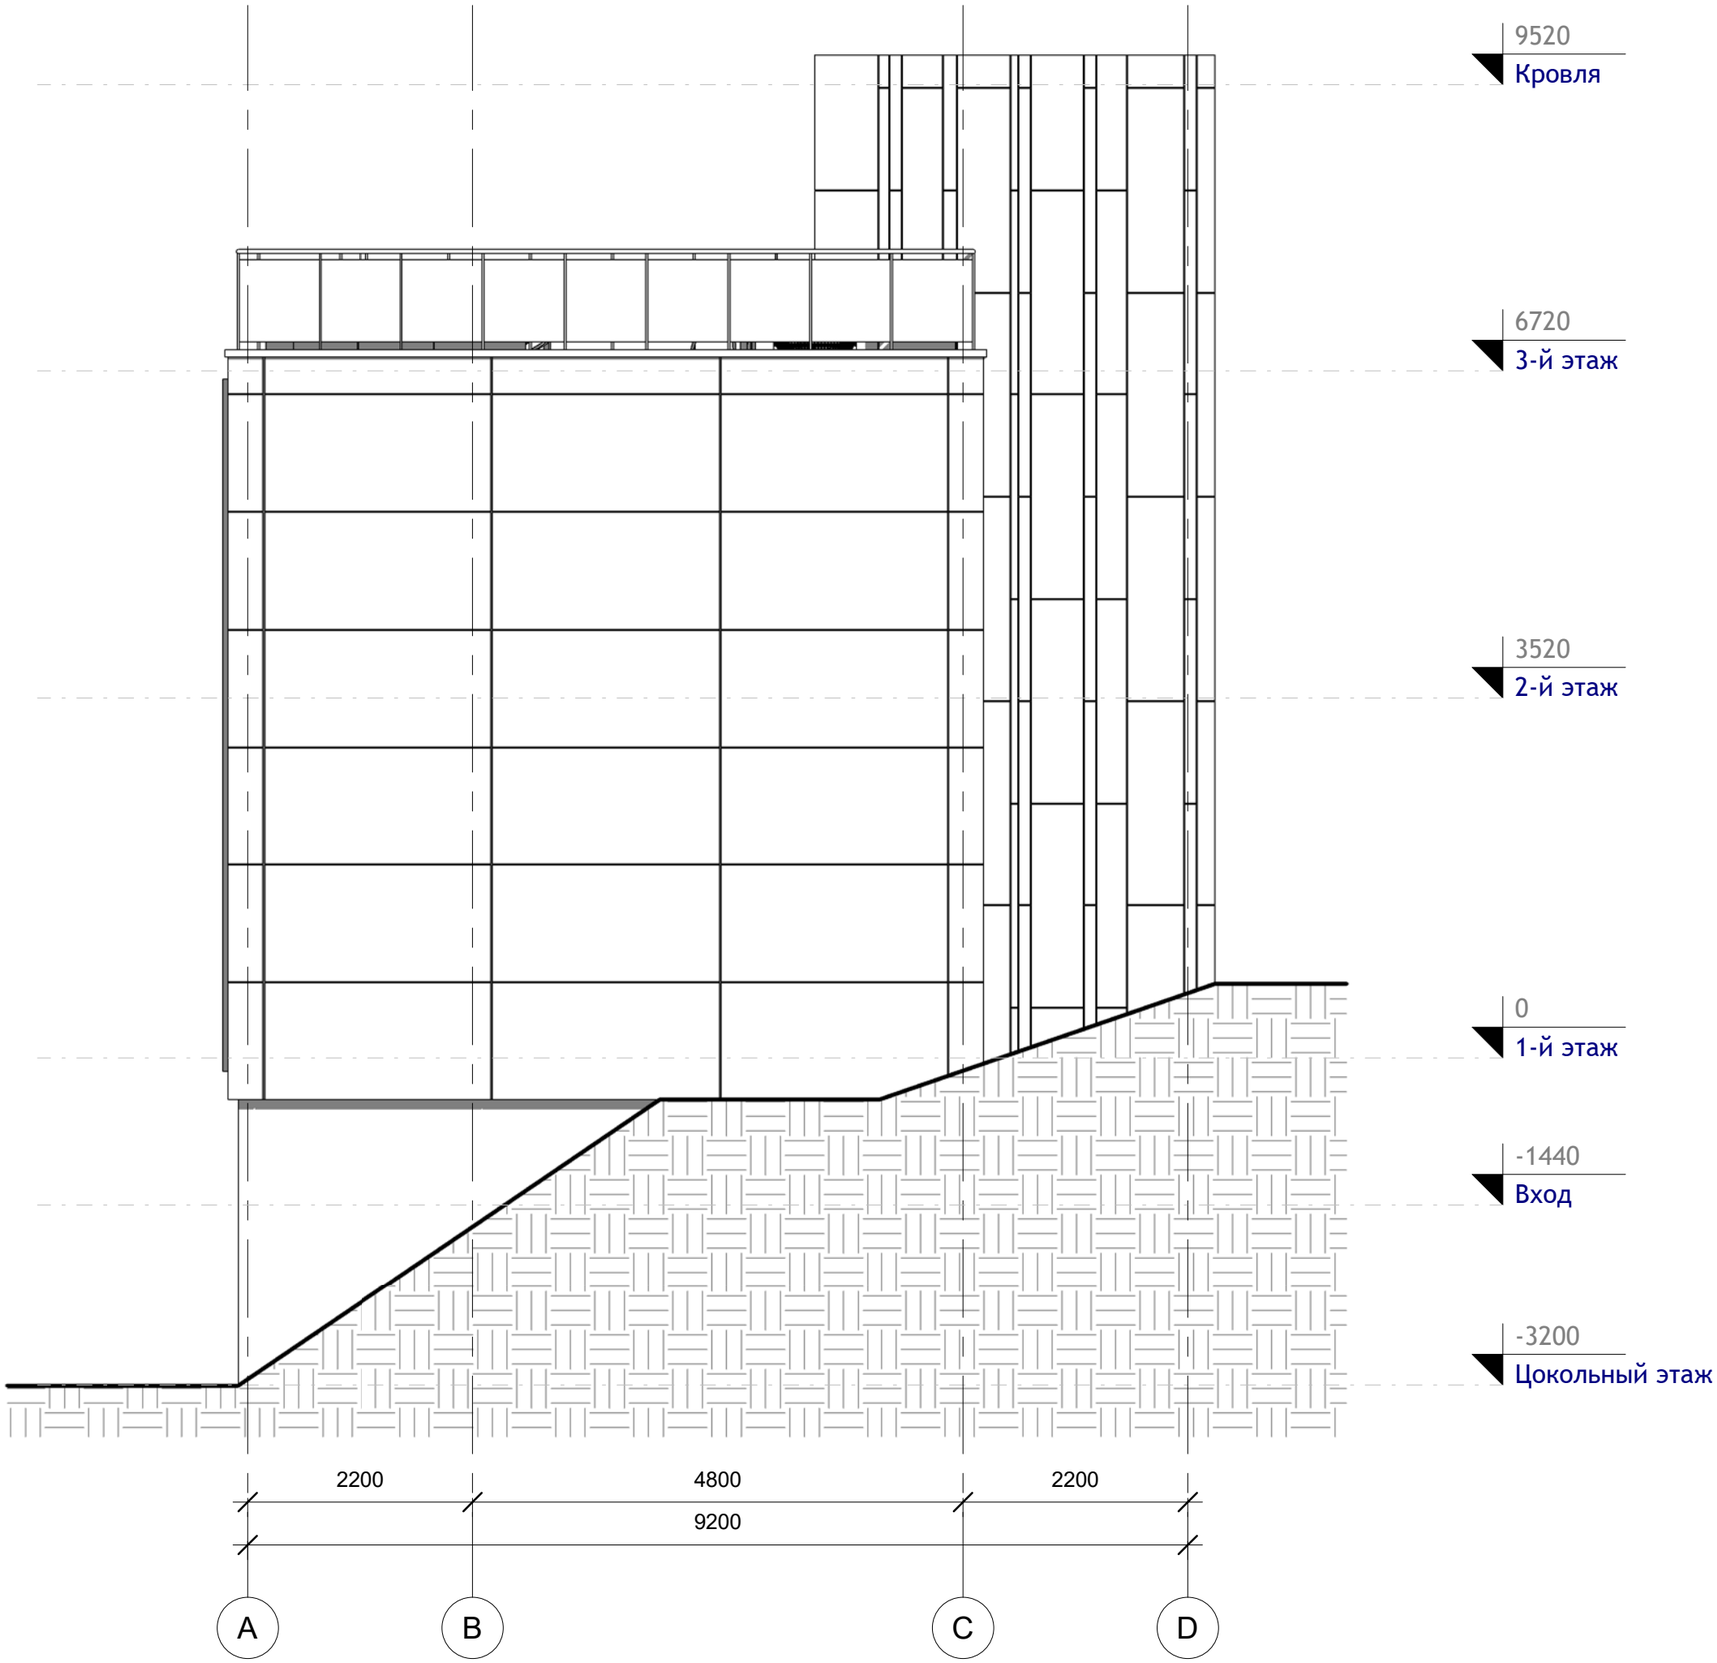

L.B.O.S.
DESIGN

№	Описание	Дата

Batumi Investment
SeaView Garden Villa. №3

Стадия (Stage): Эскиз (Concept)

Фасад в осях A-D

Номер проекта	0001
Дата	29.04.2021
Чертил	Сидорук О.
Проверил	

A110

Масштаб	1 : 60

5/10/2021 6:30:46 PM

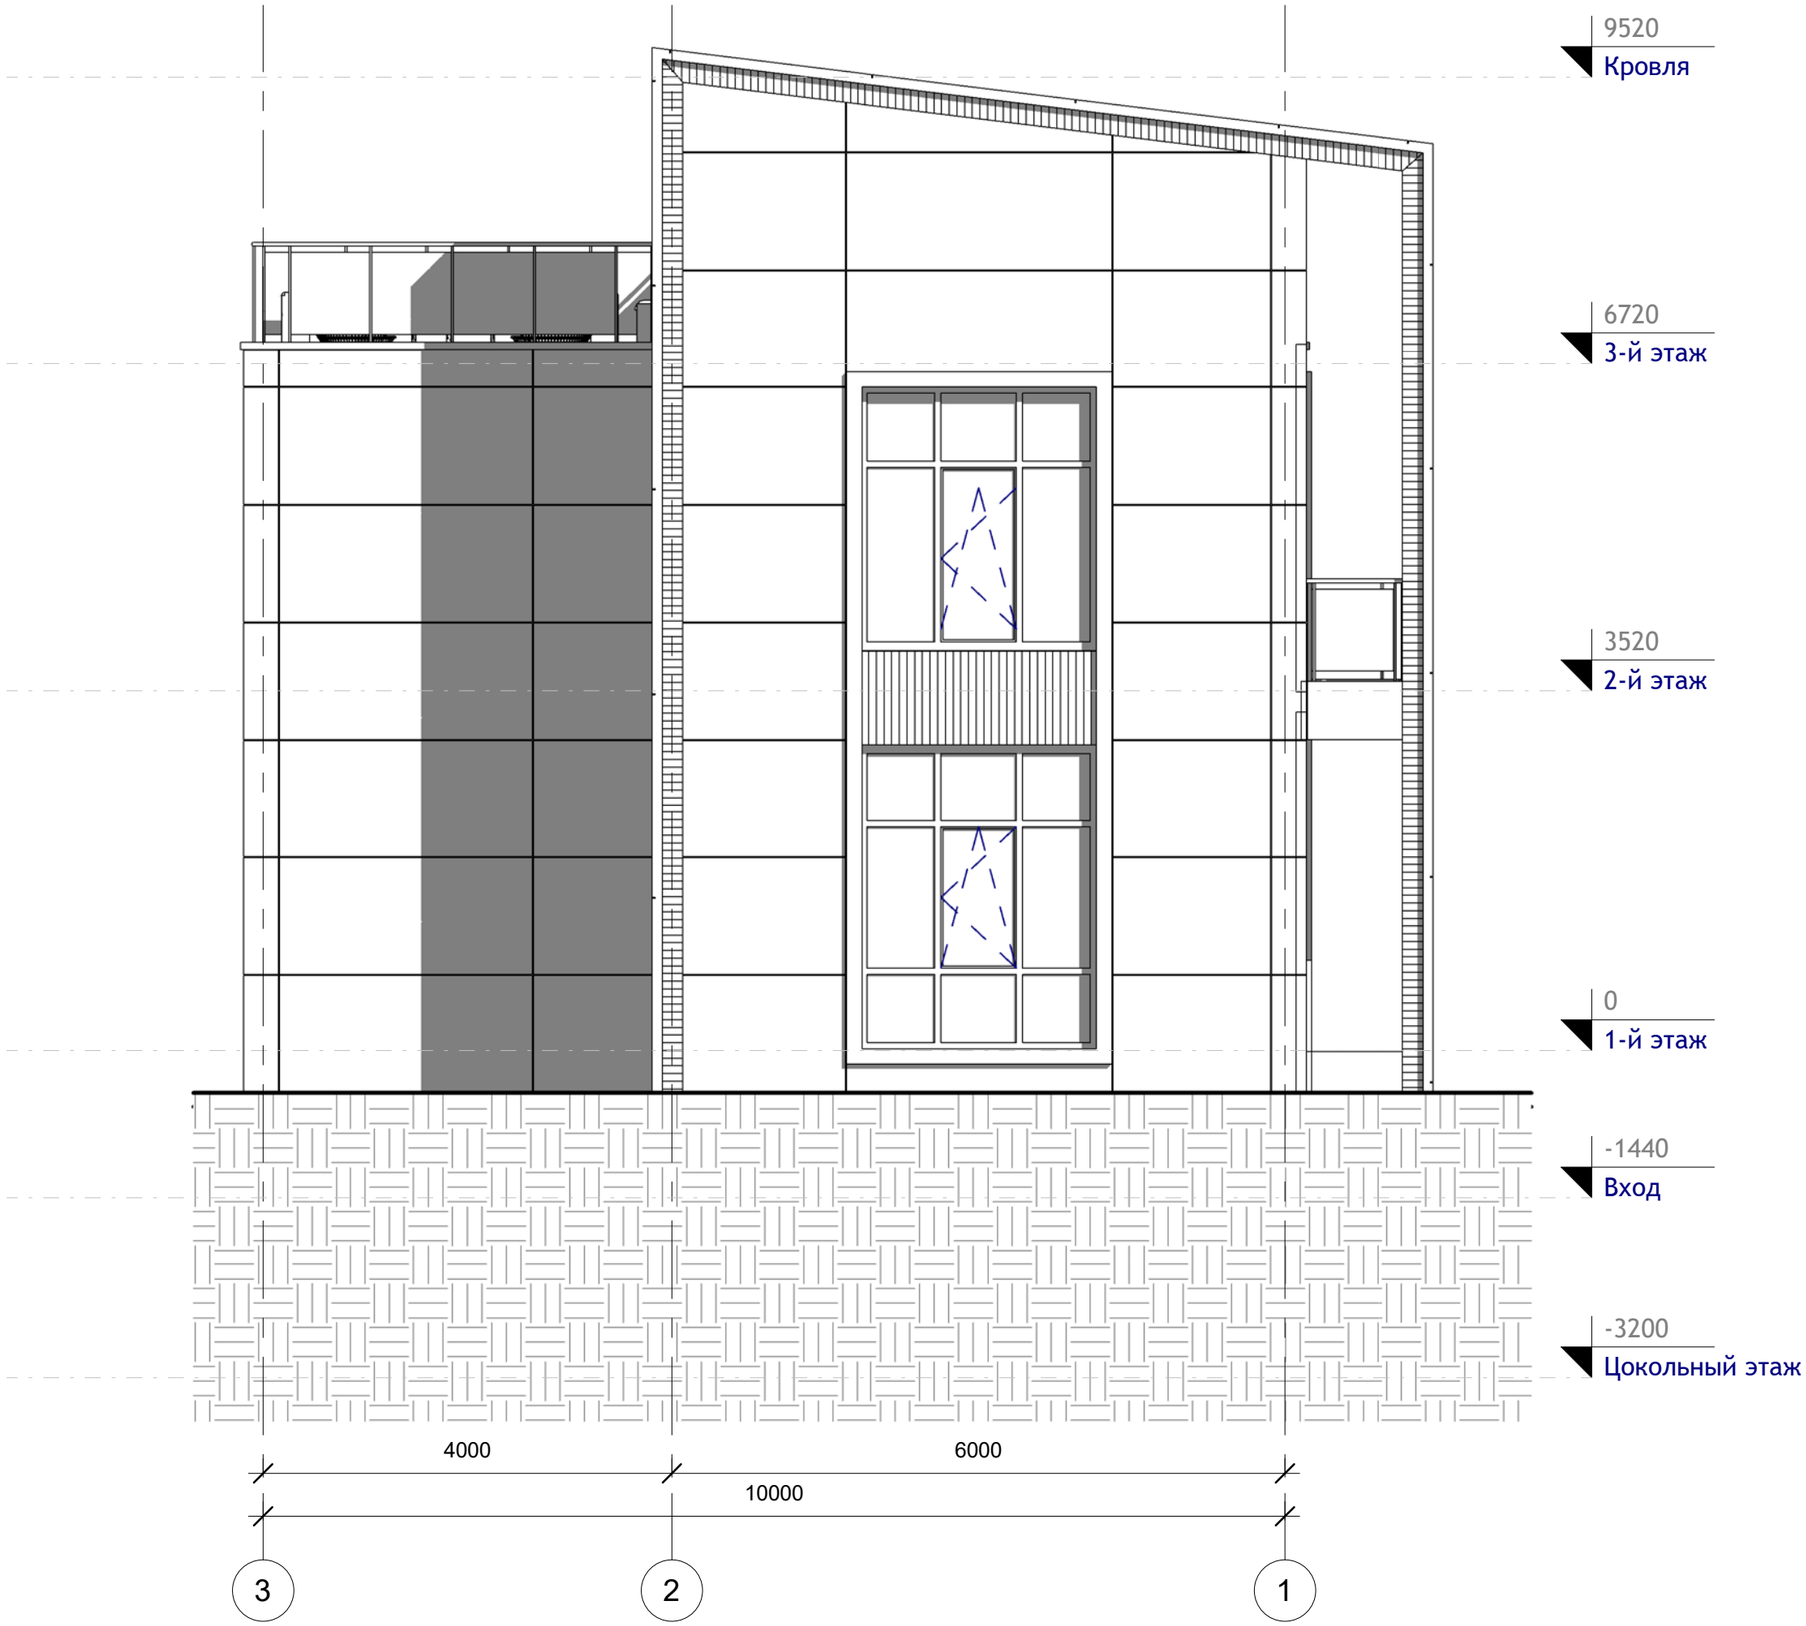

L.B.O.S.
DESIGN

№	Описание	Дата

Batumi Investment
SeaView Garden Villa. №3

Стадия (Stage): Эскиз (Concept)

Фасад в осях 3-1

Номер проекта	0001
Дата	29.04.2021
Чертил	Сидорук О.
Проверил	

A111

Масштаб	1 : 60

5/10/2021 6:30:53 PM

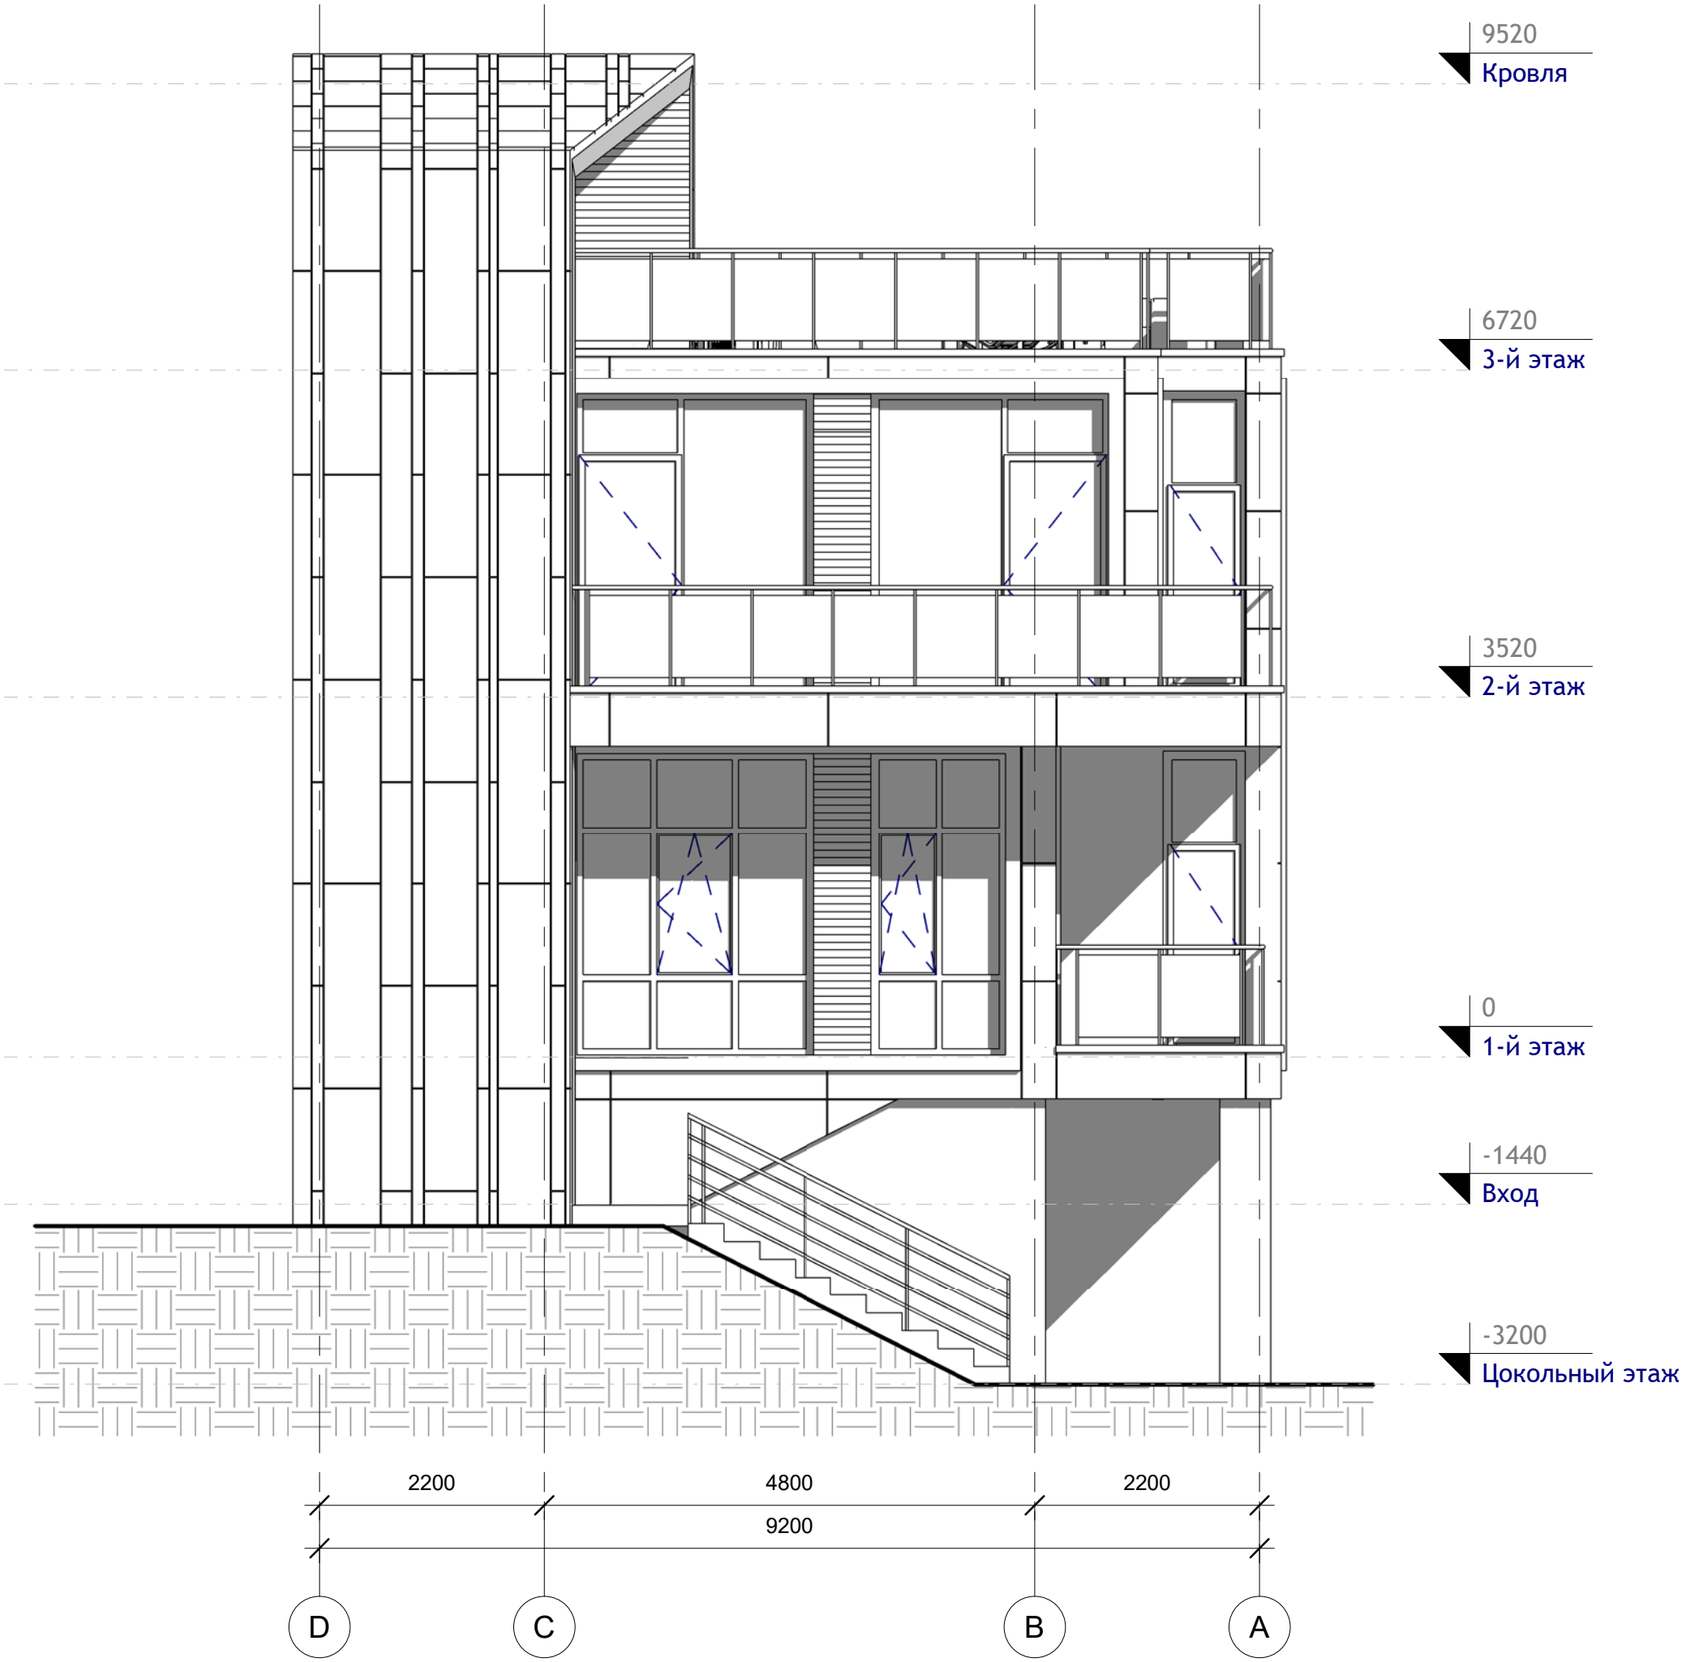

L.B.O.S.
DESIGN

№	Описание	Дата

Batumi Investment
SeaView Garden Villa. №3

Стадия (Stage): Эскиз (Concept)

Фасад в осях D-A

Номер проекта	0001
Дата	29.04.2021
Чертил	Сидорук О.
Проверил	

A112

Масштаб	1 : 60

5/10/2021 6:31:00 PM

L.B.O.S.
DESIGN

№	Описание	Дата

Batumi Investment
SeaView Garden Villa. №3

Стадия (Stage): Эскиз (Concept)

Перспектива

Номер проекта	0001
Дата	29.04.2021
Чертил	Сидорук О.
Проверил	

A113

Масштаб

5/10/2021 6:31:10 PM